

JONES DAY

680 ATLANTIC AVENUE, BOSTON, MA, 02111

TRANSACTION WINDOW - FLOORS 24



FRAMING SYSTEM(S) USED:

–FHC PASS THRU WINDOW SNOXXOBAC (OXXO)

MATERIALS:

A. UNEXPOSED FINISHES:
–MILL (ALUMINUM)

EXPOSED:
–BRITE ANODIZED
Ⓢ ALUMINUM TUBE Ⓢ TRANSACTION WINDOW

PERFORMANCE STANDARDS:

A. STRUCTURAL DESIGN IS BASED ON THE FOLLOWING LOADING CONDITIONS:
–INTERIOR WIND LOAD: 5 PSF

B. IF INCLUDED IN PROJECT CONTRACT, THEN STAMPED STRUCTURAL CALCULATIONS SHALL BE SUBMITTED ONLY AFTER DRAWINGS HAVE BEEN RETURNED EITHER STAMPED "APPROVED" OR "APPROVED AS NOTED"

ARCHITECT/G.C. NOTES:

A. TO SALEM GLASS "APPROVED" MEANS:

* ALL DETAILS, ON THE DRAWINGS HEREIN, HAVE BEEN REVIEWED FOR PROPER DESIGN AND AESTHETIC CONTENT. DETAILS, DIMENSIONS AND OTHER INFORMATION NOTED AS "PLEASE VERIFY", ON THE DRAWINGS HEREIN, HAVE BEEN REVIEWED, VERIFIED AND APPROVED.
* ALL CURTAIN WALL FINISHES, GLASS TYPES AND CURTAIN WALL HARDWARE APPLICABLE TO THE PROJECT HAVE BEEN SELECTED AND/OR ARE INDICATED CORRECTLY ON THE DRAWINGS HEREIN. ALSO, ALL SUBMITTED SAMPLES ARE APPROVED.
* AUTHORIZATION IS GIVEN TO ORDER AND FABRICATE MATERIAL AS SHOWN, OR NOTED, ON THE DRAWINGS HEREIN.
* DETAILS, DIMENSIONS AND OTHER INFORMATION NOTED AS "PLEASE VERIFY", THAT ARE NOT RESPONDED TO, ARE ASSUMED TO BE CORRECT AS SHOWN. (ANY FUTURE PROBLEMS DUE TO THESE VERIFICATIONS NOT BEING ADDRESSED WILL NOT BE THE RESPONSIBILITY OF SALEM GLASS COMPANY).

NOTE: THIS PROJECT WILL NOT BE RELEASED INTO PRODUCTION, AND MATERIALS WILL NOT BE ORDERED, UNTIL ALL APPROVAL REQUIREMENTS ARE MET AND OPEN CONTRACT/PRICE ITEMS ARE AGREED UPON.

B. ALL SHOP APPLIED AND INTERNAL SYSTEM SEALANTS USED FOR ALUMINUM FRAMING SYSTEMS FURNISHED AND INSTALLED BY SALEM GLASS SHALL BE DOWSIL / TREMCO SILICONE SEALANT. ARCHITECT AND/OR GC SHALL VERIFY COMPATIBILITY WITH AIR VAPOR BARRIER SYSTEMS AND/OR ANY OTHER PRODUCTS FURNISHED AND INSTALLED BY OTHERS THAT MAY COME INTO CONTACT WITH FRAMING SYSTEMS INSTALLED BY SALEM GLASS.

ARCHITECTURAL DWG. REF. SET

REVISION#: BULLETIN #10 DATE: 11/26/25

DRAWING RELEASE RECORD

SUBMISSION	DATE	STATUS	REVISION	DESCRIPTION/SHEETS
01	12/23/25	FOR APPROVAL	00	C201–C202, P201, E201, H201, V201
–	mm/dd/yy	–	1	
–	mm/dd/yy	–	2	
–	mm/dd/yy	–	3	
–	mm/dd/yy	–	4	
–	mm/dd/yy	–	5	
–	mm/dd/yy	–	6	
–	mm/dd/yy	–	7	

GENERAL NOTES:

1. STRUCTURAL STEEL AND CONCRETE DIMENSIONS ARE DERIVED FROM THE CONTRACT DRAWINGS AND ARE THE RESPONSIBILITY OF THE GENERAL CONTRACTOR.

2. FIELD DIMENSIONS AND/OR MEASUREMENTS ARE EXCLUDED FROM THIS WORK UNLESS SPECIFICALLY STATED OTHERWISE.

3. SALEM GLASS COMPANY WILL NOT ASSUME THE RESPONSIBILITY OF COORDINATION BETWEEN SALEM GLASS COMPANY'S DRAWINGS AND OTHER TRADE'S DRAWINGS.

4. ALL BUILDING ELEMENTS USED TO SUPPORT THE GLAZING SYSTEM ARE TO BE STRUCTURALLY SOUND AND PROVIDE ADEQUATE SUPPORT TO WITHSTAND LOADS IMPOSED BY THE GLAZING SYSTEM.

5. THE GLAZING SYSTEM HAS BEEN DESIGNED TO INCORPORATE, WITHOUT FAILURE OF MATERIALS OR PERMANENT DEFORMATION, A MAXIMUM LIVE LOAD DEFLECTION OF +/- 1/4".

6. ATTACHMENT OF ALL MATERIALS TO THE GLAZING SYSTEM IS STRICTLY PROHIBITED UNLESS SPECIFICALLY SHOWN ON APPROVED SHOP DRAWINGS.

7. ALL DISSIMILAR MATERIALS IN CONTACT WITH ALUMINUM MEMBERS ARE TO BE ISOLATED FROM THE ALUMINUM USING BITUMINOUS PAINT.

8. THESE DRAWINGS AND THE INFORMATION CONTAINED HEREIN ARE THE SOLE EXPRESSED PROPERTY OF SALEM GLASS COMPANY. USE OF THESE DRAWINGS WITHOUT THE PERMISSION OF SALEM GLASS COMPANY SHALL BE CAUSE FOR LEGAL RECOURSE BY SALEM GLASS COMPANY.

9. REQUESTS FOR INFORMATION (RFI'S) DELAYED OR NOT ANSWERED COULD AFFECT THE START OF FABRICATION. IN THIS CASE, PROMISED DELIVERY DATES CANNOT BE GUARANTEED.

10. THESE DRAWINGS ARE BASED UPON SALEM GLASS COMPANY'S INTERPRETATION OF THE CONTRACT DOCUMENTS. DUE DILIGENCE HAS BEEN MADE TO ELIMINATE ALL ERRORS. HOWEVER, SINCE THE POSSIBILITY OF ERRORS EXISTS, SALEM GLASS COMPANY ASSUMES ONLY THE RESPONSIBILITY OF MANUFACTURING THE GLAZING SYSTEM IN ACCORDANCE WITH APPROVED SHOP DRAWINGS.

11. APPROVAL OF THESE DRAWINGS BY THE ARCHITECT SHALL CONSTITUTE ACCEPTANCE OF ALL DEVIATIONS SHOWN HEREIN.

12. SALEM GLASS COMPANY IS NOT RESPONSIBLE FOR ERRORS RESULTING FROM THE USE OF THESE DRAWINGS BY OTHER TRADES.

13. TO MAINTAIN SCHEDULE, FIRST SUBMISSION OF SHOP DRAWINGS MIGHT ONLY INCLUDE A PRELIMINARY STRUCTURAL ANALYSIS. FOR THIS REASON, SALEM GLASS COMPANY RESERVES THE RIGHT TO CHANGE FASTENER SIZES, WALL THICKNESS, ANCHOR SIZE, ETC., UPON FORMALIZING THE STRUCTURAL ANALYSIS AND TO IMPROVE THE PERFORMANCE OF THE GLAZING SYSTEM. THESE CHANGES WILL BE INTERNAL CHANGES TO THE SYSTEM AND WILL NOT VISUALLY AFFECT THE SYSTEM. IF VISUAL CHANGES ARE REQUIRED, THE ARCHITECT AND GENERAL CONTRACTOR WILL BE NOTIFIED.

14. SALEM GLASS WILL ONLY INSTALL ITS MATERIALS BASED ON BUILDING CONTROL BENCHMARKS PROVIDED BY THE GENERAL CONTRACTOR. SALEM GLASS WILL NOT INSTALL ITS MATERIALS BASED ON OTHER SUBCONTRACTOR'S LAYOUTS OR INSTALLED WORK.

INFILL SCHEDULE

MARK	INFILL DESCRIPTION
GL4	¼" CLEAR TEMPERED Ⓢ PASS THRU WINDOW
ARCH GL	
ARCH GL	
ARCH GL	
ARCH GL	
ARCH GL	
ARCH GL	

DOOR SWING DIAGRAM

INTERIOR

INSWING

RH INSWING

RH OUTSWING

OUTSWING

EXTERIOR

SYMBOLS

Ⓢ	CENTER LINE
Ⓢ	ELEVATION MARK
Ⓢ	WORK POINT (SUBSTRUCTURE)
Ⓢ	WORK POINT (PANEL)
Ⓢ	JAMB
Ⓢ OR Ⓢ	OUTSIDE 90 DEGREE CORNERS
Ⓢ OR Ⓢ	INSIDE 90 DEGREE CORNERS
Ⓢ OR Ⓢ	90 DEGREE 'T' Ⓢ JAMB
Ⓢ OR Ⓢ	90 DEGREE 'T' INTERSECTION
Ⓢ OR Ⓢ	OUTSIDE ACUTE CORNERS
Ⓢ OR Ⓢ	INSIDE ACUTE CORNERS
Ⓢ OR Ⓢ	OUTSIDE OBTUSE CORNERS
Ⓢ OR Ⓢ	INSIDE OBTUSE CORNERS
Ⓢ	REVISION MARK W/ NUMBER
Ⓢ Ⓢ	DETAIL NUMBER } SHEET NUMBER }DETAIL CALLOUT
Ⓢ	EXPANSION MULLION
Ⓢ OR Ⓢ	MEDIUM OR HEAVY WEIGHT MULLION
Ⓢ	SPLICE JOINT LOCATION
Ⓢ	INFILL TYPE
Ⓢ	FASTENER TYPE
Ⓢ	DOOR NUMBER
Ⓢ	DEAD LOAD ANCHOR
Ⓢ	WIND LOAD ANCHOR
Ⓢ OR Ⓢ	WINDLOAD ANCHOR (ELEVATION)
Ⓢ OR Ⓢ	DEADLOAD ANCHOR (ELEVATION)
Ⓢ	GRAIN DIRECTION (VERTICAL)
Ⓢ	GRAIN DIRECTION (HORIZONTAL)
Ⓢ QTY:	PANEL TAG

TABLE OF CONTENTS

PAGE NUMBERS	DESCRIPTION
C201–C202	COVER SHEET / GENERAL INFORMATION
P201	FLOOR PLANS
E201	ELEVATIONS
H201	HORIZONTAL DETAILS
V201	VERTICAL DETAILS

ABBREVIATIONS

AFF	ABOVE FINISH FLOOR
ALUM	ALUMINUM
ARCH	ARCHITECT
BO	BOTTOM OF
BOSTL	BOTTOM OF STEEL
CJ	CAULK JOINT
CONT	CONTINUOUS
DTL	DETAIL
DF	DOOR FRAME
DFO	DOOR FRAME OPENING
DL	DEAD LOAD
DLO	DAYLIGHT OPENING
DLR	DEAD LOAD REACTION
DO	DOOR OPENING
EO	EDGE OF
FMD	FORMED
FO	FACE OF
FOG	FACE OF GLASS
FS	FRAME SIZE
GB	GLASS BITE
GC	GENERAL CONTRACTOR
GS	GLASS SIZE
HORZ	HORIZONTAL
HP	HIGH POINT
LP	LOW POINT
MF	MIRROR FACE
ML	MULLION LENGTH
MO	MASONRY OPENING
MS	MEDIUM STYLE
MULL	MULLION
N/A	NOT APPLICABLE
NBSGC	NOT BY SALEM GLASS COMPANY
NIC	NOT IN CONTRACT
NOM	NOMINAL
NTS	NOT TO SCALE
OPP	OPPOSITE HAND
PF	PANEL FACE
PS	PANEL SIZE
PSD	PANEL SYSTEM DEPTH
REF	REFERENCE
REQ'D	REQUIRED
RO	ROUGH OPENING
SFS	SILL FLASHING SIZE
SGC	SALEM GLASS COMPANY
SIM	SIMILAR
SPD	SPANDREL
SS	STAINLESS STEEL
STL	STEEL
TBD	TO BE DETERMINED
THK	THICK
TOS	TOP OF SLAB
TOSTL	TOP OF STEEL
TYP	TYPICAL
UNO	UNLESS NOTED OTHERWISE
VIF	VERIFY IN FIELD
VIS	VISION
WL	WIND LOAD
WLR	WIND LOAD REACTION
WP	WORK POINT

PROJECT
JONES DAY BOSTON FIT–OUT

ARCHITECT
ELKUS MANFREDI

GENERAL CONTRACTOR
STRUCTURE TONE

DESCRIPTION

BY

DATE

REV

PROJ NO

8833

DATE

12/23/25

DRAWN

SM

CHECKED

MO/SB

FILE NAME

8833 c 1

SCALE

NO SCALE

SHEET NUMBER

C201

INTERIOR GLAZING FASTENER INDEX

FASTENER#:	1	IMAGE:	
PART#:	FASTENAL #1173058		
DESCRIPTION:		#12-11 X 2" PFH TYPE-A SMS *18-8SS	

FASTENER#:	2	IMAGE:	
PART#:	FASTENAL #1173006		
DESCRIPTION:		#6-18 x 3/4" PFH TYPE-A SMS *18-8SS	



SALEM GLASS COMPANY
3 Technology Way, Salem, MA 01970
Phone# (978)744-5177 Fax# (978)745-4036

PROJECT	JONES DAY BOSTON FIT-OUT	REV	DATE	BY	DESCRIPTION
ARCHITECT	ELKUS MANFREDI				
GENERAL CONTRACTOR	STRUCTURE TONE				
PROJ NO	8833				
DATE	12/23/25				
DRAWN	SM				
CHECKED	MO/SB				
FILE NAME	8833 c 1				
SCALE	NO SCALE				
SHEET NUMBER	C202				



SALEM GLASS COMPANY
3 Technology Way, Salem, MA 01970
Phone# (978)44-5517 Fax# (978)45-4036

DESCRIPTION

BY

DATE

REV

PROJECT
JONES DAY BOSTON FIT-OUT

ARCHITECT


ELKUS MANFREDI

GENERAL CONTRACTOR

STRUCTURE TONE

PROJ NO	8833
DATE	12/23/25
DRAWN	SM
CHECKED	MO/SB
FILE NAME	8833 p 1
SCALE	1/8"=1'-0"

SHEET
NUMBER
P201

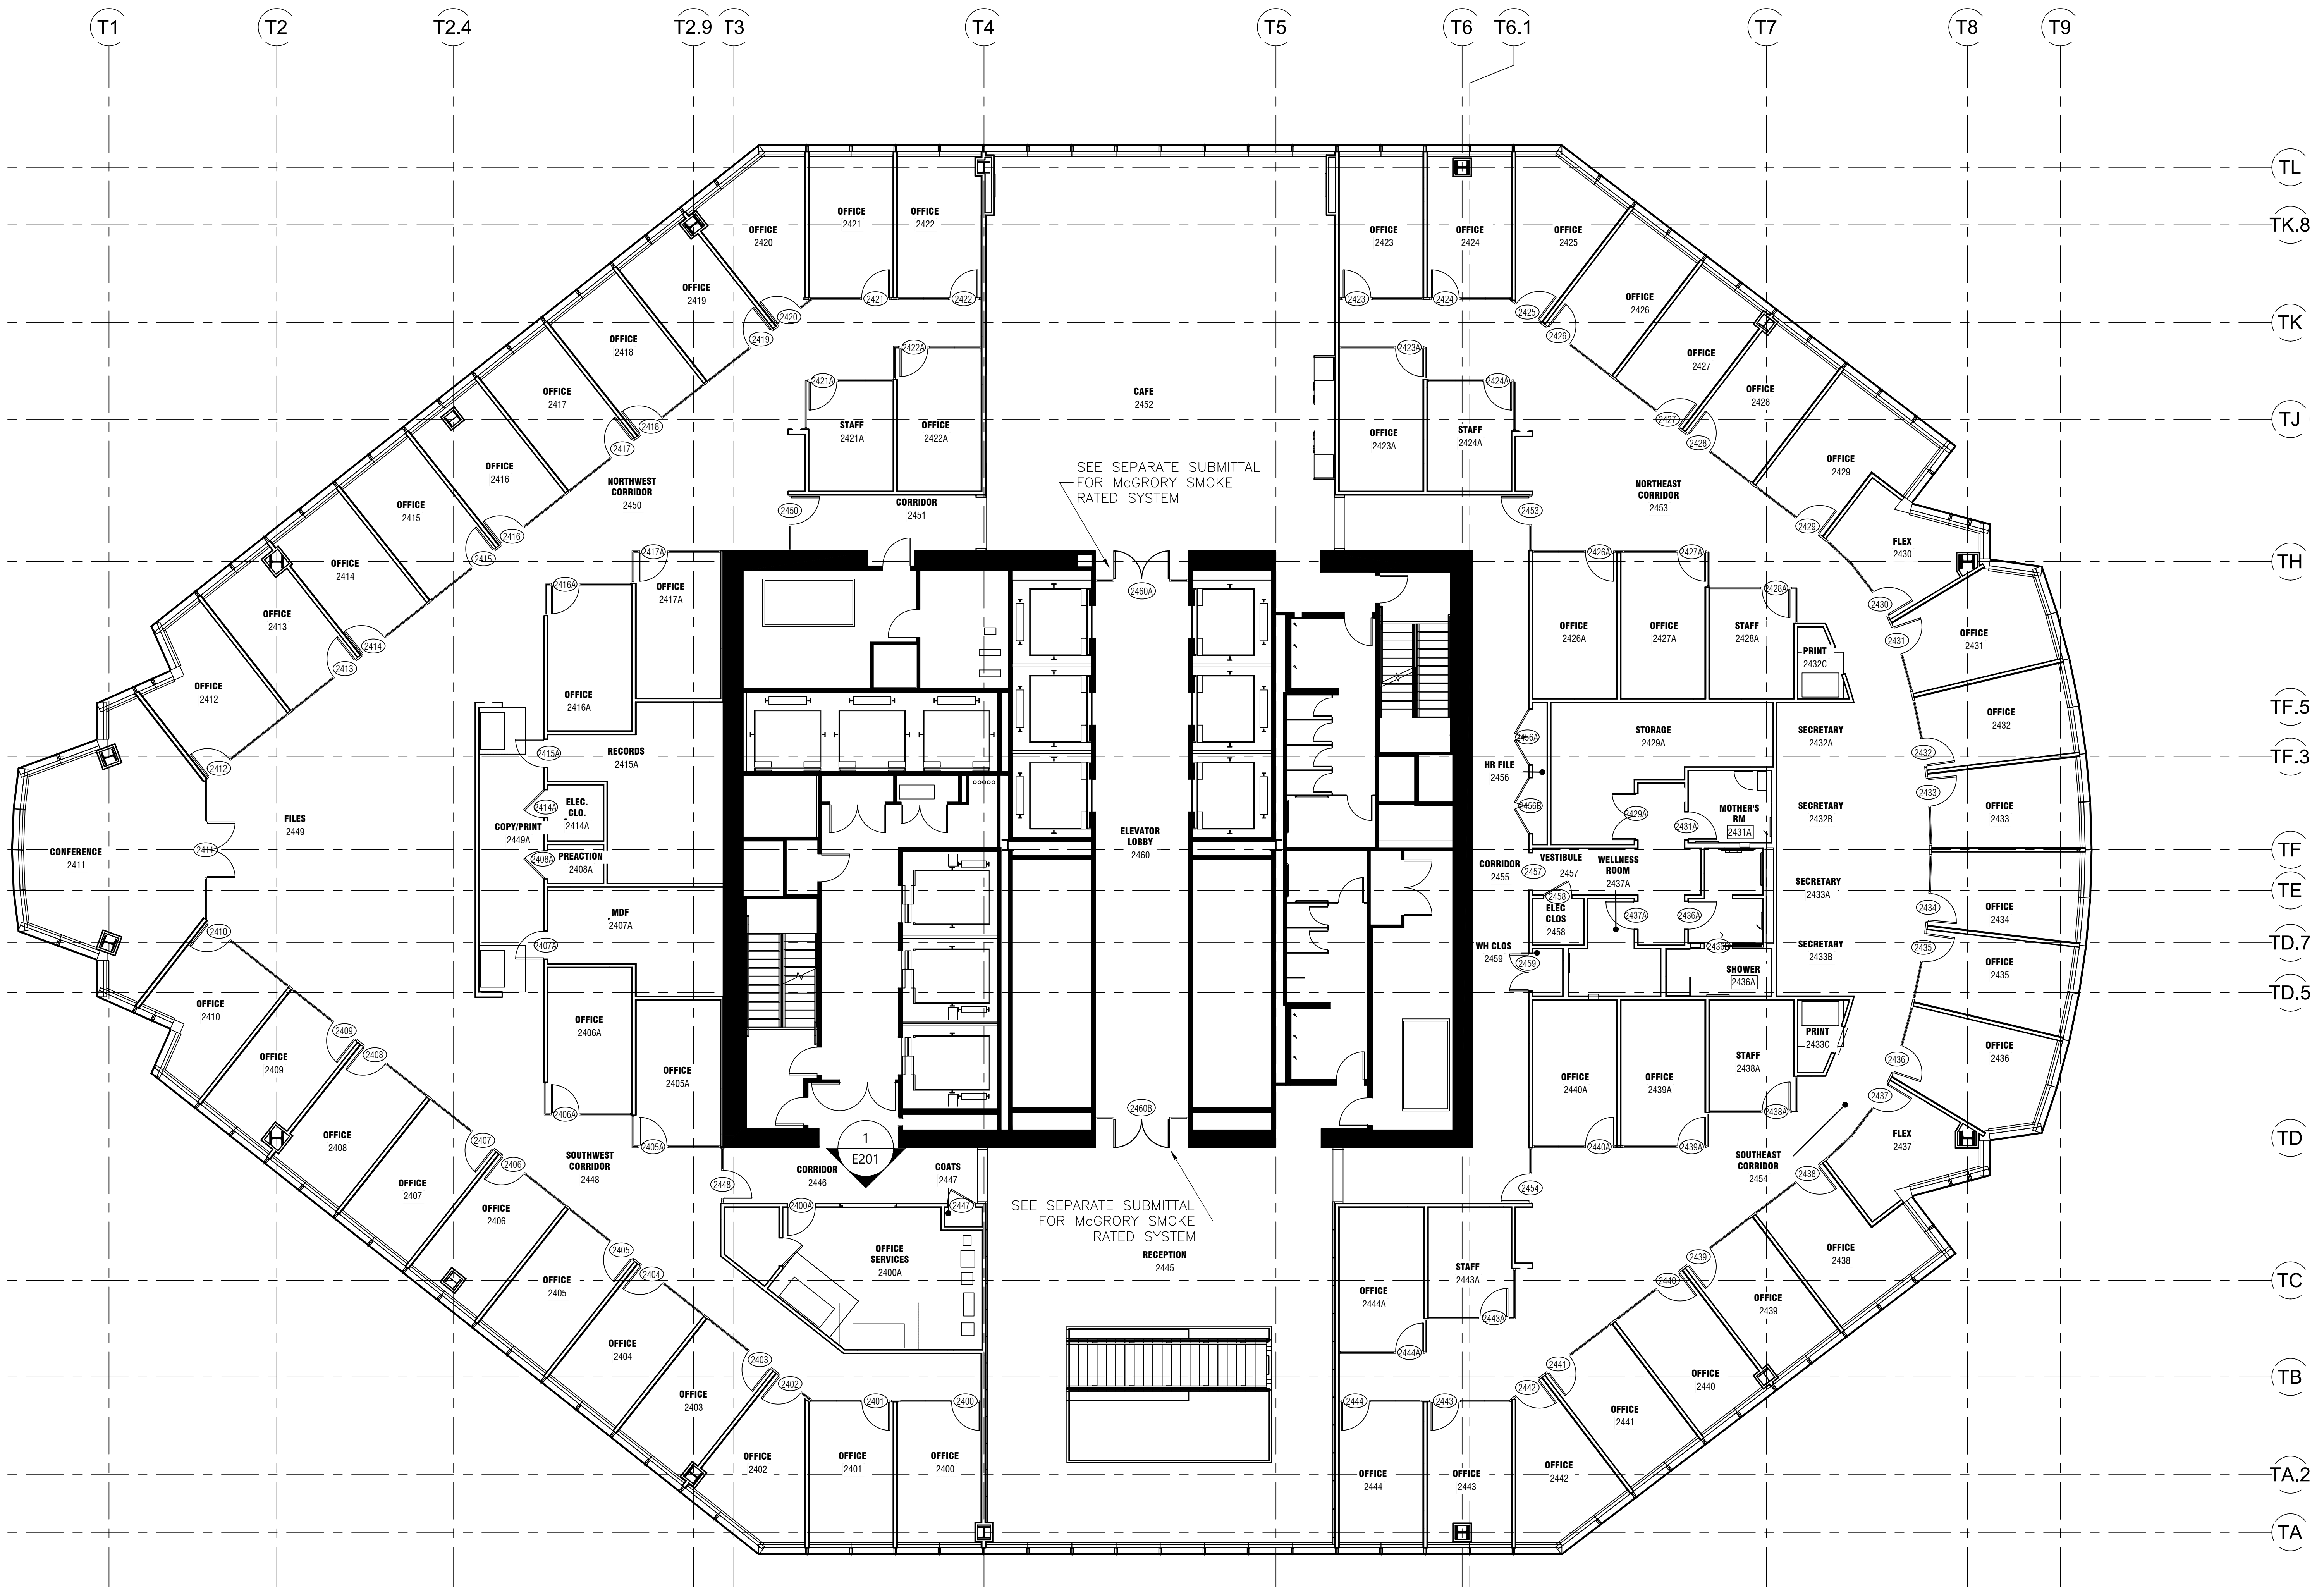


1 PLAN LEVEL 24
ARCH REF: 1/A124



< GL4

ALL DIMENSIONS TO BE
VERIFIED IN FIELD BY SGC
PRIOR TO FABRICATION

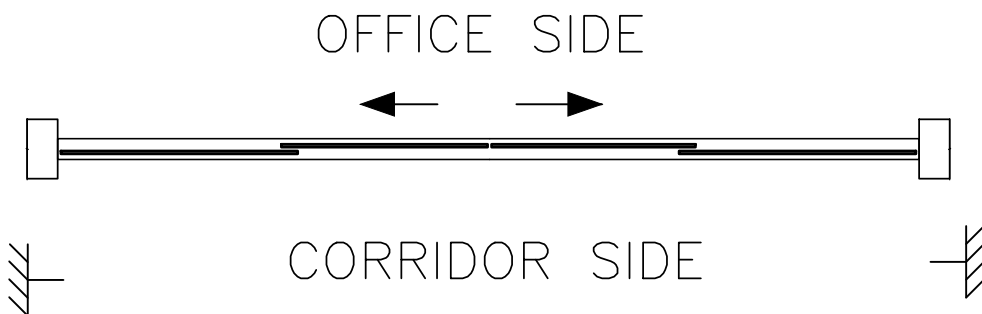

1


QUANTITY: (1) THUS
ARCH REF: 5/A715
@ OFFICE SERVICES 2400A

DESCRIPTION


PROJECT JONES DAY BOSTON FIT-OUT

PROJ NO	8833
DATE	12/23/25
DRAWN	SM
CHECKED	MO/SB
FILE NAME	8833 e 1
SCALE	1/2"=1'-0"

SHEET NUMBER	E201
-----------------	------

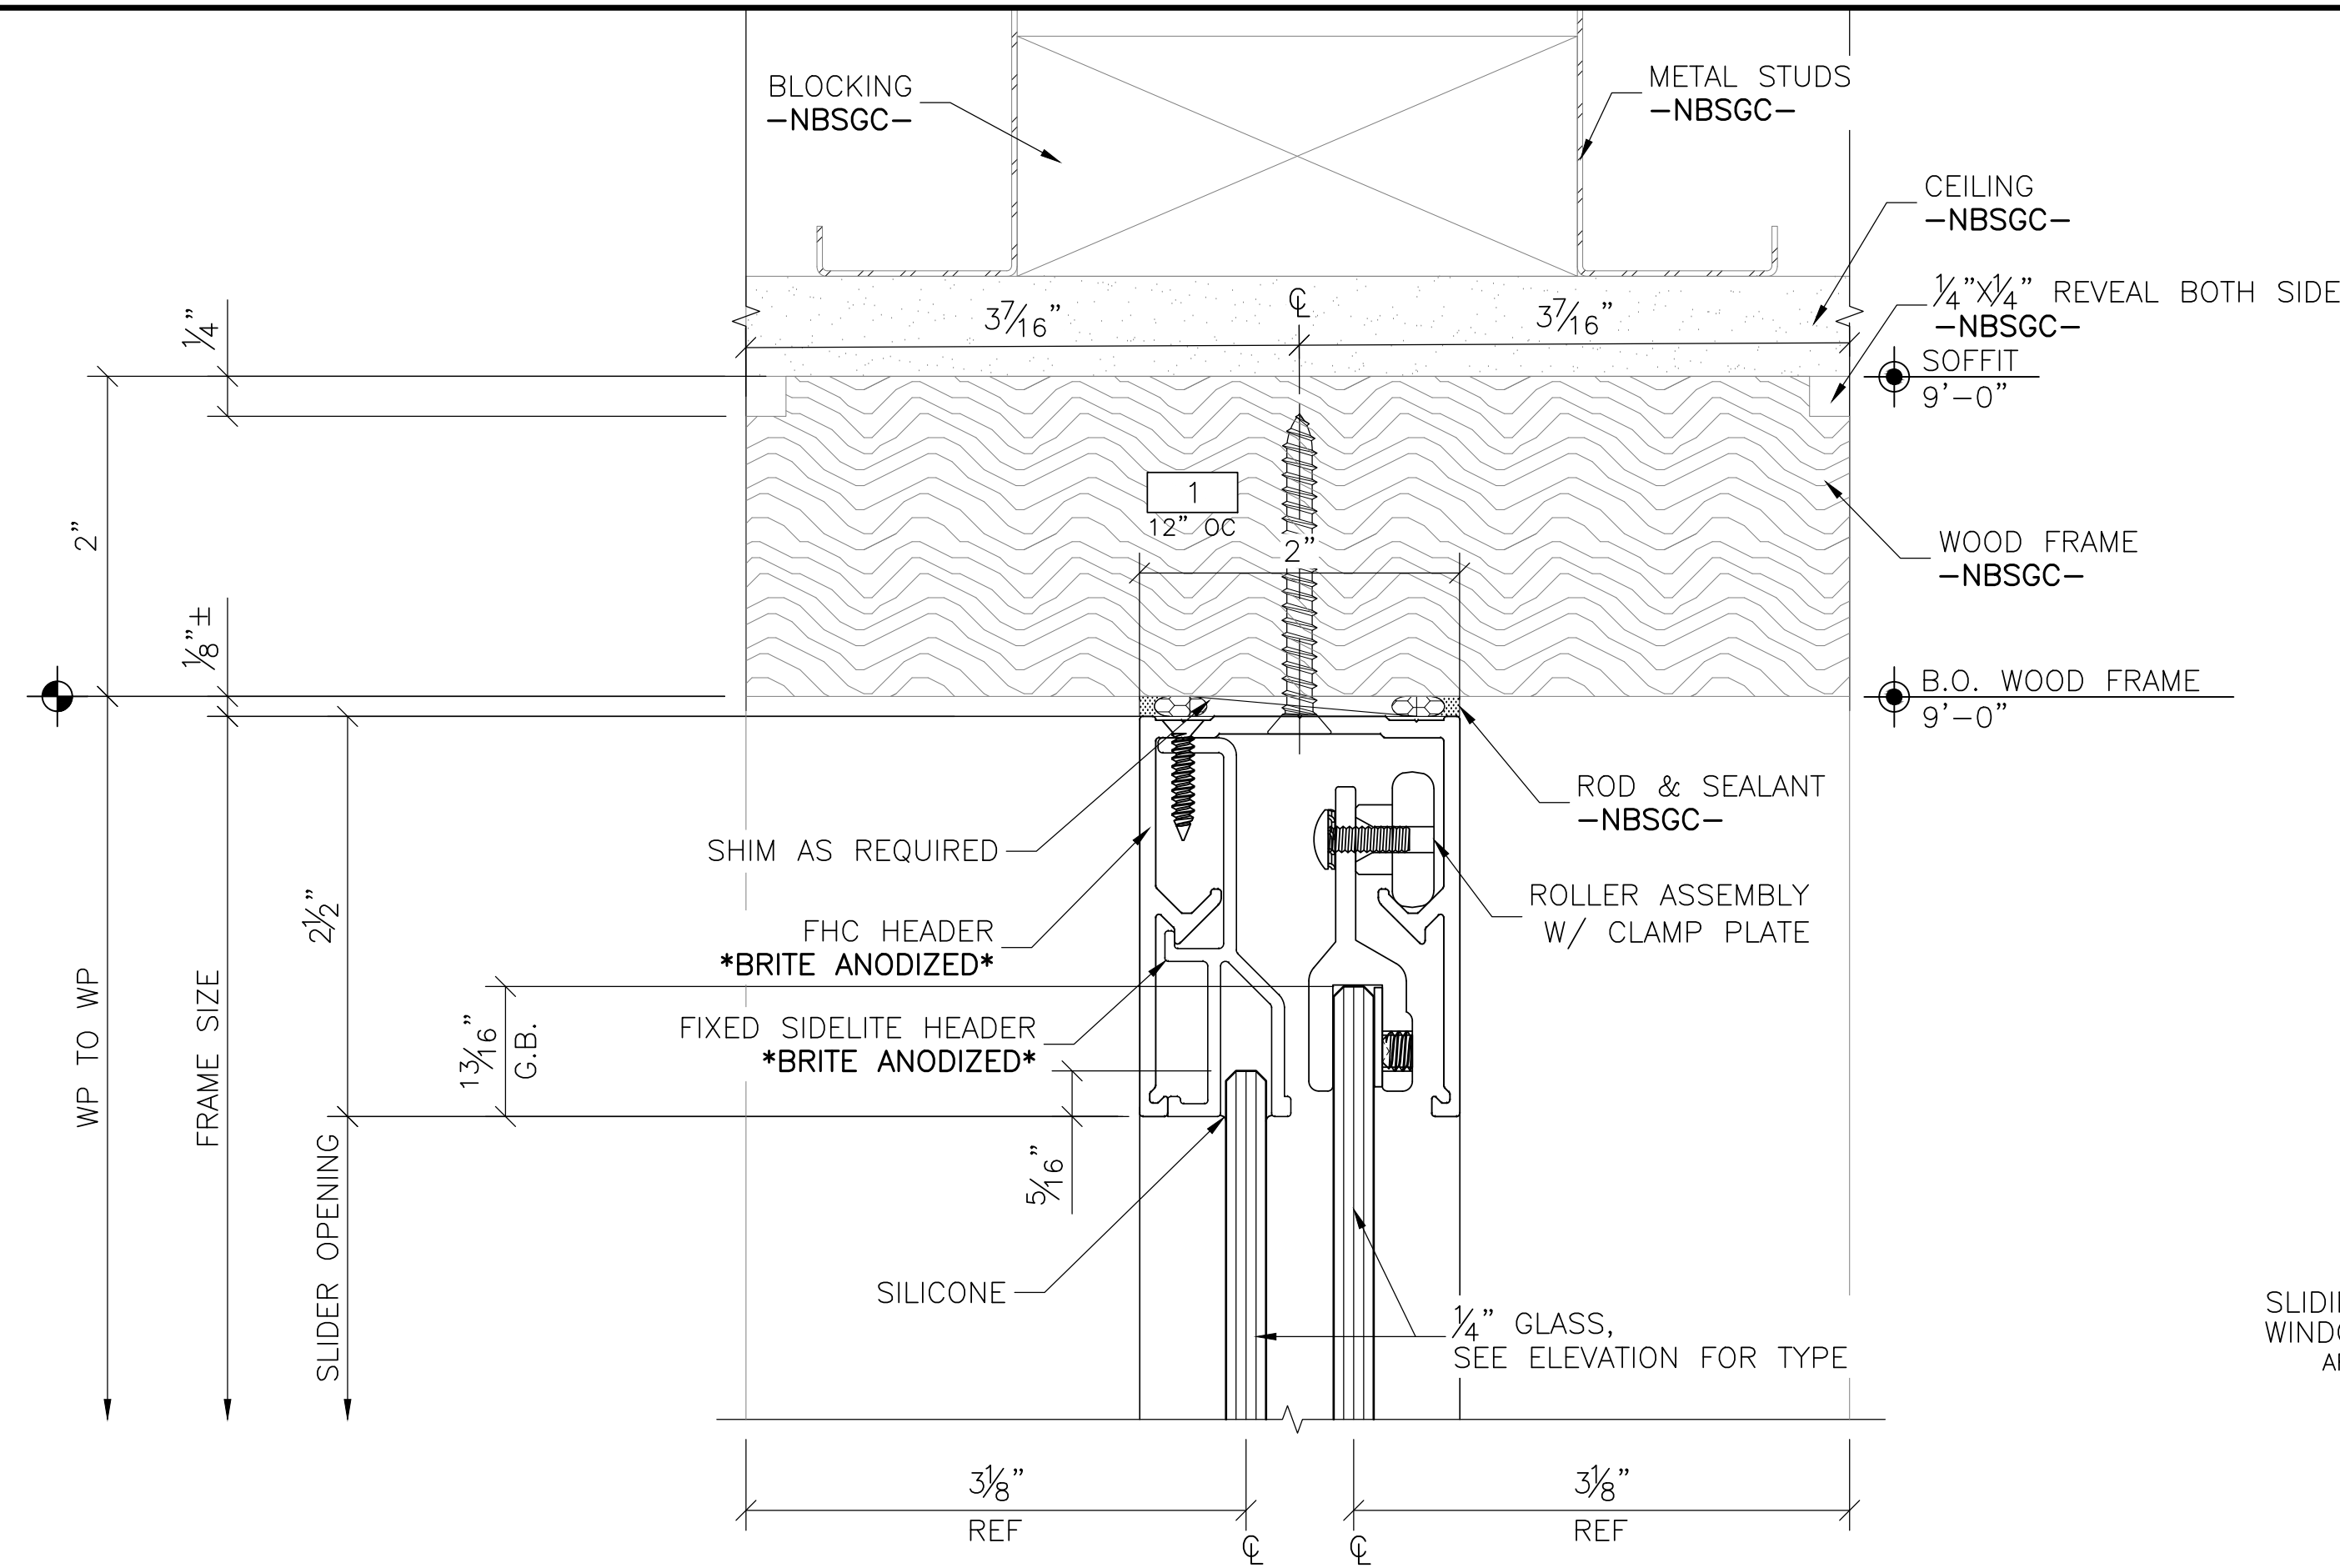

H1
SLIDING TRANSACTION
WINDOW HEAD DETAIL
ARCH REF: NONE

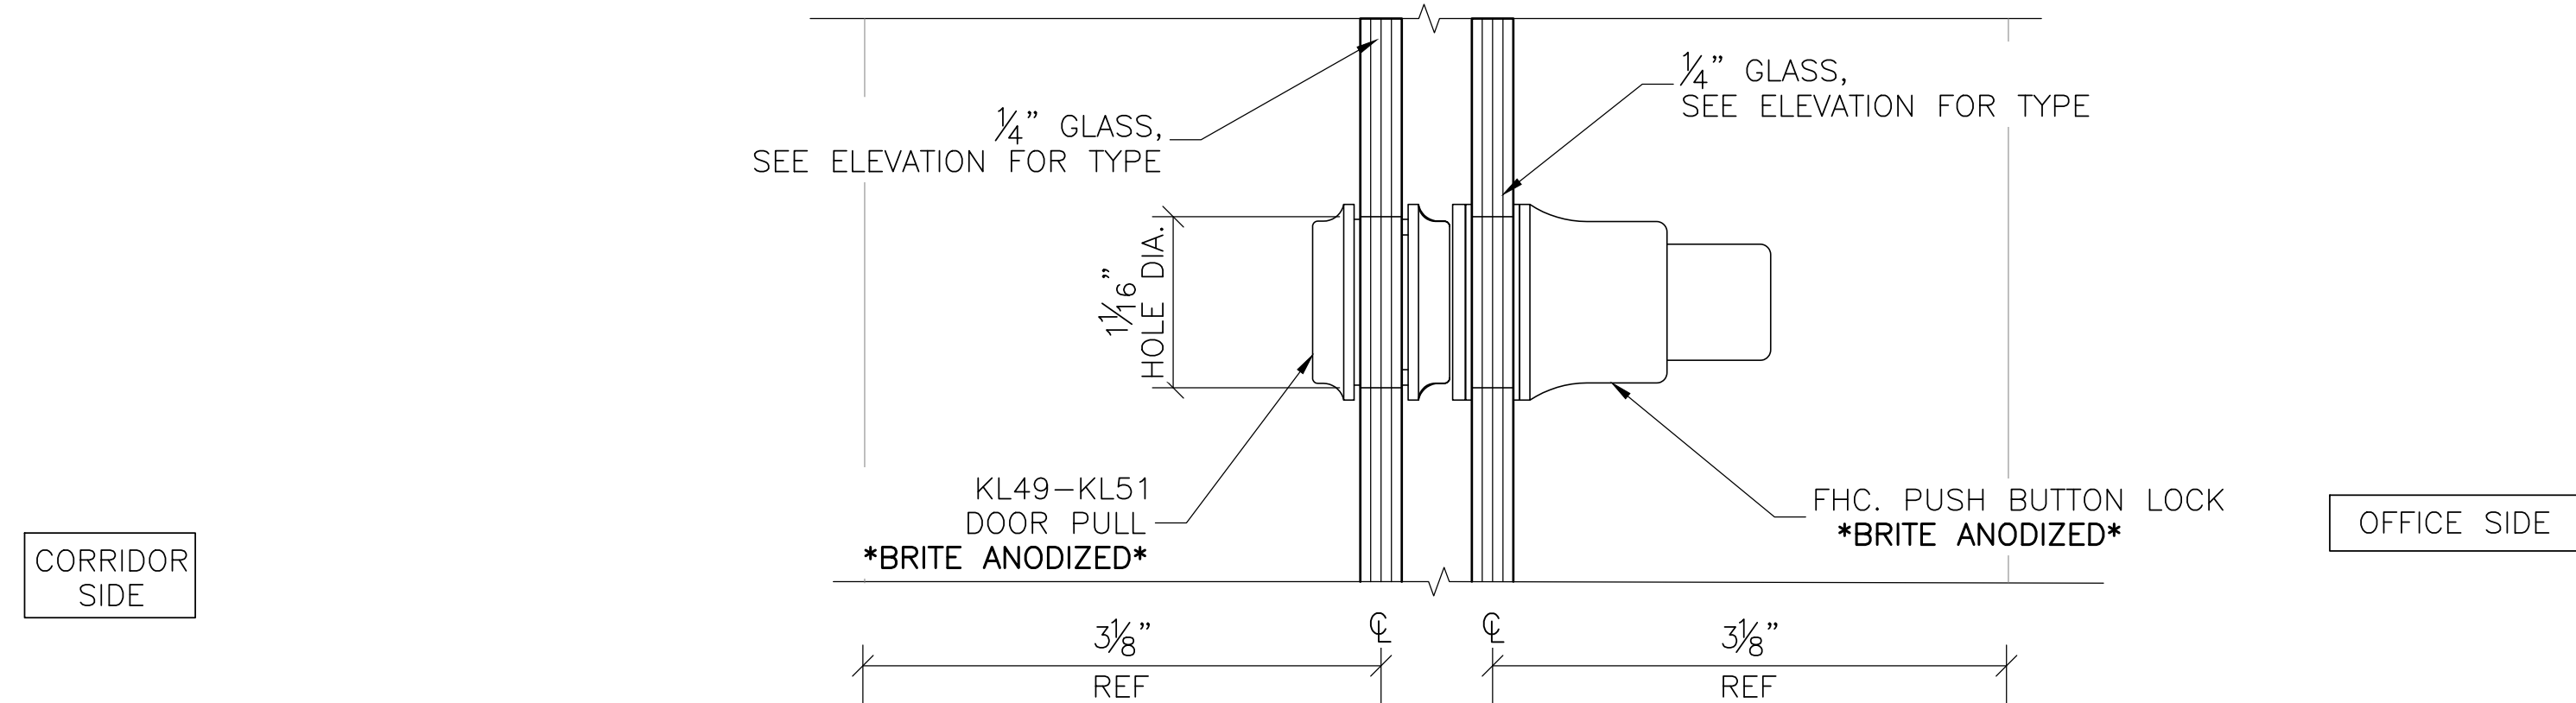

H2
SLIDING TRANSACTION
WINDOW SILL DETAIL
ARCH REF: NONE



SALEM GLASS COMPANY
3 Technology Way, Salem, MA 01970
Phone# (978)744-5177 Fax# (978)745-4036

REV	DATE	BY	DESCRIPTION

PROJECT	JONES DAY BOSTON FIT-OUT
ARCHITECT	ELKUS MANFREDI
GENERAL CONTRACTOR	STRUCTURE TONE

PROJ NO	8833
DATE	12/23/25
DRAWN	SM
CHECKED	MO/SB
FILE NAME	8833 h 1
SCALE	FULL SCALE


SHEET NUMBER	H201
--------------	------

REV	DATE	BY	DESCRIPTION


PROJECT	JONES DAY BOSTON FIT-OUT
ARCHITECT	ELKUS MANFREDI
GENERAL CONTRACTOR	STRUCTURE TONE

PROJ NO	8833
DATE	12/23/25
DRAWN	SM
CHECKED	MO/SB
FILE NAME	8833 v 1
SCALE	FULL SCALE


SHEET NUMBER	V201
--------------	------

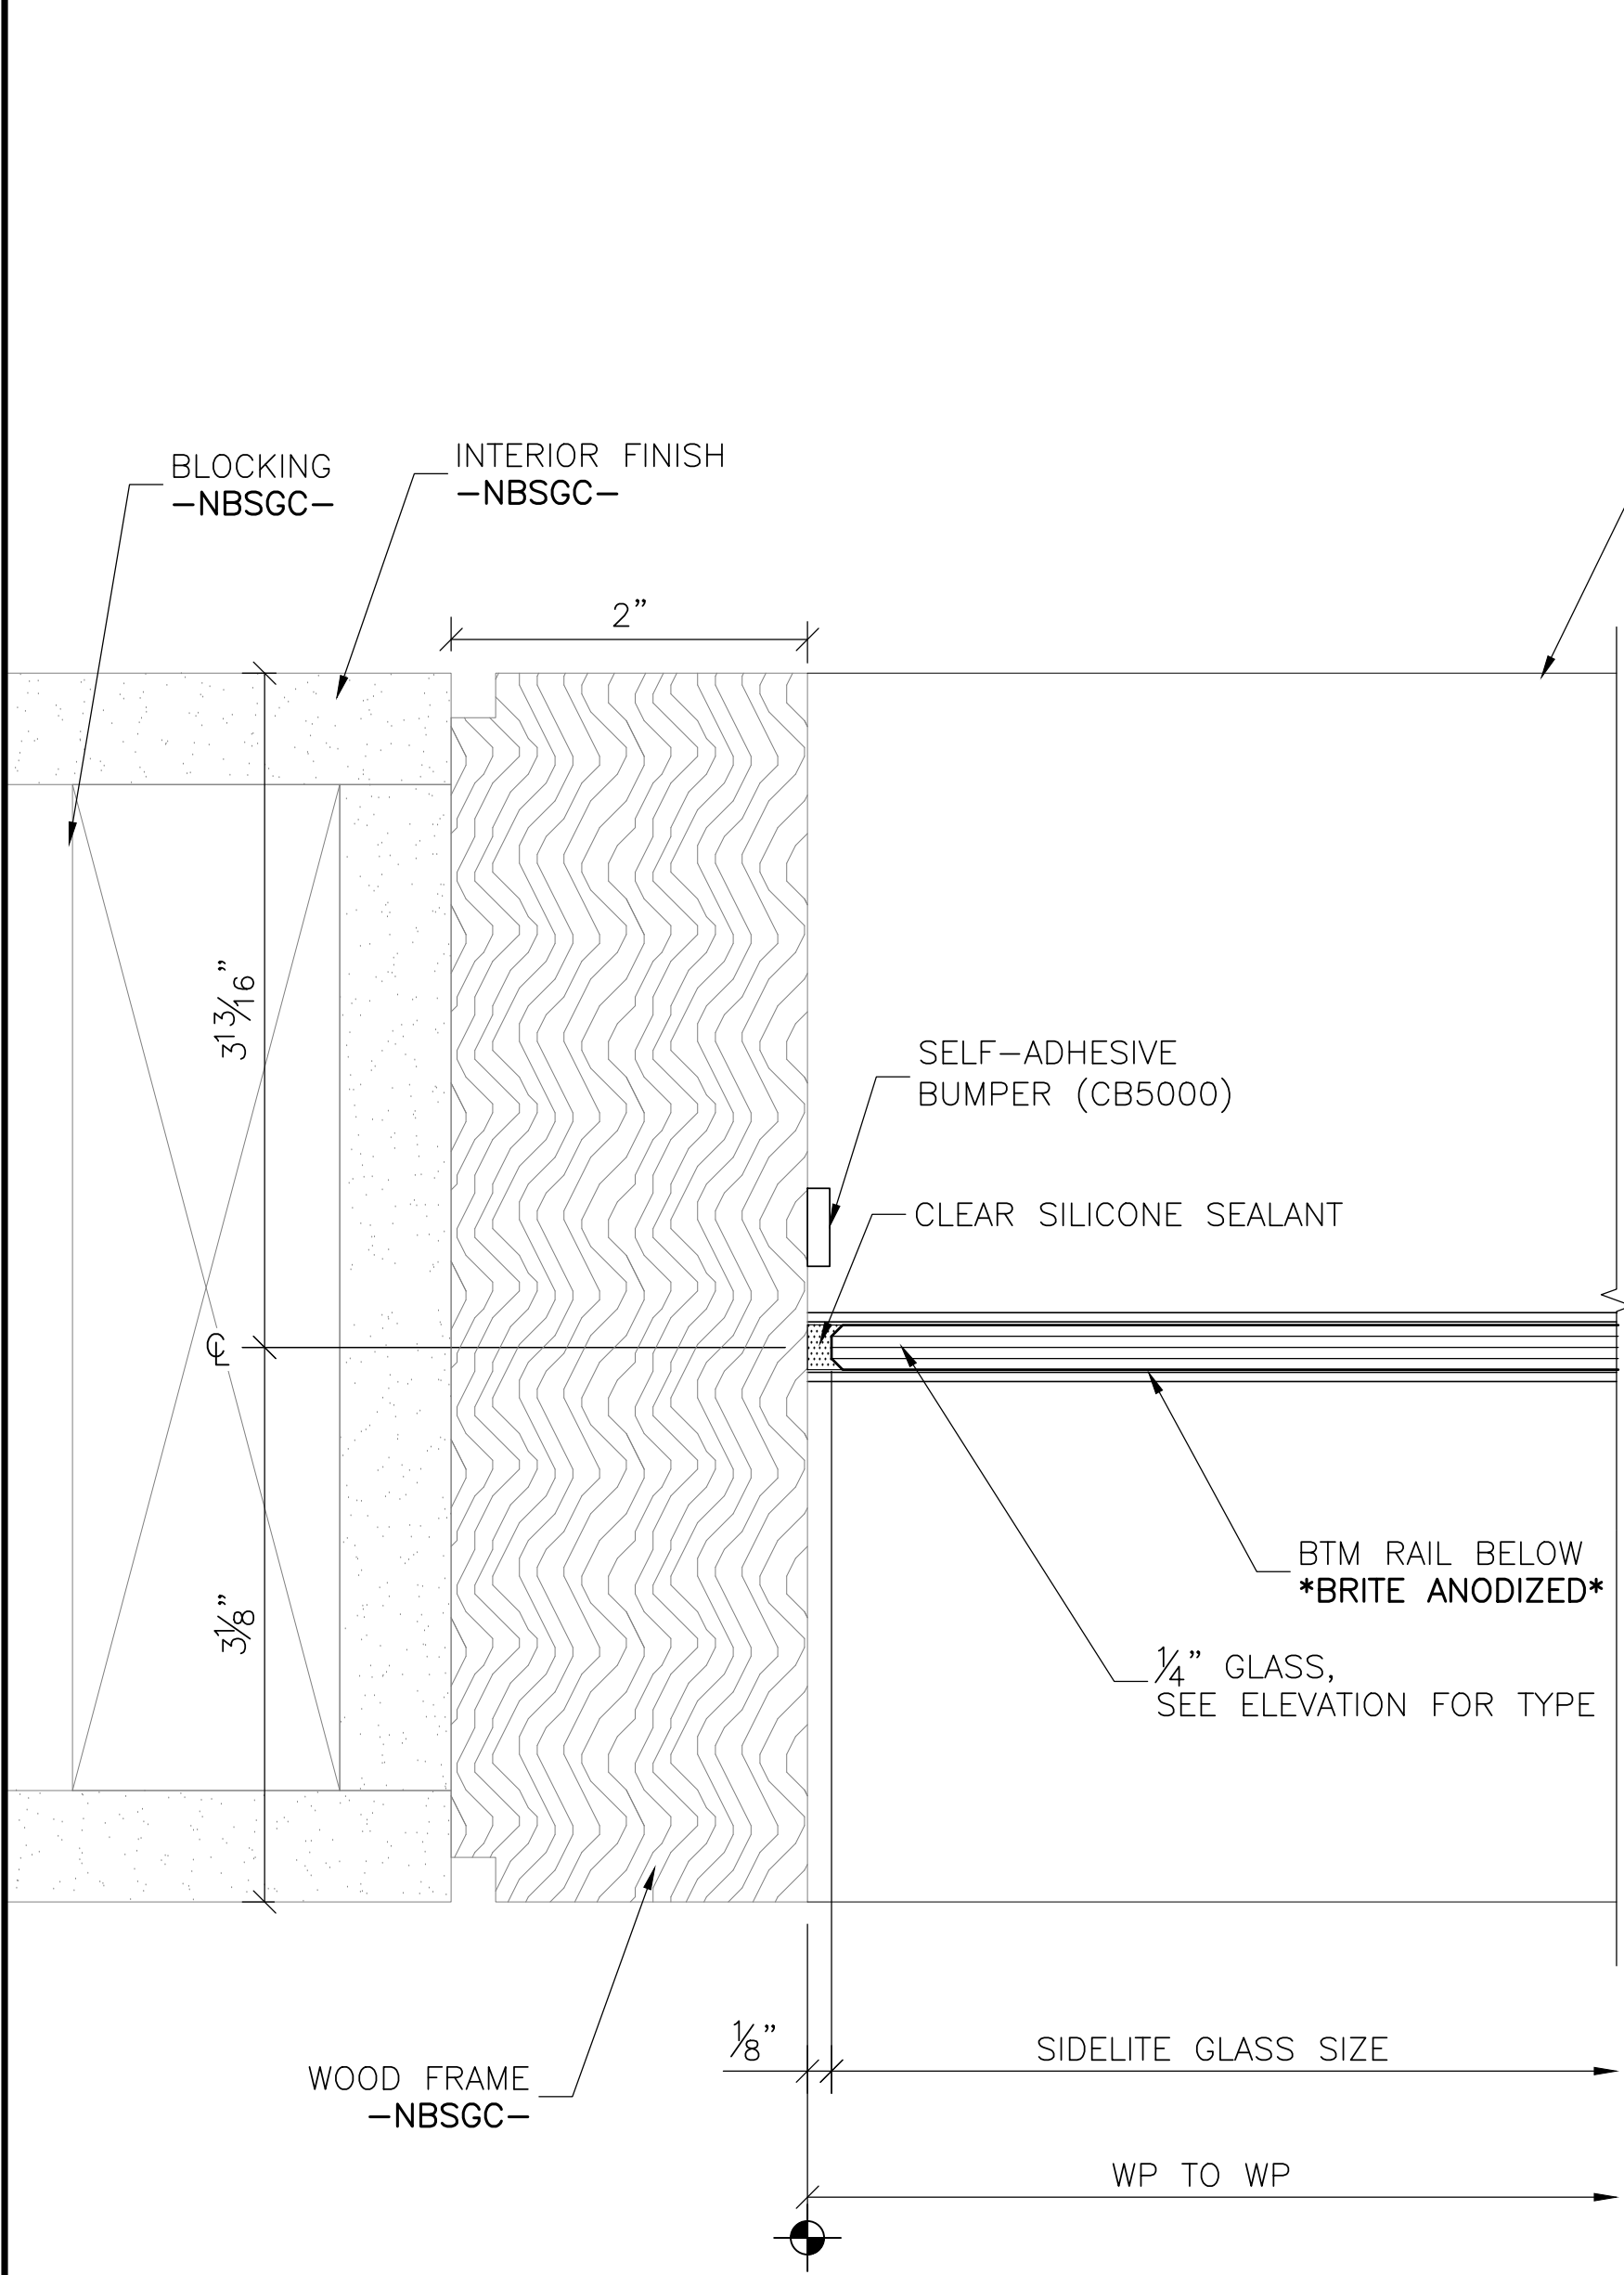

V1
PASS THRU WINDOW
JAMB DETAIL
ARCH REF: NONE

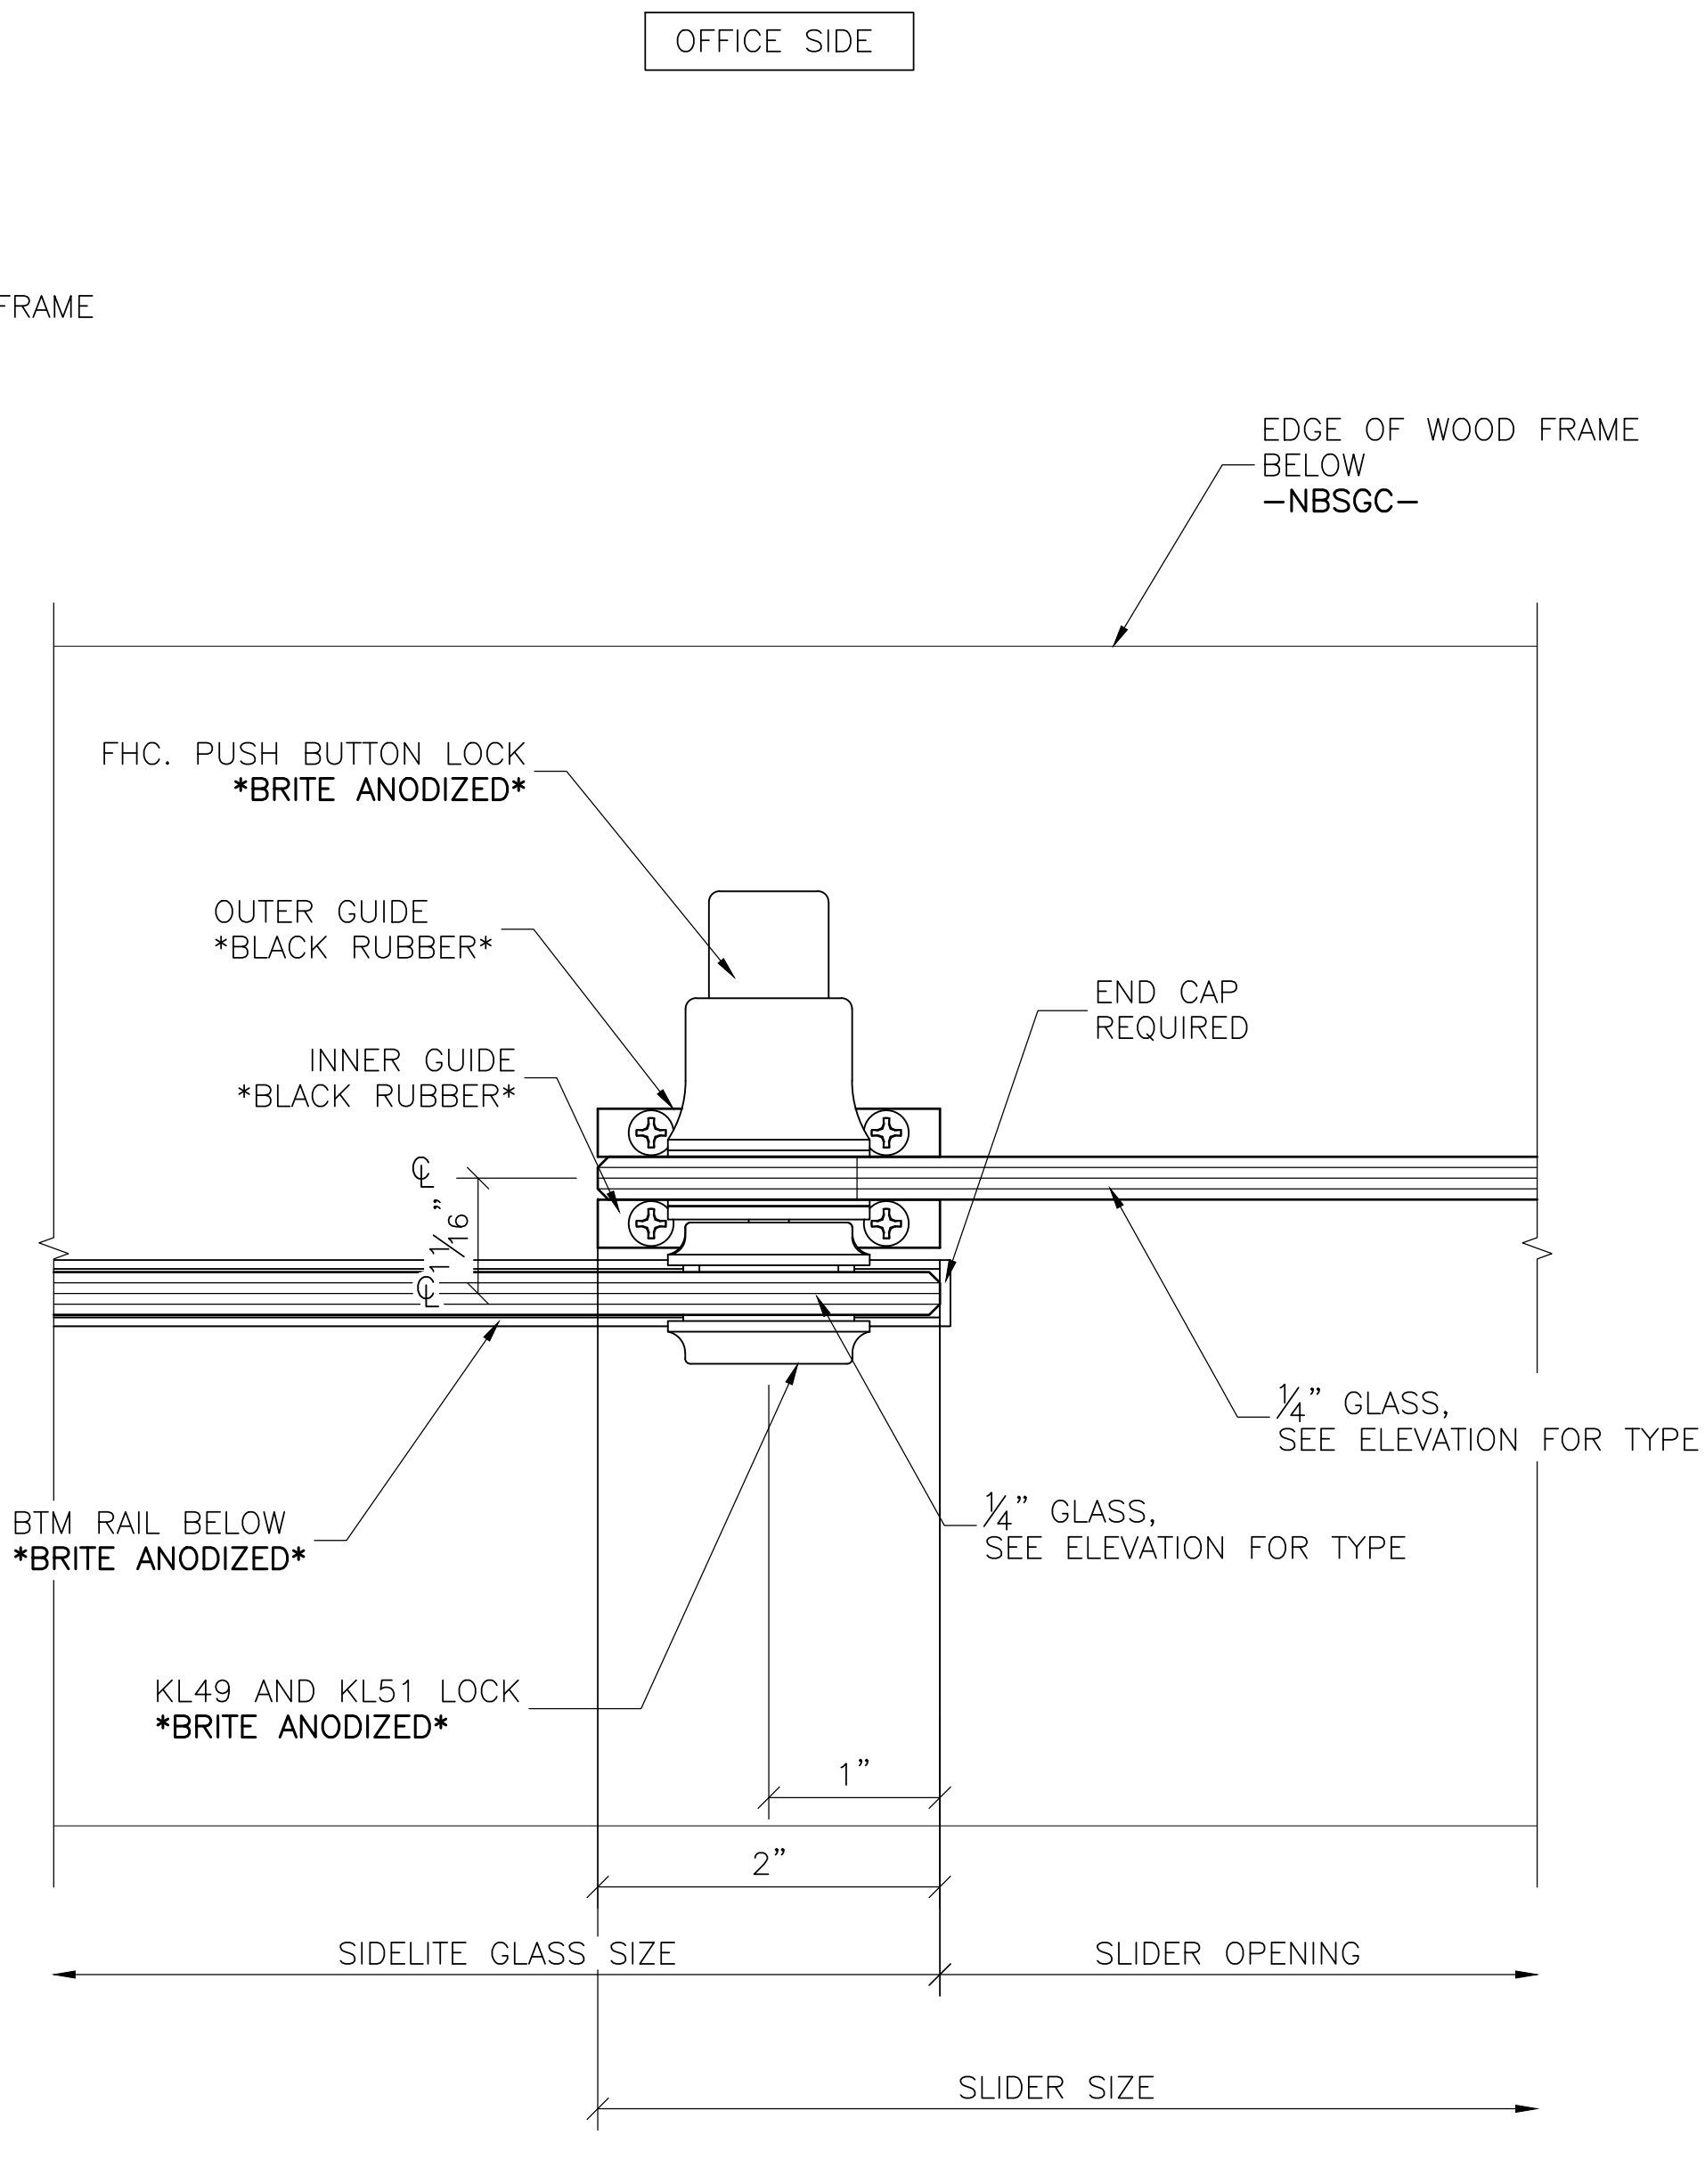

V2
PASS THRU WINDOW
SIDELITE-DOOR DETAIL
ARCH REF: NONE

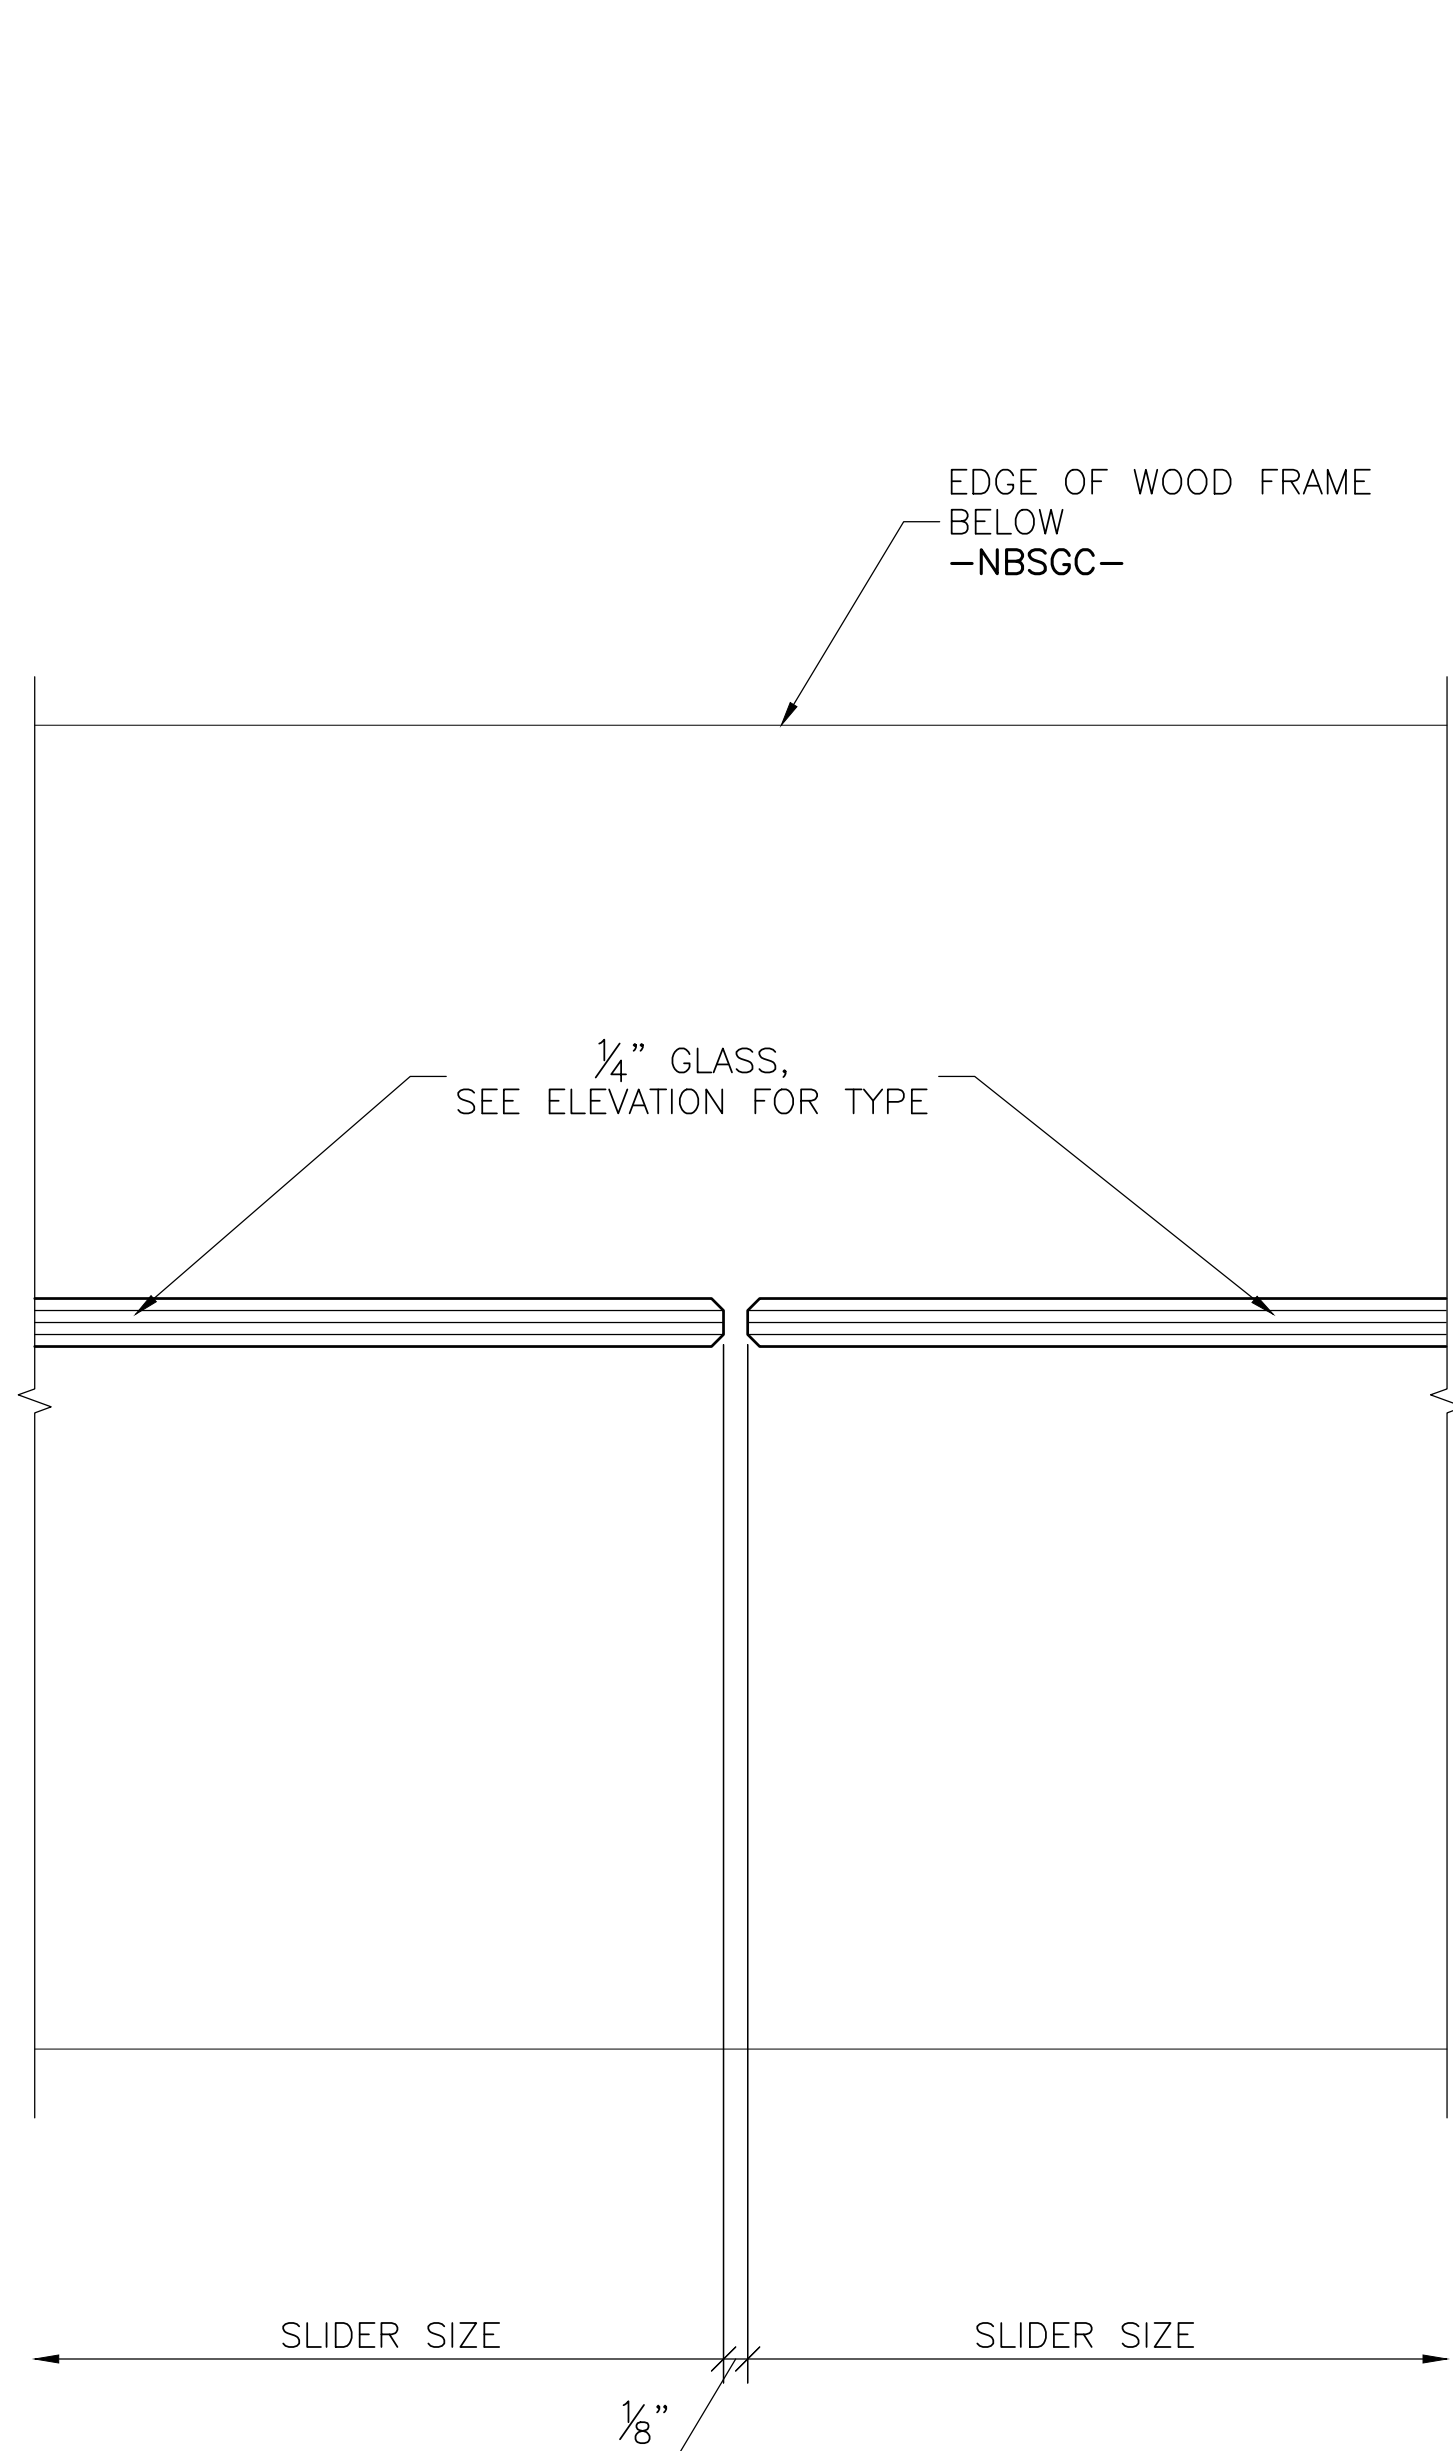

V3
PASS THRU WINDOW
MEETING DETAIL
ARCH REF: NONE