



INTERIOR GLAZING

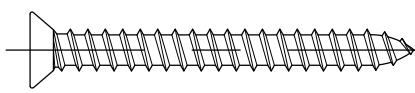


PROJECT	KIRKLAND & ELLIS			
ARCHITECT	HO&K			
GENERAL CONTRACTOR	STRUCTURE TONE, INC			
PROJ NO	8901			
DATE	5/4/26			
DRAWN	SM			
CHECKED	SB/MO			
FILE NAME	8109 c 1			
SCALE	NO SCALE			
SHEET NUMBER	C101			
REV	DATE	BY	DESCRIPTION	

INTERIOR GLAZING FASTENER INDEX

FASTENER#:	1	IMAGE: 
PART#:		
FASTENAL #1173058		
DESCRIPTION:		#12-11 X 2" PFH TYPE-A SMS *18-8SS

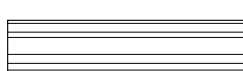FASTENER#:	2	IMAGE: 	SGC INVENTORY
PART#: FASTENAL #50985			
DESCRIPTION: #10/#12 GREEN MASONRY PLUG *PLASTIC			

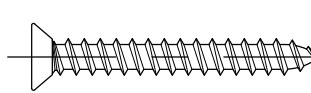FASTENER#:	3	IMAGE: 
PART#:		
FASTENAL #1173036		
.		
.		
.		
DESCRIPTION:		#10-12 x 1-1/2" PFH TYPE-A SMS *18-8SS



PROJECT KIRKLAND & ELLIS ARCHITECT HO&K GENERAL CONTRACTOR STRUCTURE TONE, INC	DESCRIPTION					
	BY					
	DATE					
	REV					
	PROJ NO	8901				
	DATE	5/4/26				
	DRAWN	SM				
	CHECKED	SB/MO				
	FILE NAME	8109 c 1				
	SCALE	NO SCALE				
	SHEET NUMBER	C102				



SALEM GLASS COMPANY
3 Technology Way, Salem, MA 01970
Phone# (978)744-5177 Fax# (978)745-4036

DESCRIPTION

BY

DATE

REV


PROJECT
KIRKLAND & ELLIS

ARCHITECT
HO&K

GENERAL CONTRACTOR
STRUCTURE TONE, INC

PROJ NO	8901
DATE	5/4/26
DRAWN	SM
CHECKED	SB/MO
FILE NAME	8109 p 1
SCALE	1/8"=1'-0"

SHEET NUMBER	P101
--------------	------

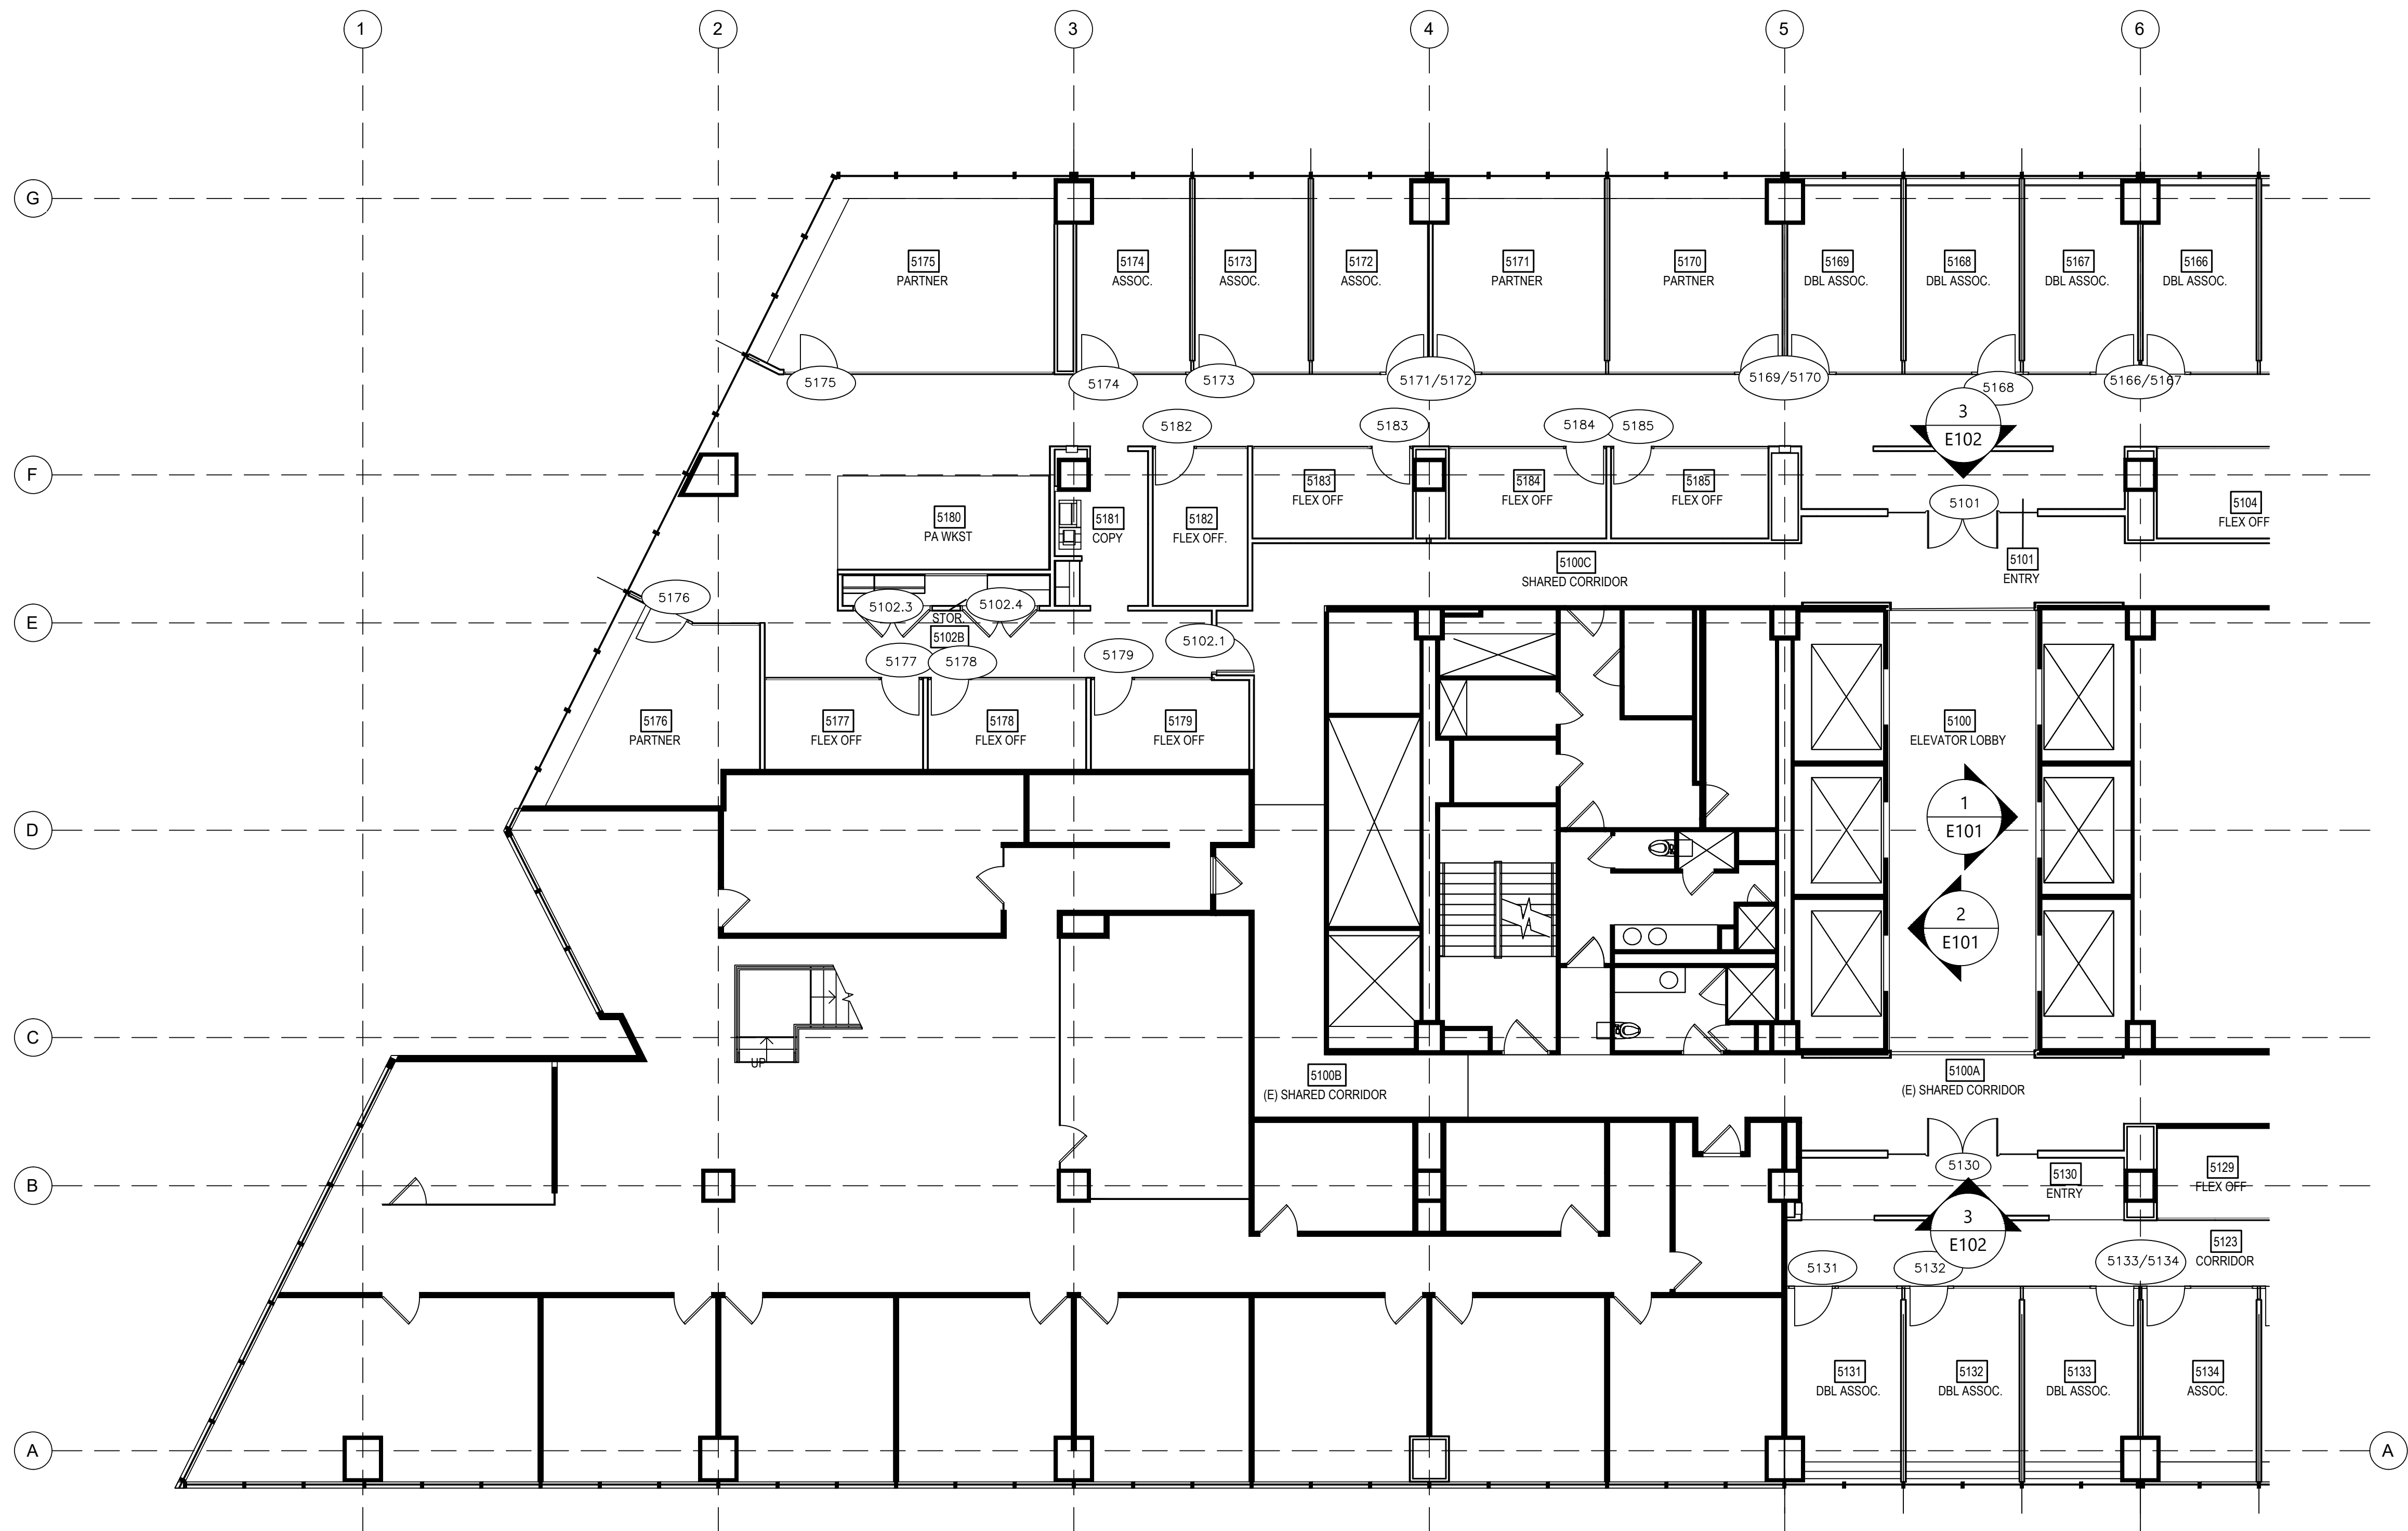


A LEVEL 51— FINISH PLAN— PART A
ARCH REF: 1/A401A




ALL DIMENSIONS TO BE
VERIFIED IN FIELD BY SGC
PRIOR TO FABRICATION

GL1 7/16" ACID ETCH LAMINATED MIRROR
GL2 1/2" CLEAR TEMPERED GLASS

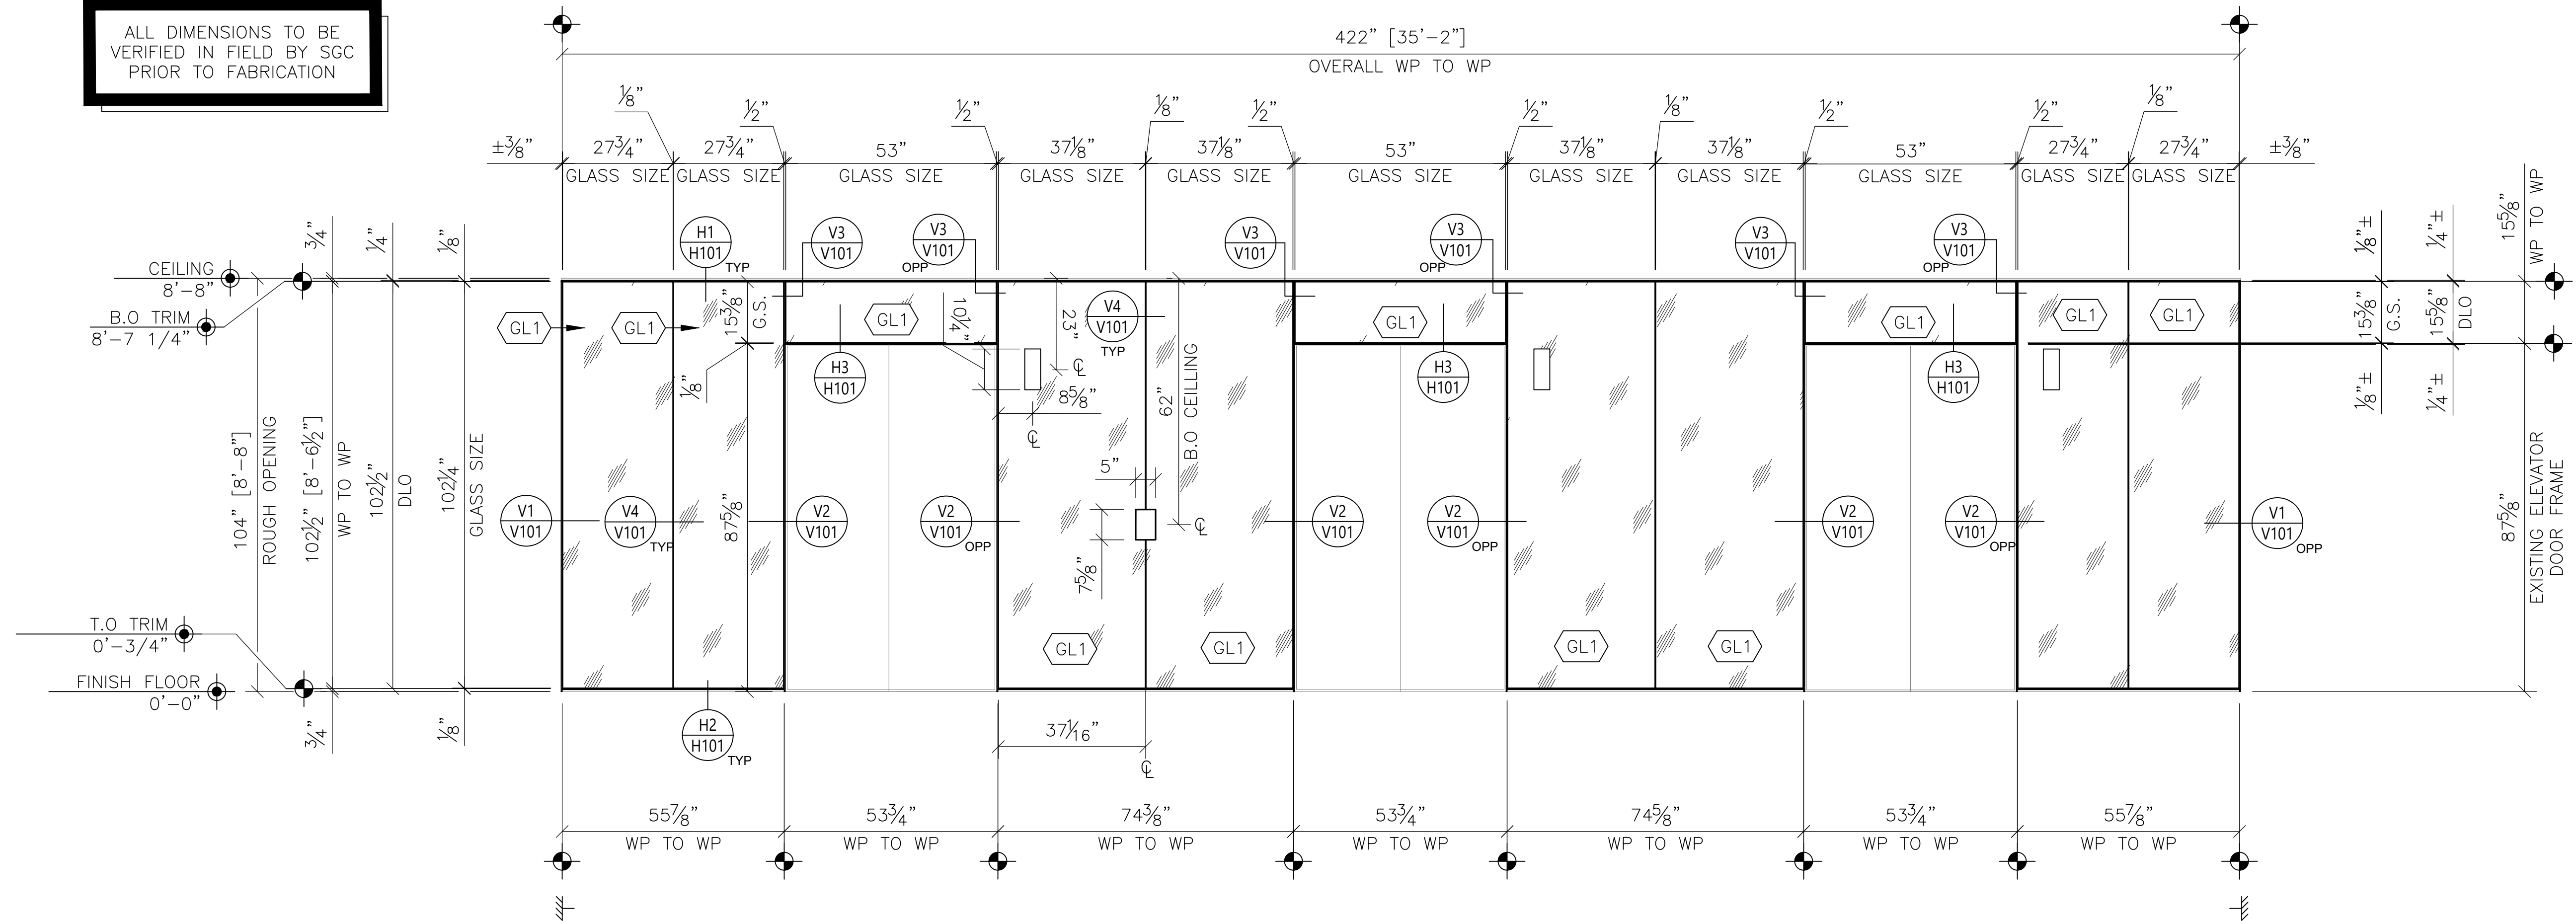

1 ELEVATION—EAST
QUANTITY: 1
ARCH. REF: 4/A803
© ELEVATOR LOBBY 5100

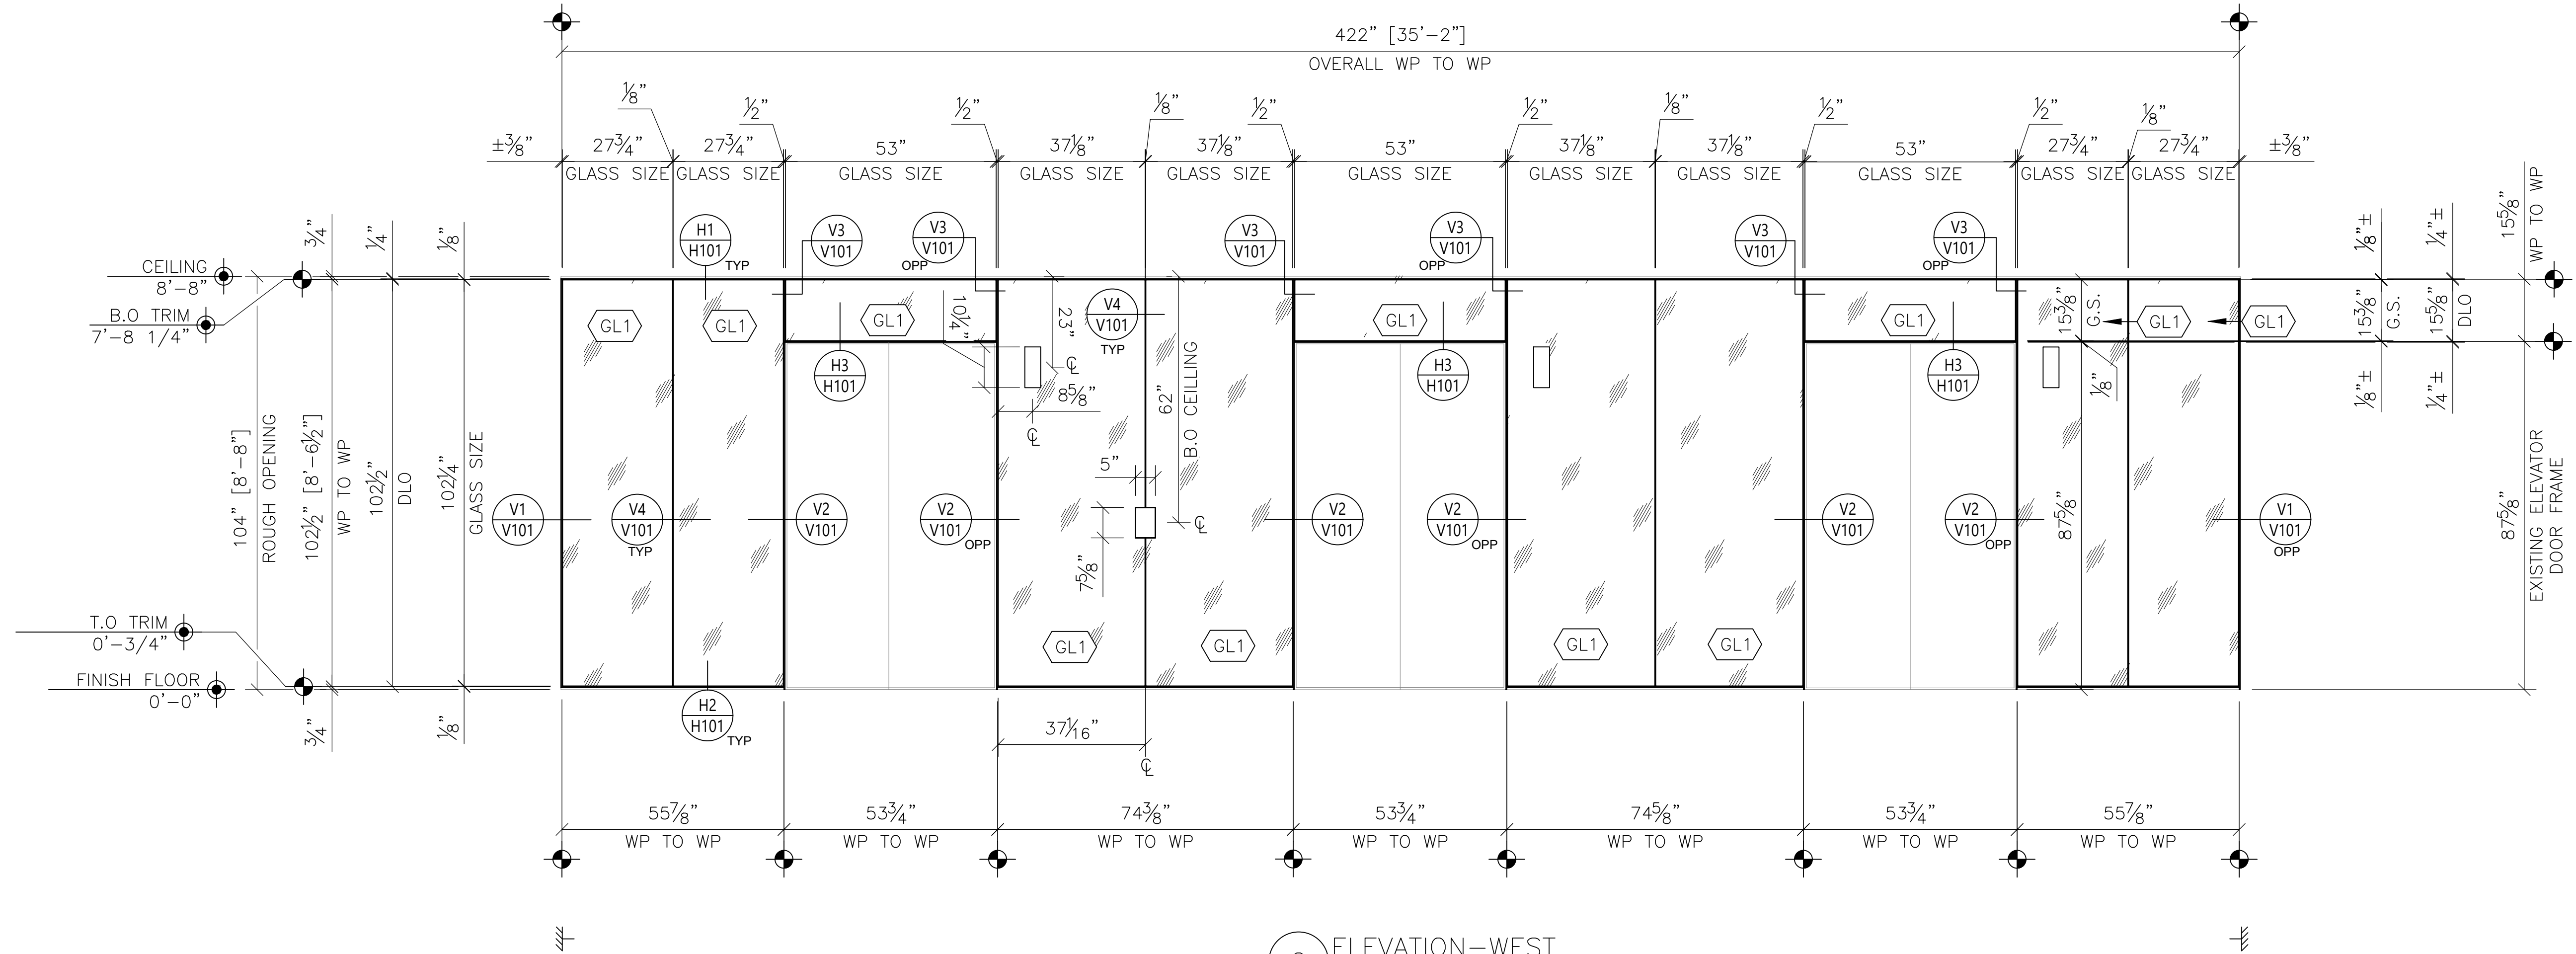

2 ELEVATION—WEST
QUANTITY: 1
ARCH. REF: 2/A803
© ELEVATOR LOBBY 5100


REV	DATE	BY	DESCRIPTION
PROJECT			KIRKLAND & ELLIS
ARCHITECT			HO&K
GENERAL CONTRACTOR			STRUCTURE TONE, INC
PROJ NO		8901	
DATE		5/4/26	
DRAWN		SM	
CHECKED		SB/MO	
FILE NAME		8109 e 1	
SCALE		1/2"=1'-0"	
SHEET NUMBER		E101	

ALL DIMENSIONS TO BE
VERIFIED IN FIELD BY SGC
PRIOR TO FABRICATION

GL1	7/16" ACID ETCH LAMINATED MIRROR
GL2	1/2" CLEAR TEMPERED GLASS




SALEM GLASS COMPANY
3 Technology Way, Salem, MA 01970
Phone# (978)744-5177 Fax# (978)745-4036

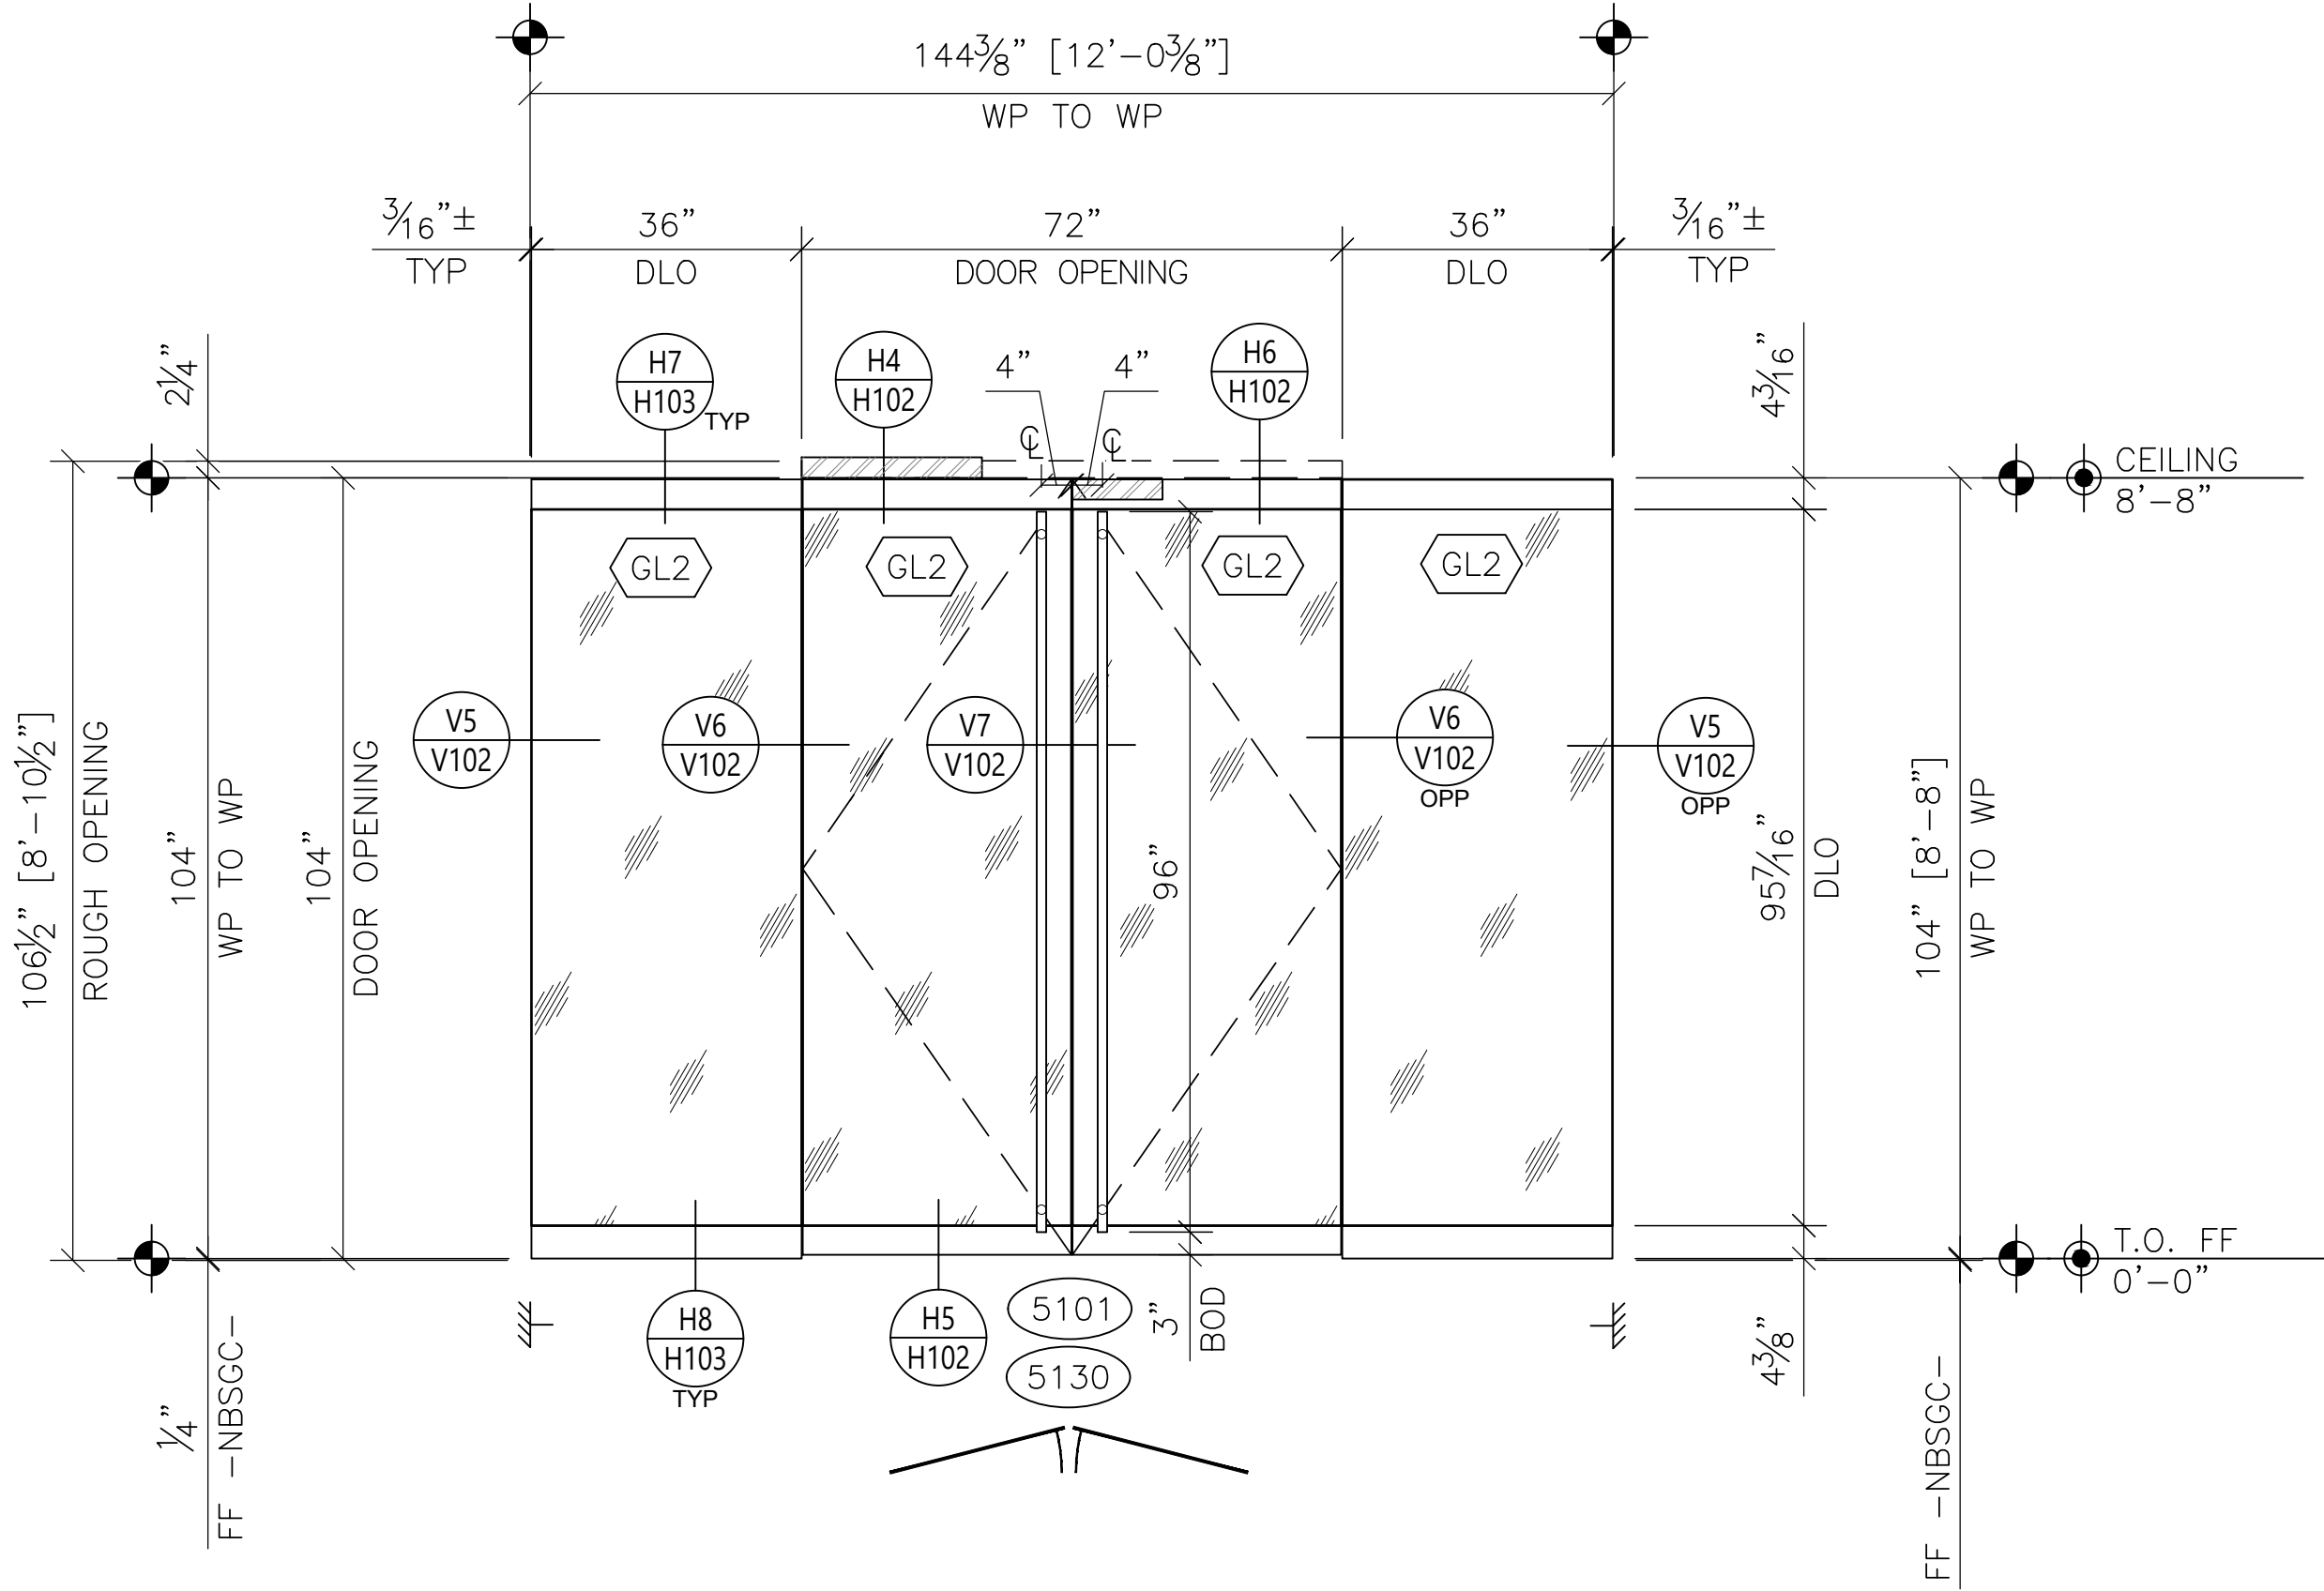


3 ELEVATION-ELEVATOR LOBBY-NORTH & SOUTH
QUANTITY: 2
ARCH REF: 1&3/A803


[illegible]

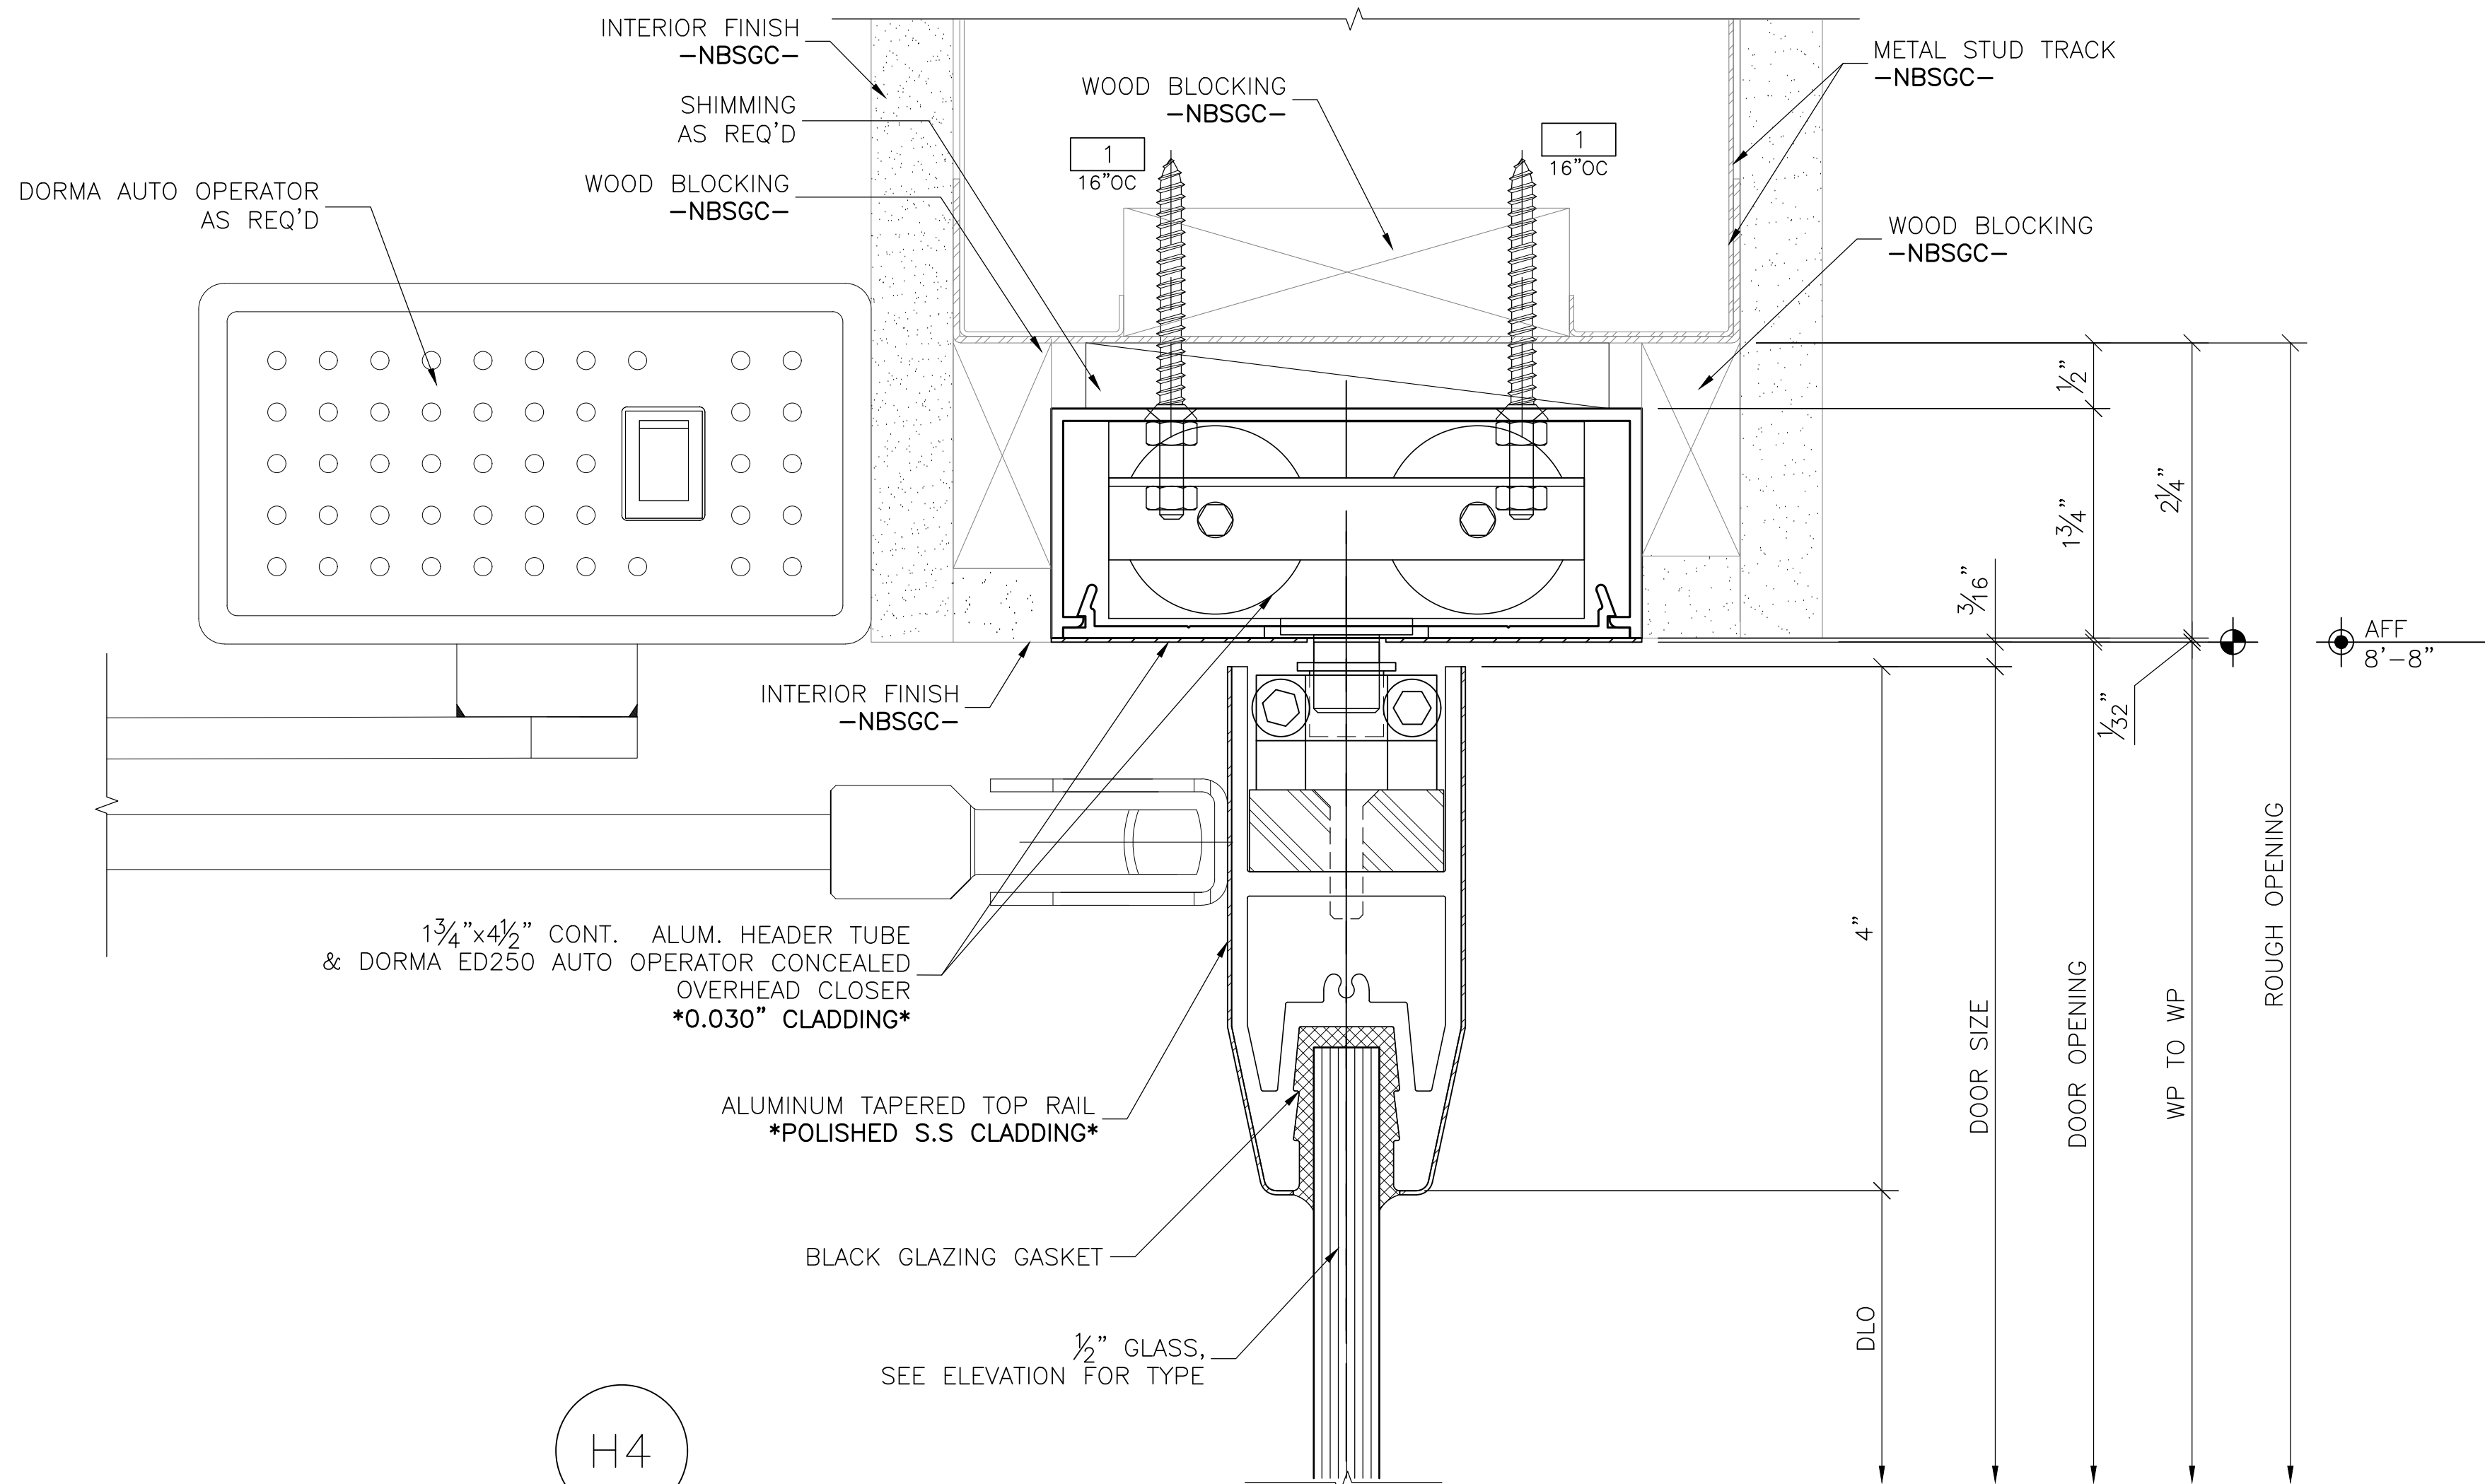

H4
DOOR HEAD DETAIL
W/ CLAD TOP RAIL & HEADER TUBE COC & DORMA AUTO OP
ARCH REF: NONE

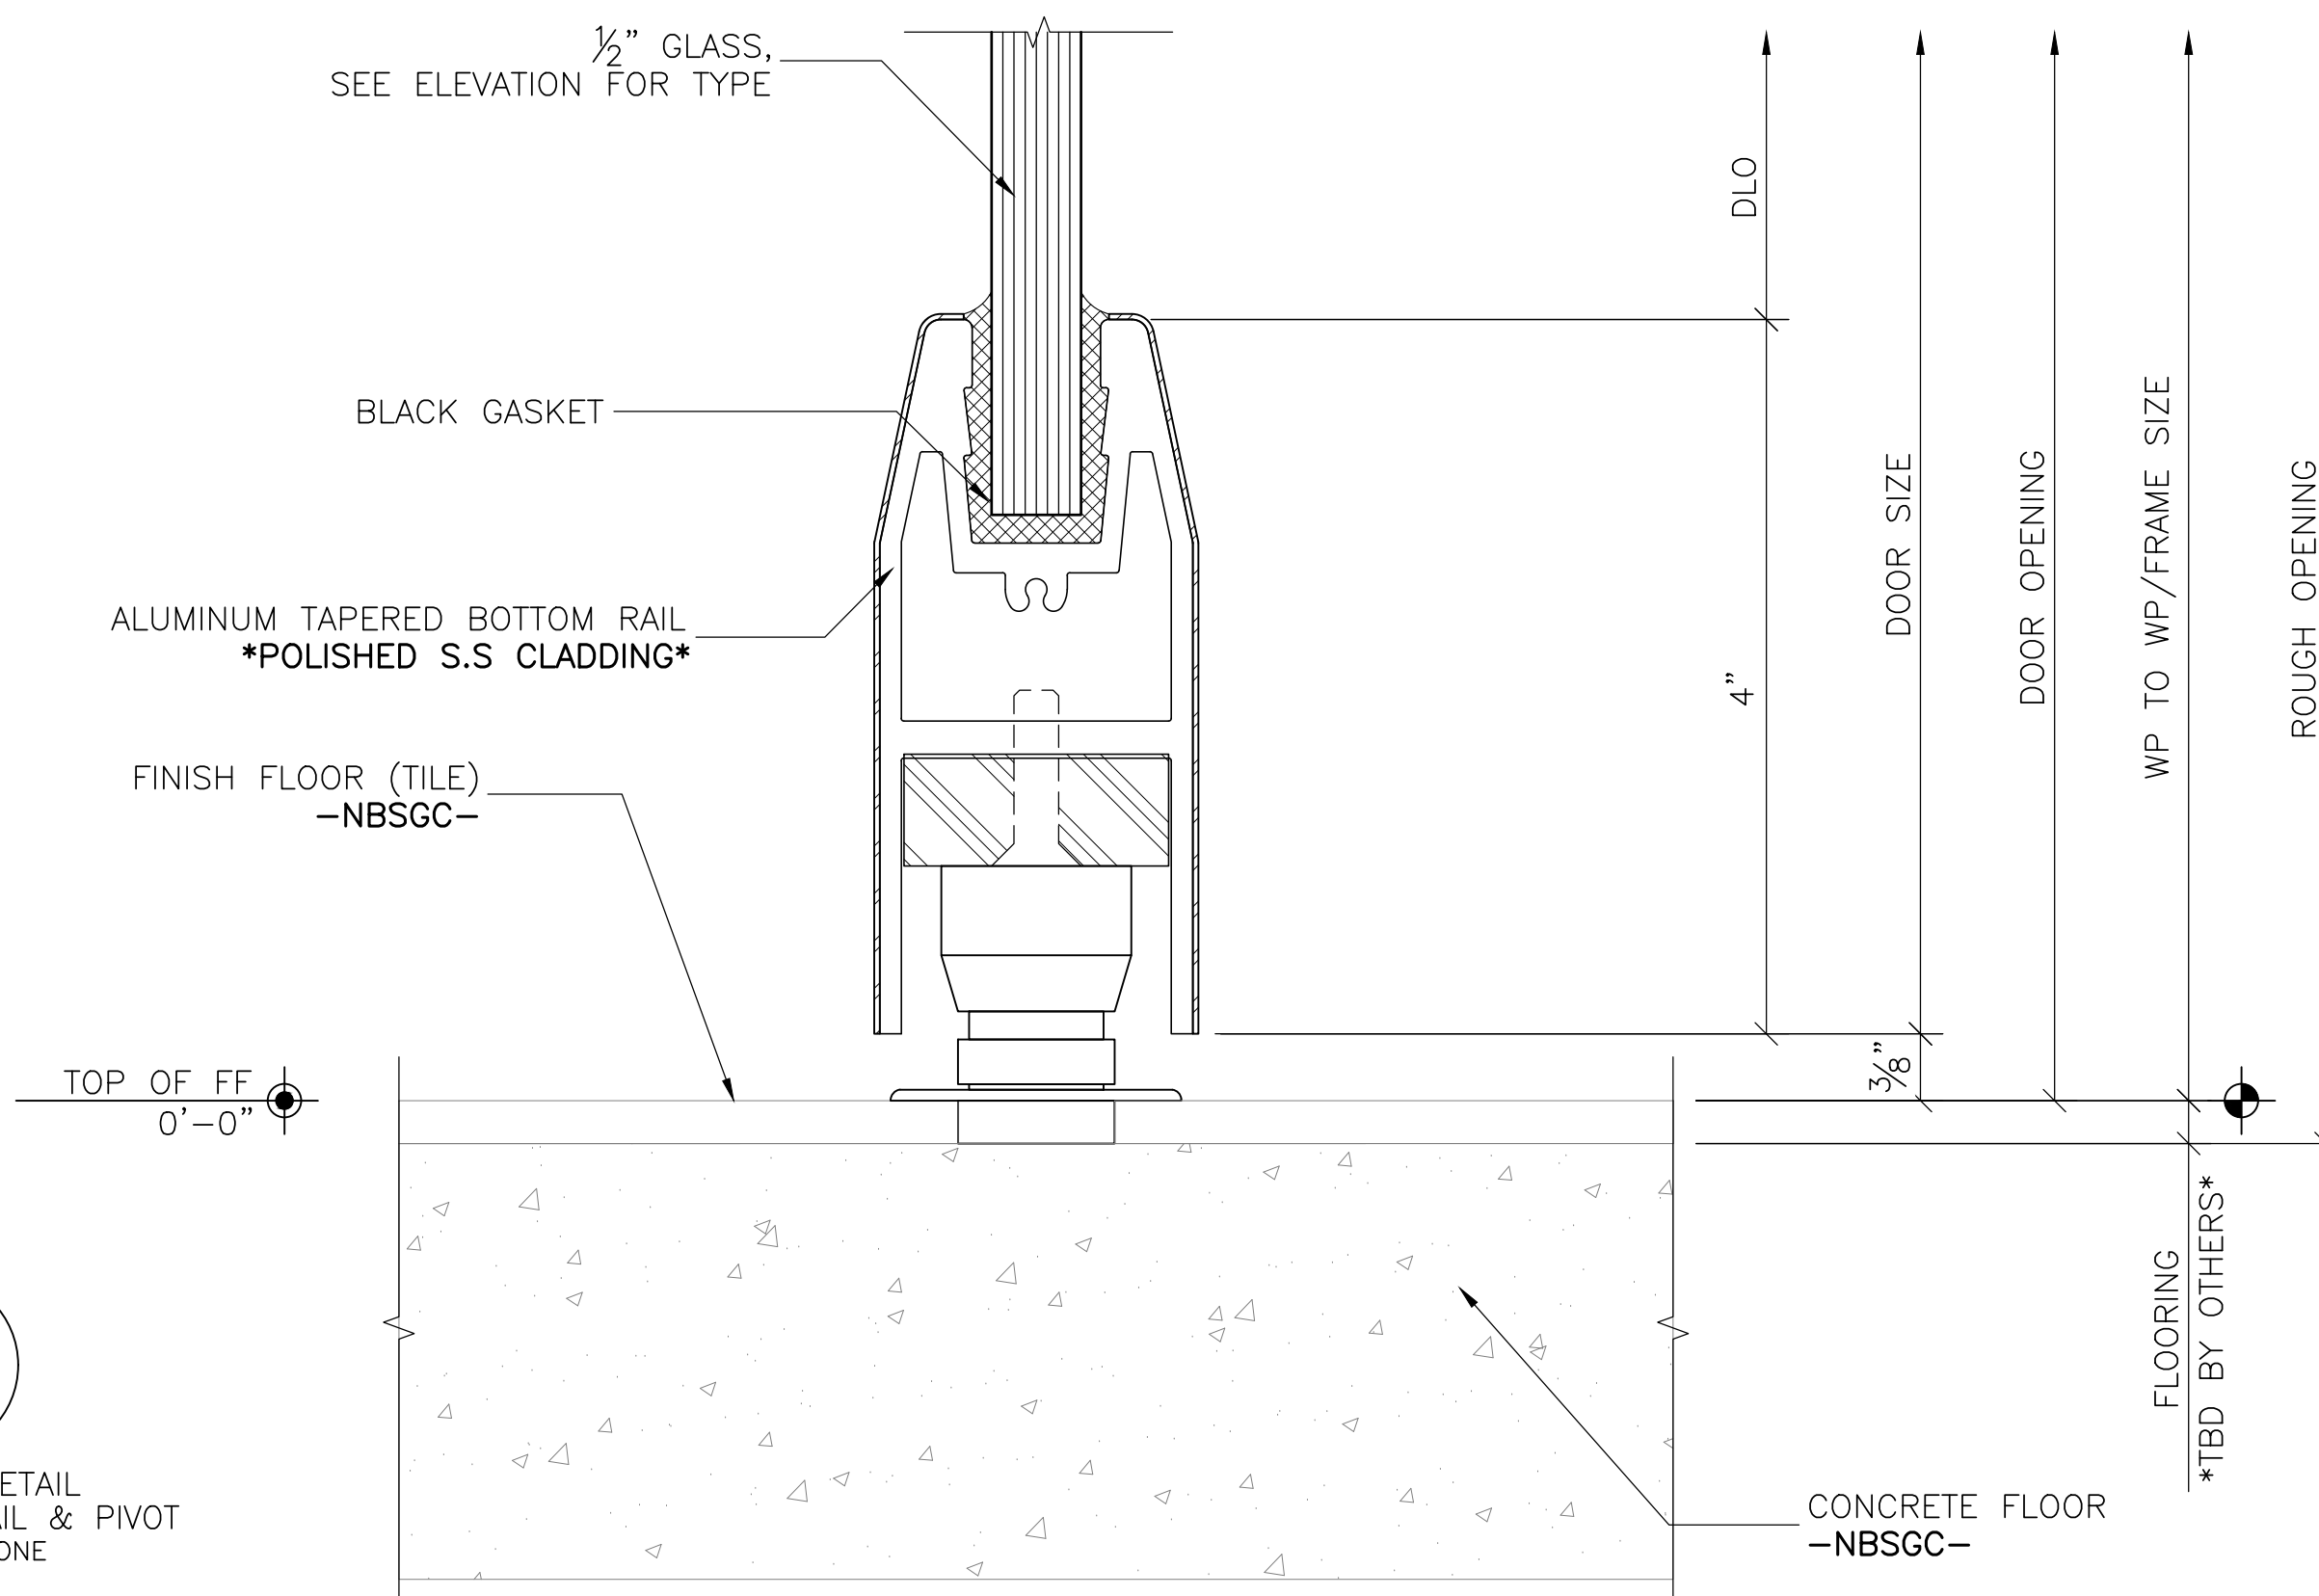

H5
DOOR SILL DETAIL
W/ CLAD BOTTOM RAIL & PIVOT
ARCH REF: NONE

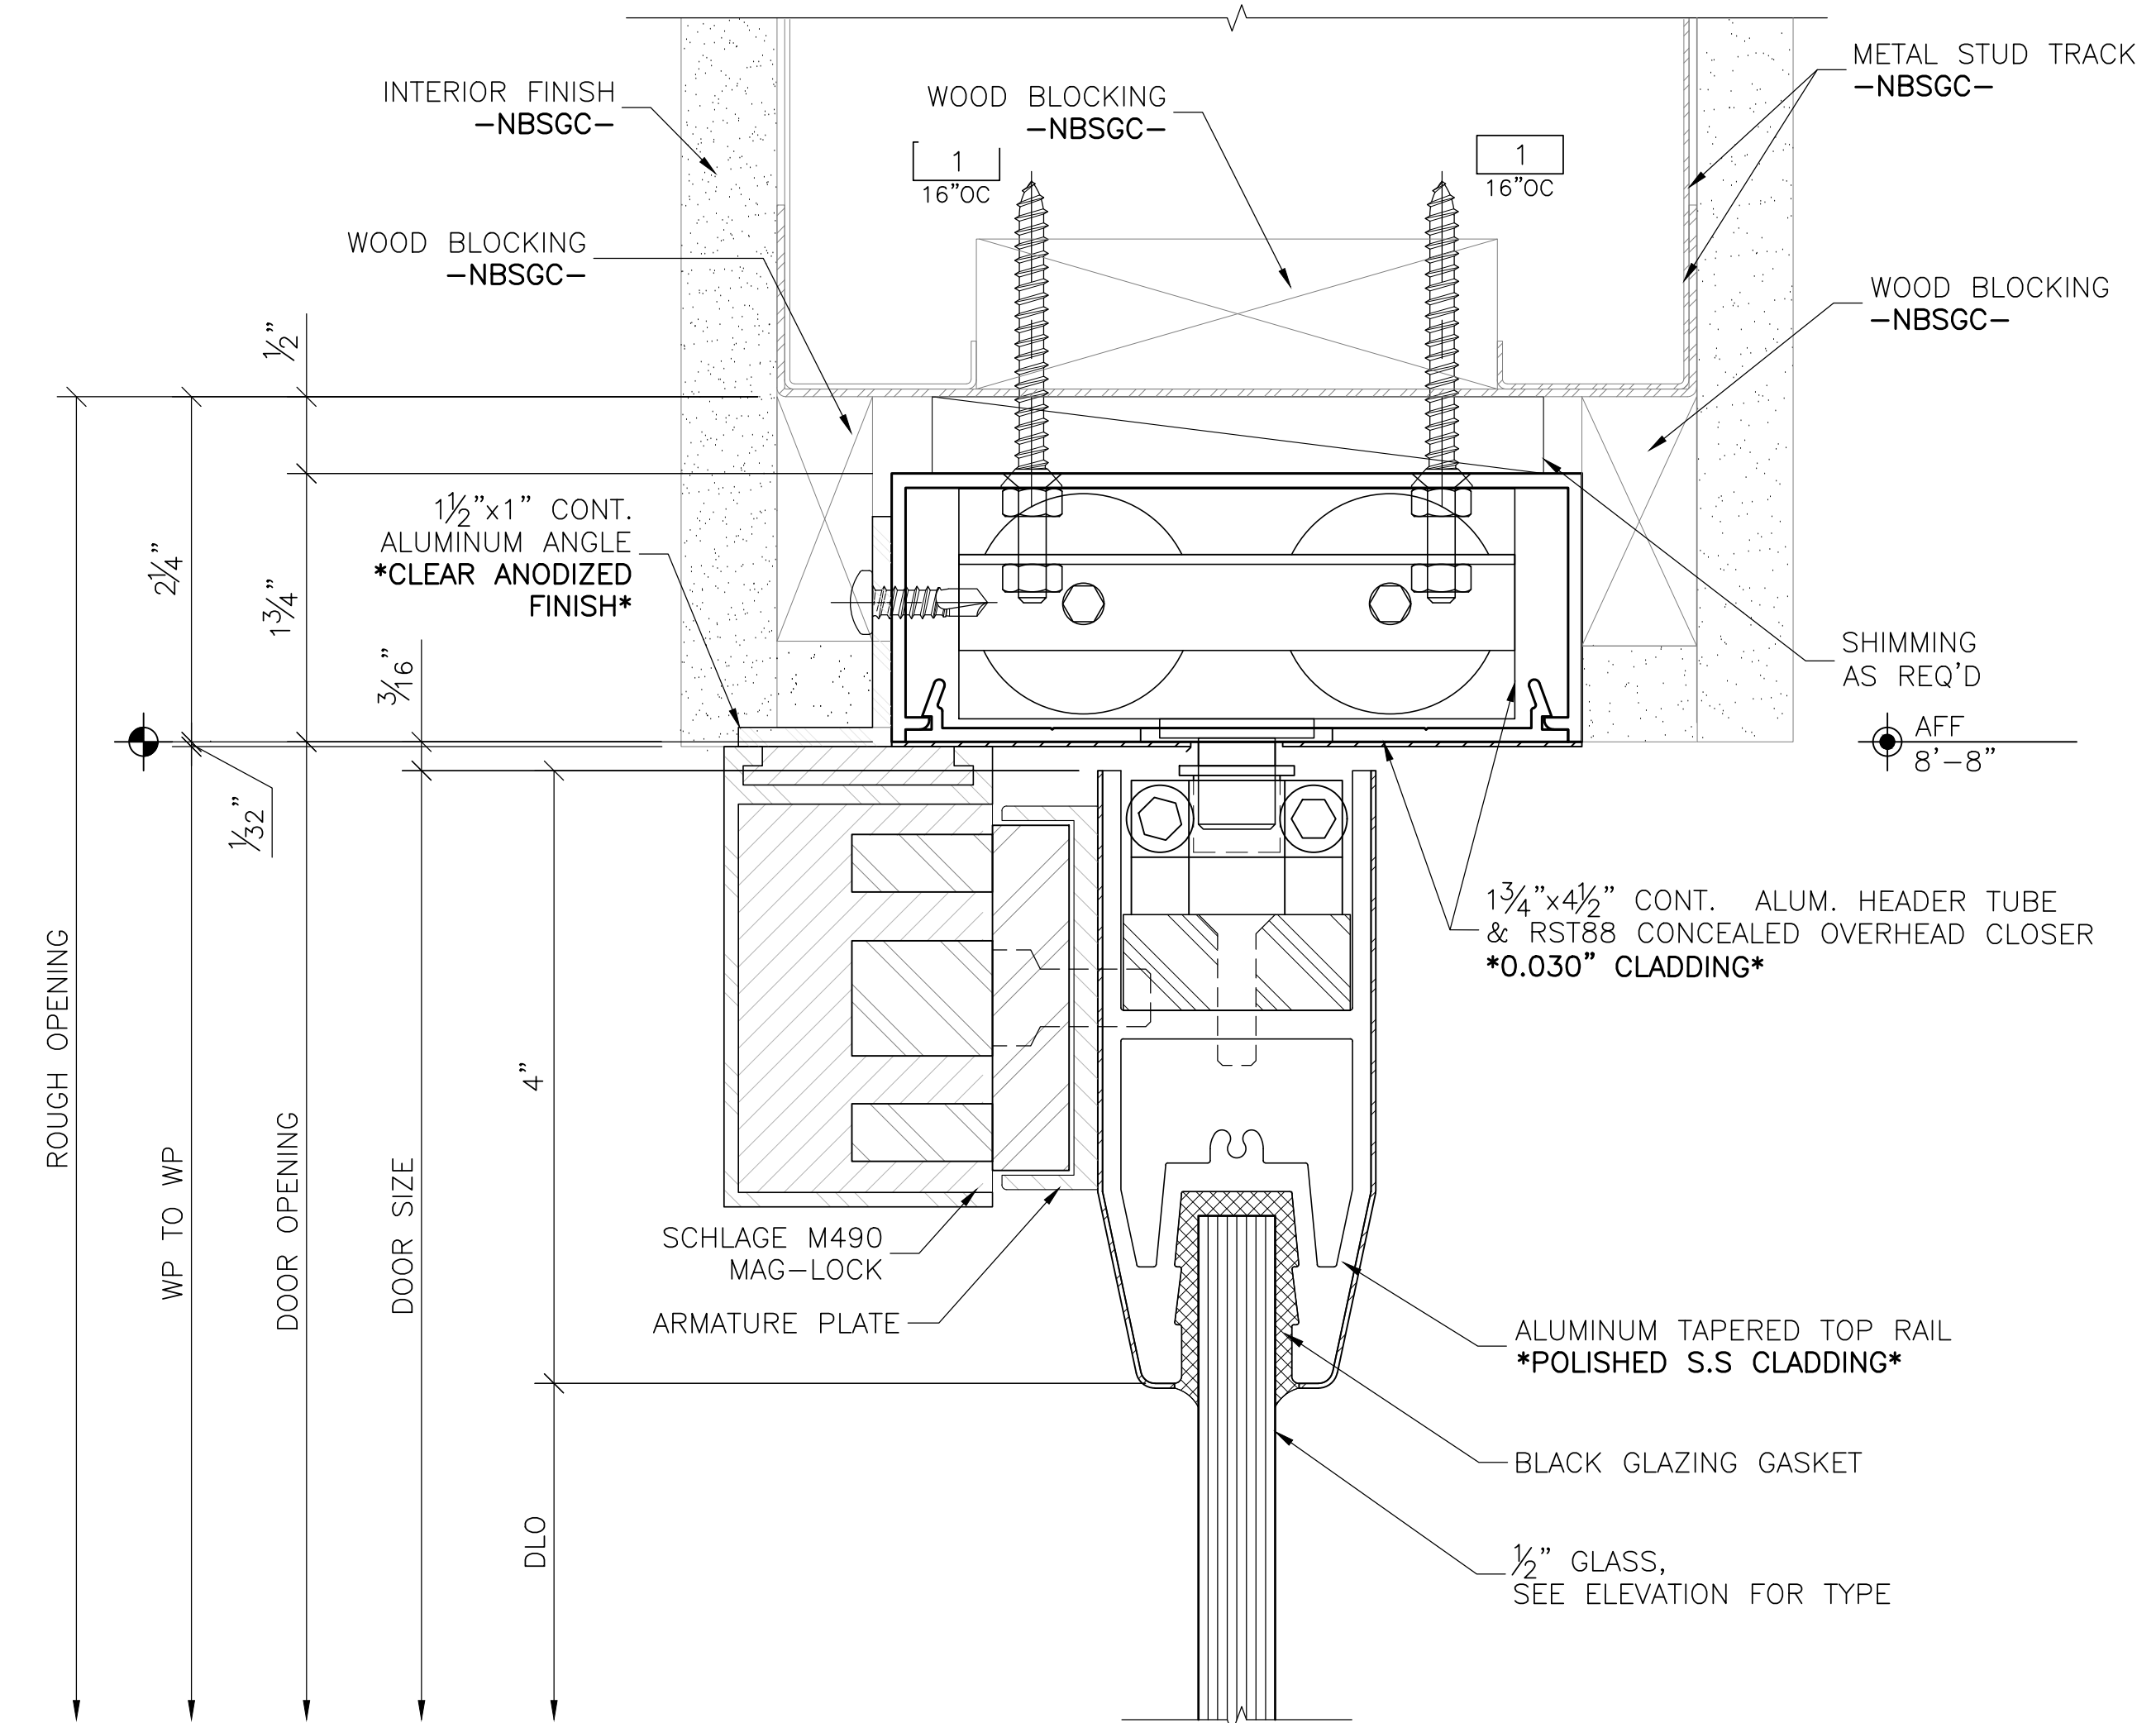

H6
DOOR HEAD DETAIL
W/ CLAD TOP RAIL & HEADER TUBE COC & MAG-LOCK
ARCH REF: 7/A621

DESCRIPTION

BY

DATE

REV

PROJECT
KIRKLAND & ELLIS

ARCHITECT
HO&K

GENERAL CONTRACTOR
STRUCTURE TONE, INC

PROJ NO	8901
DATE	5/4/26
DRAWN	SM
CHECKED	SB/MO
FILE NAME	8109 h 1
SCALE	FULL SCALE


SHEET NUMBER	H102
--------------	------

[illegible]


PROJECT	KIRKLAND & ELLIS
ARCHITECT	HO&K
GENERAL CONTRACTOR	STRUCTURE TONE INC.

PROJ NO	8901
DATE	5/4/26
DRAWN	SM
CHECKED	SB/MO
FILE NAME	8109 h
SCALE	FULL SCA


SHEET NUMBER	H103
-----------------	------

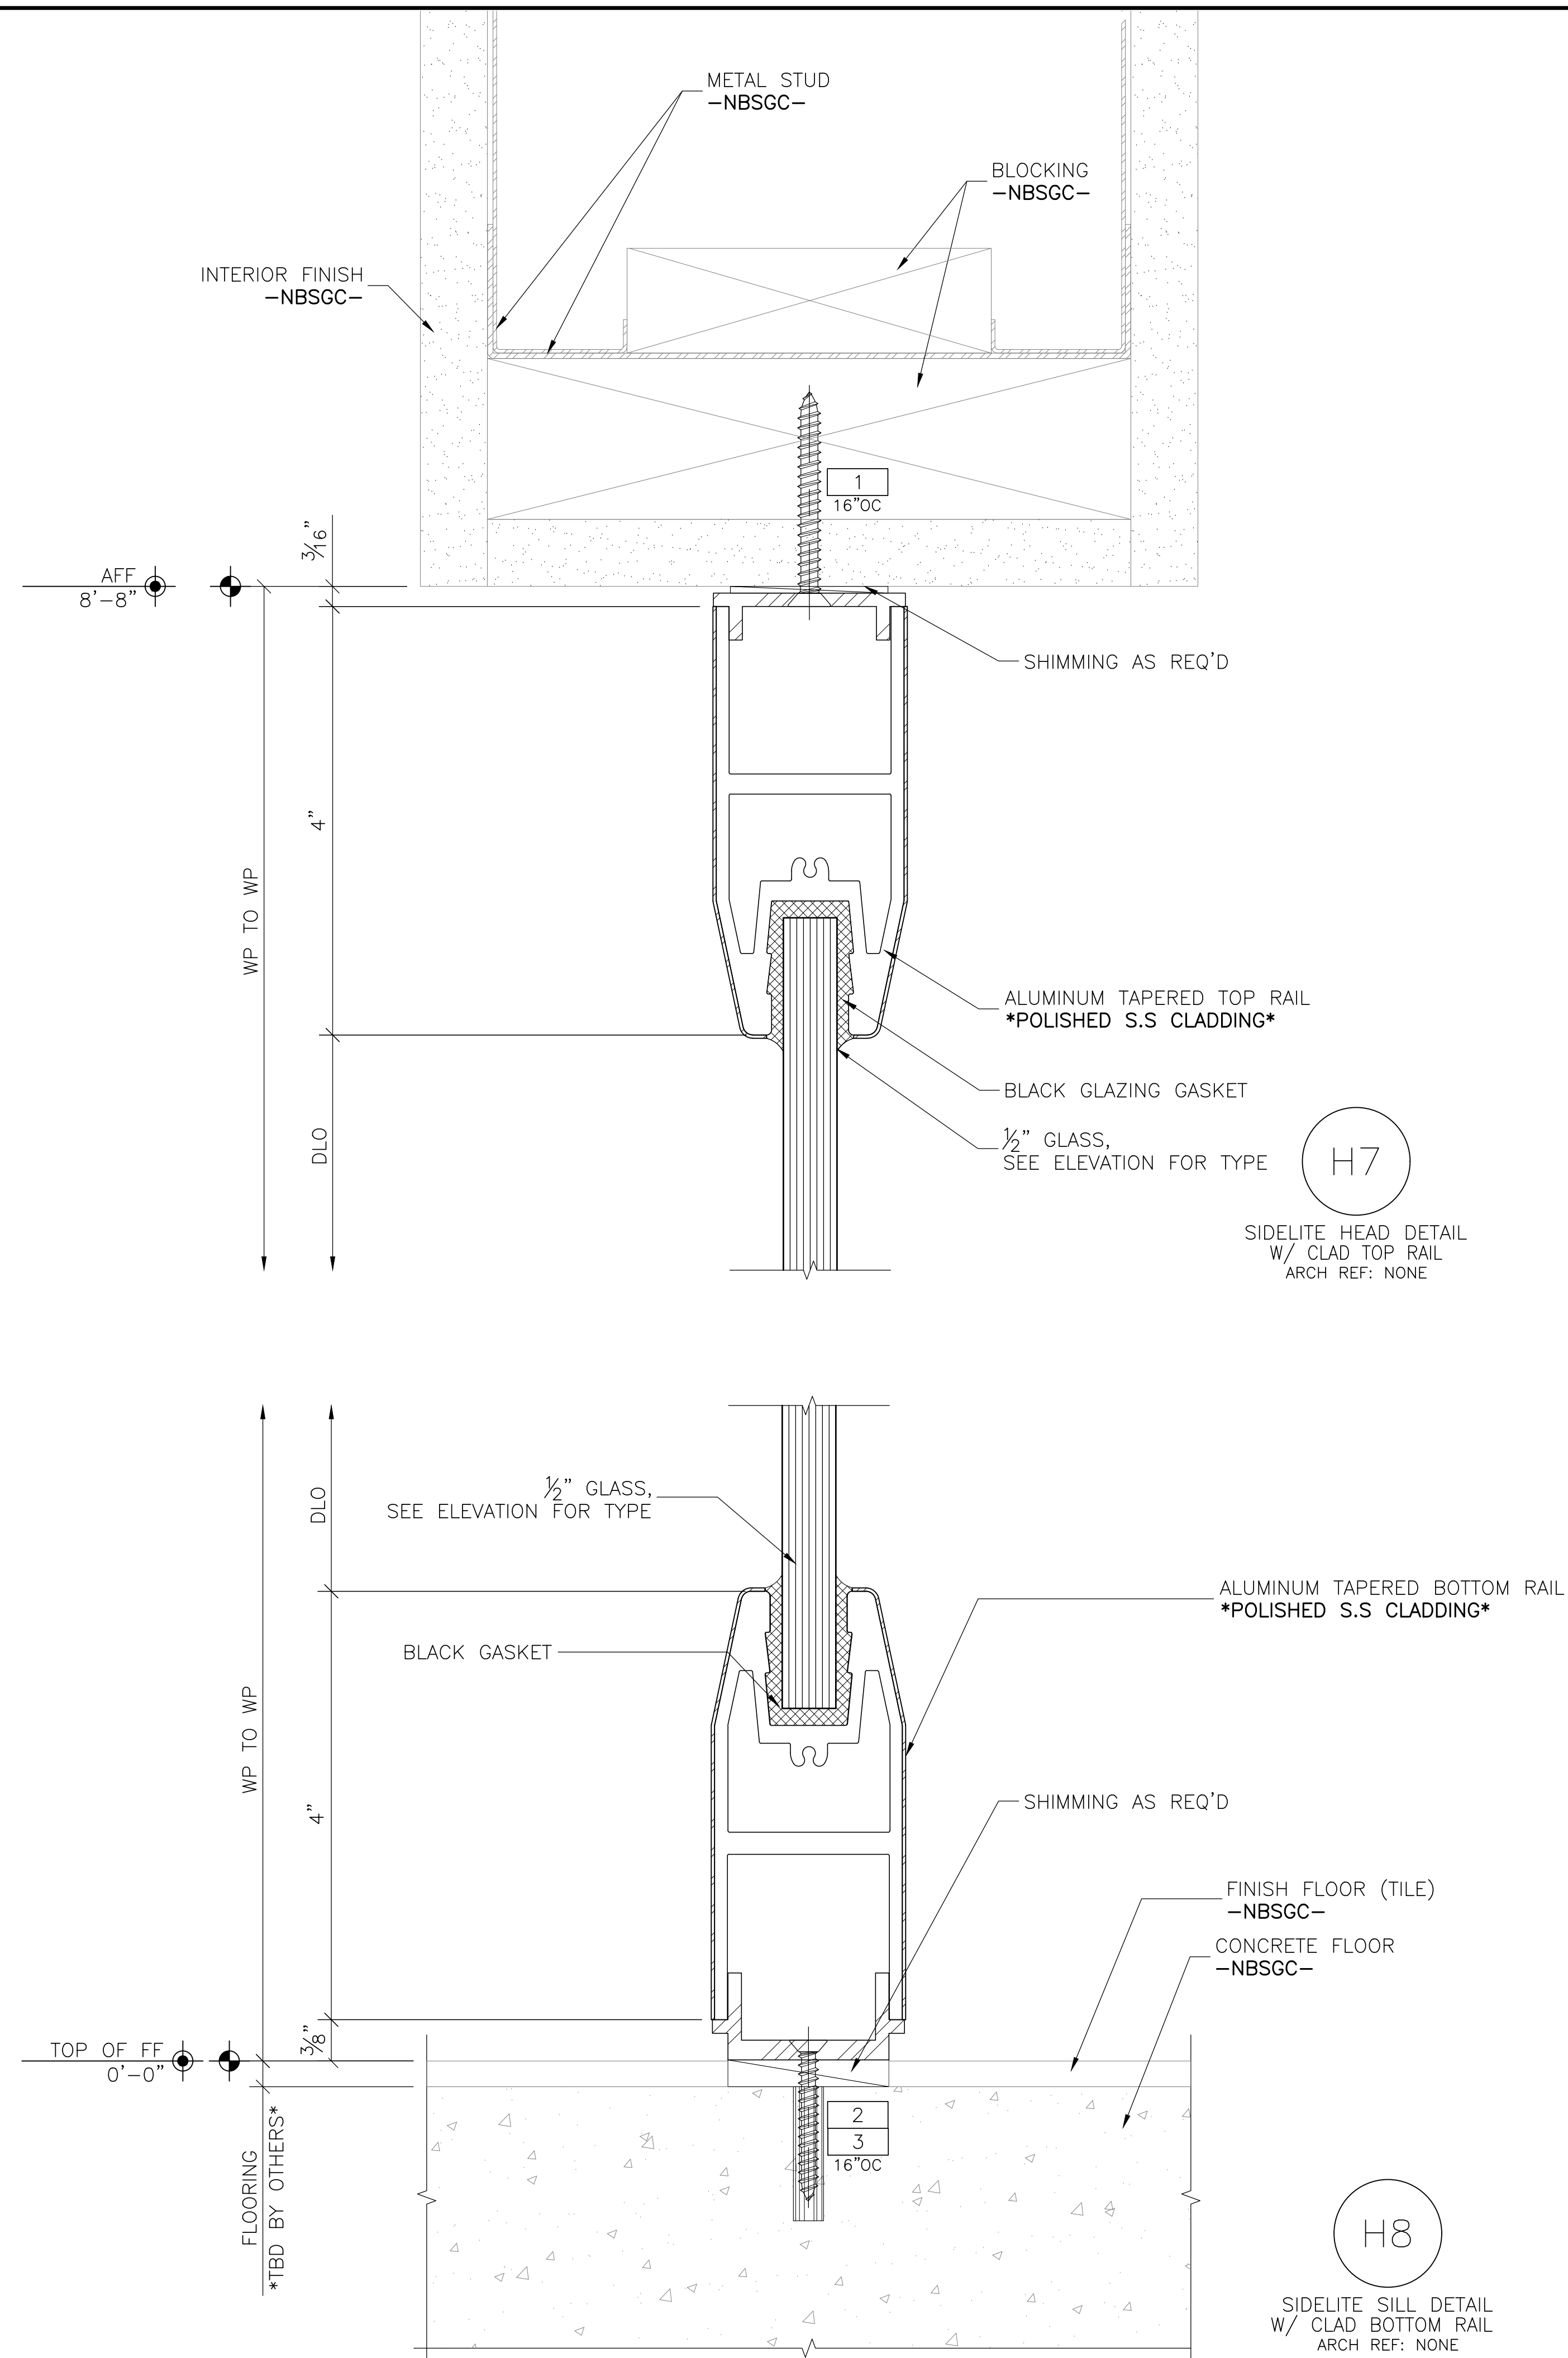


ARCHITECT/GC NOTE:
AT BACKPAINTED GLASS LOCATIONS ADHERED TO WOOD,
THE WOOD SHOULD BE UNPRIMED/PAINTED, FREE OF DUST
AND NOT BE FIRE RATED.

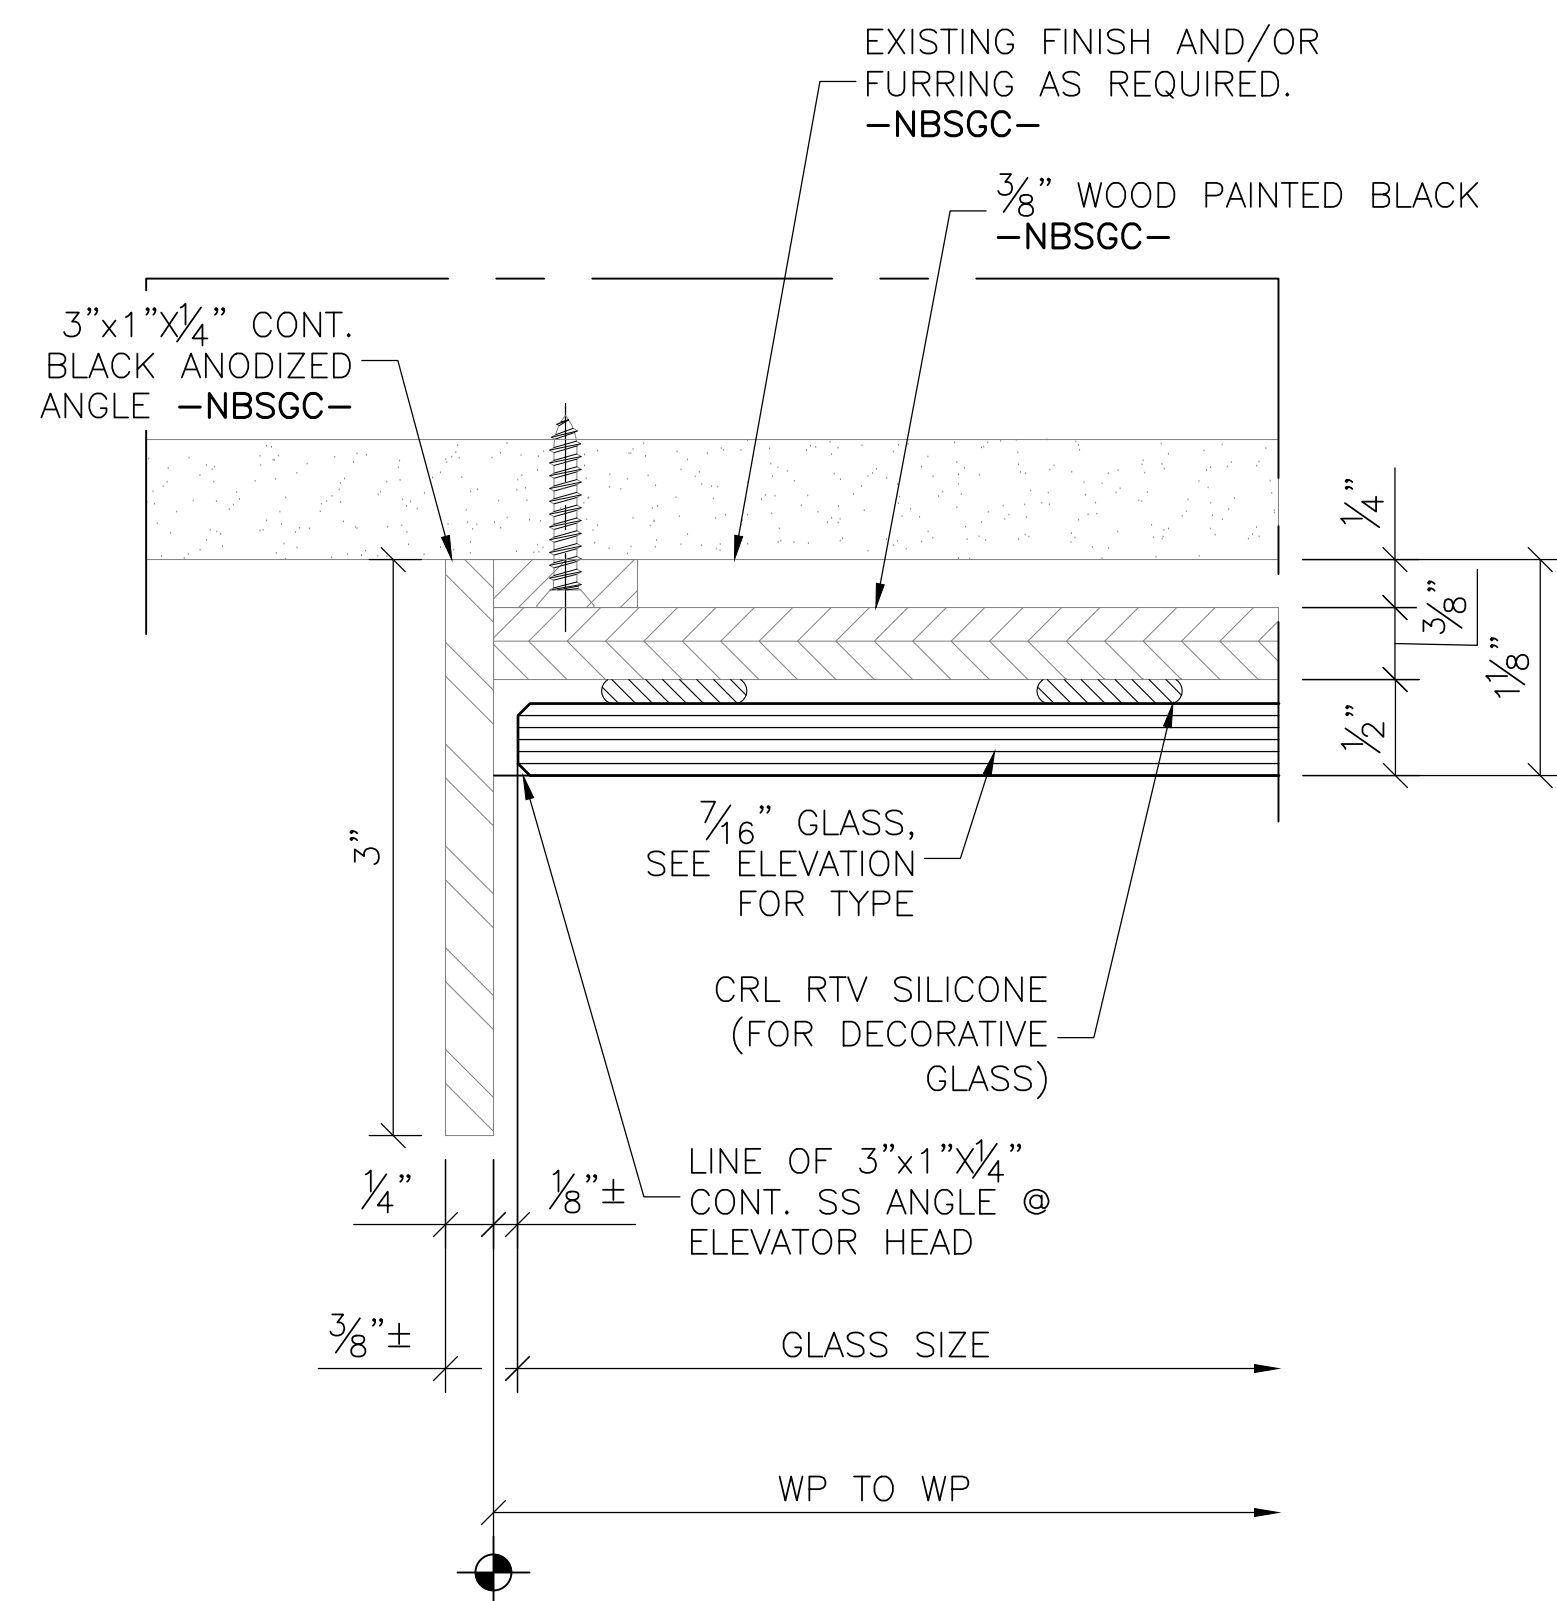


V1
OPEN JAMB
© BACK PAINTED GLASS
ARCH REF: NONE

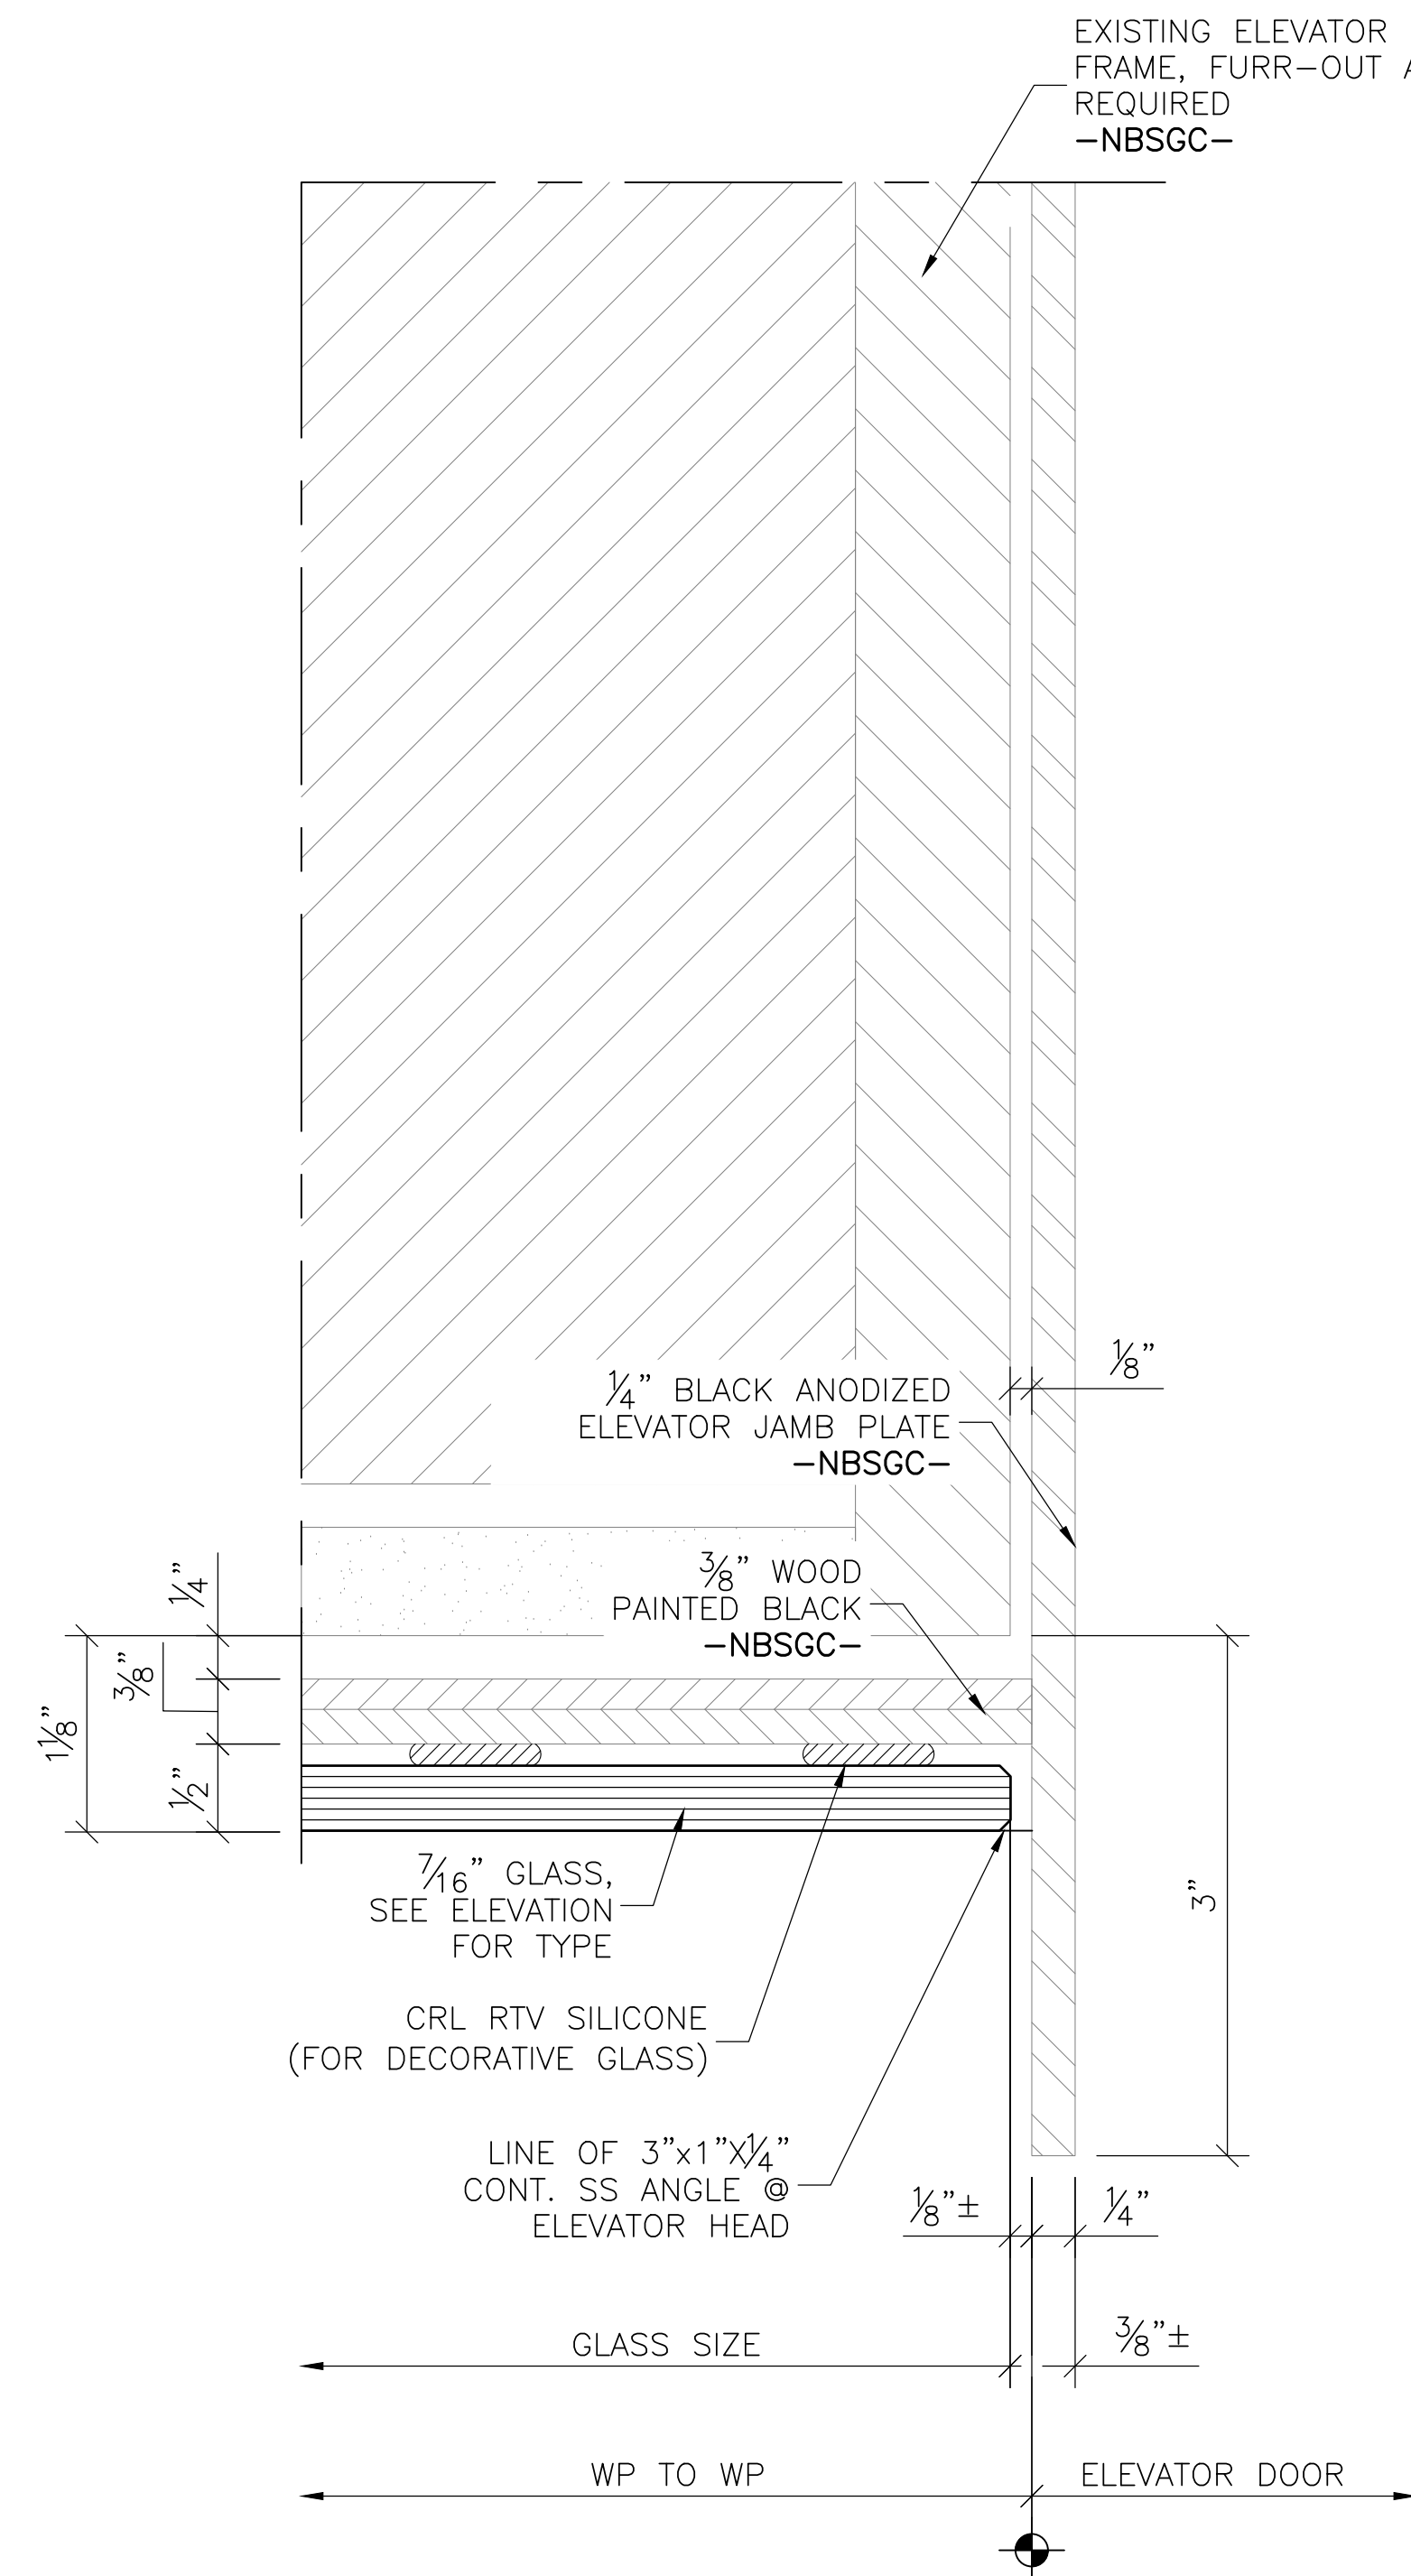

V2
ELEVATOR JAMB
© BACK PAINTED GLASS
ARCH REF: NONE

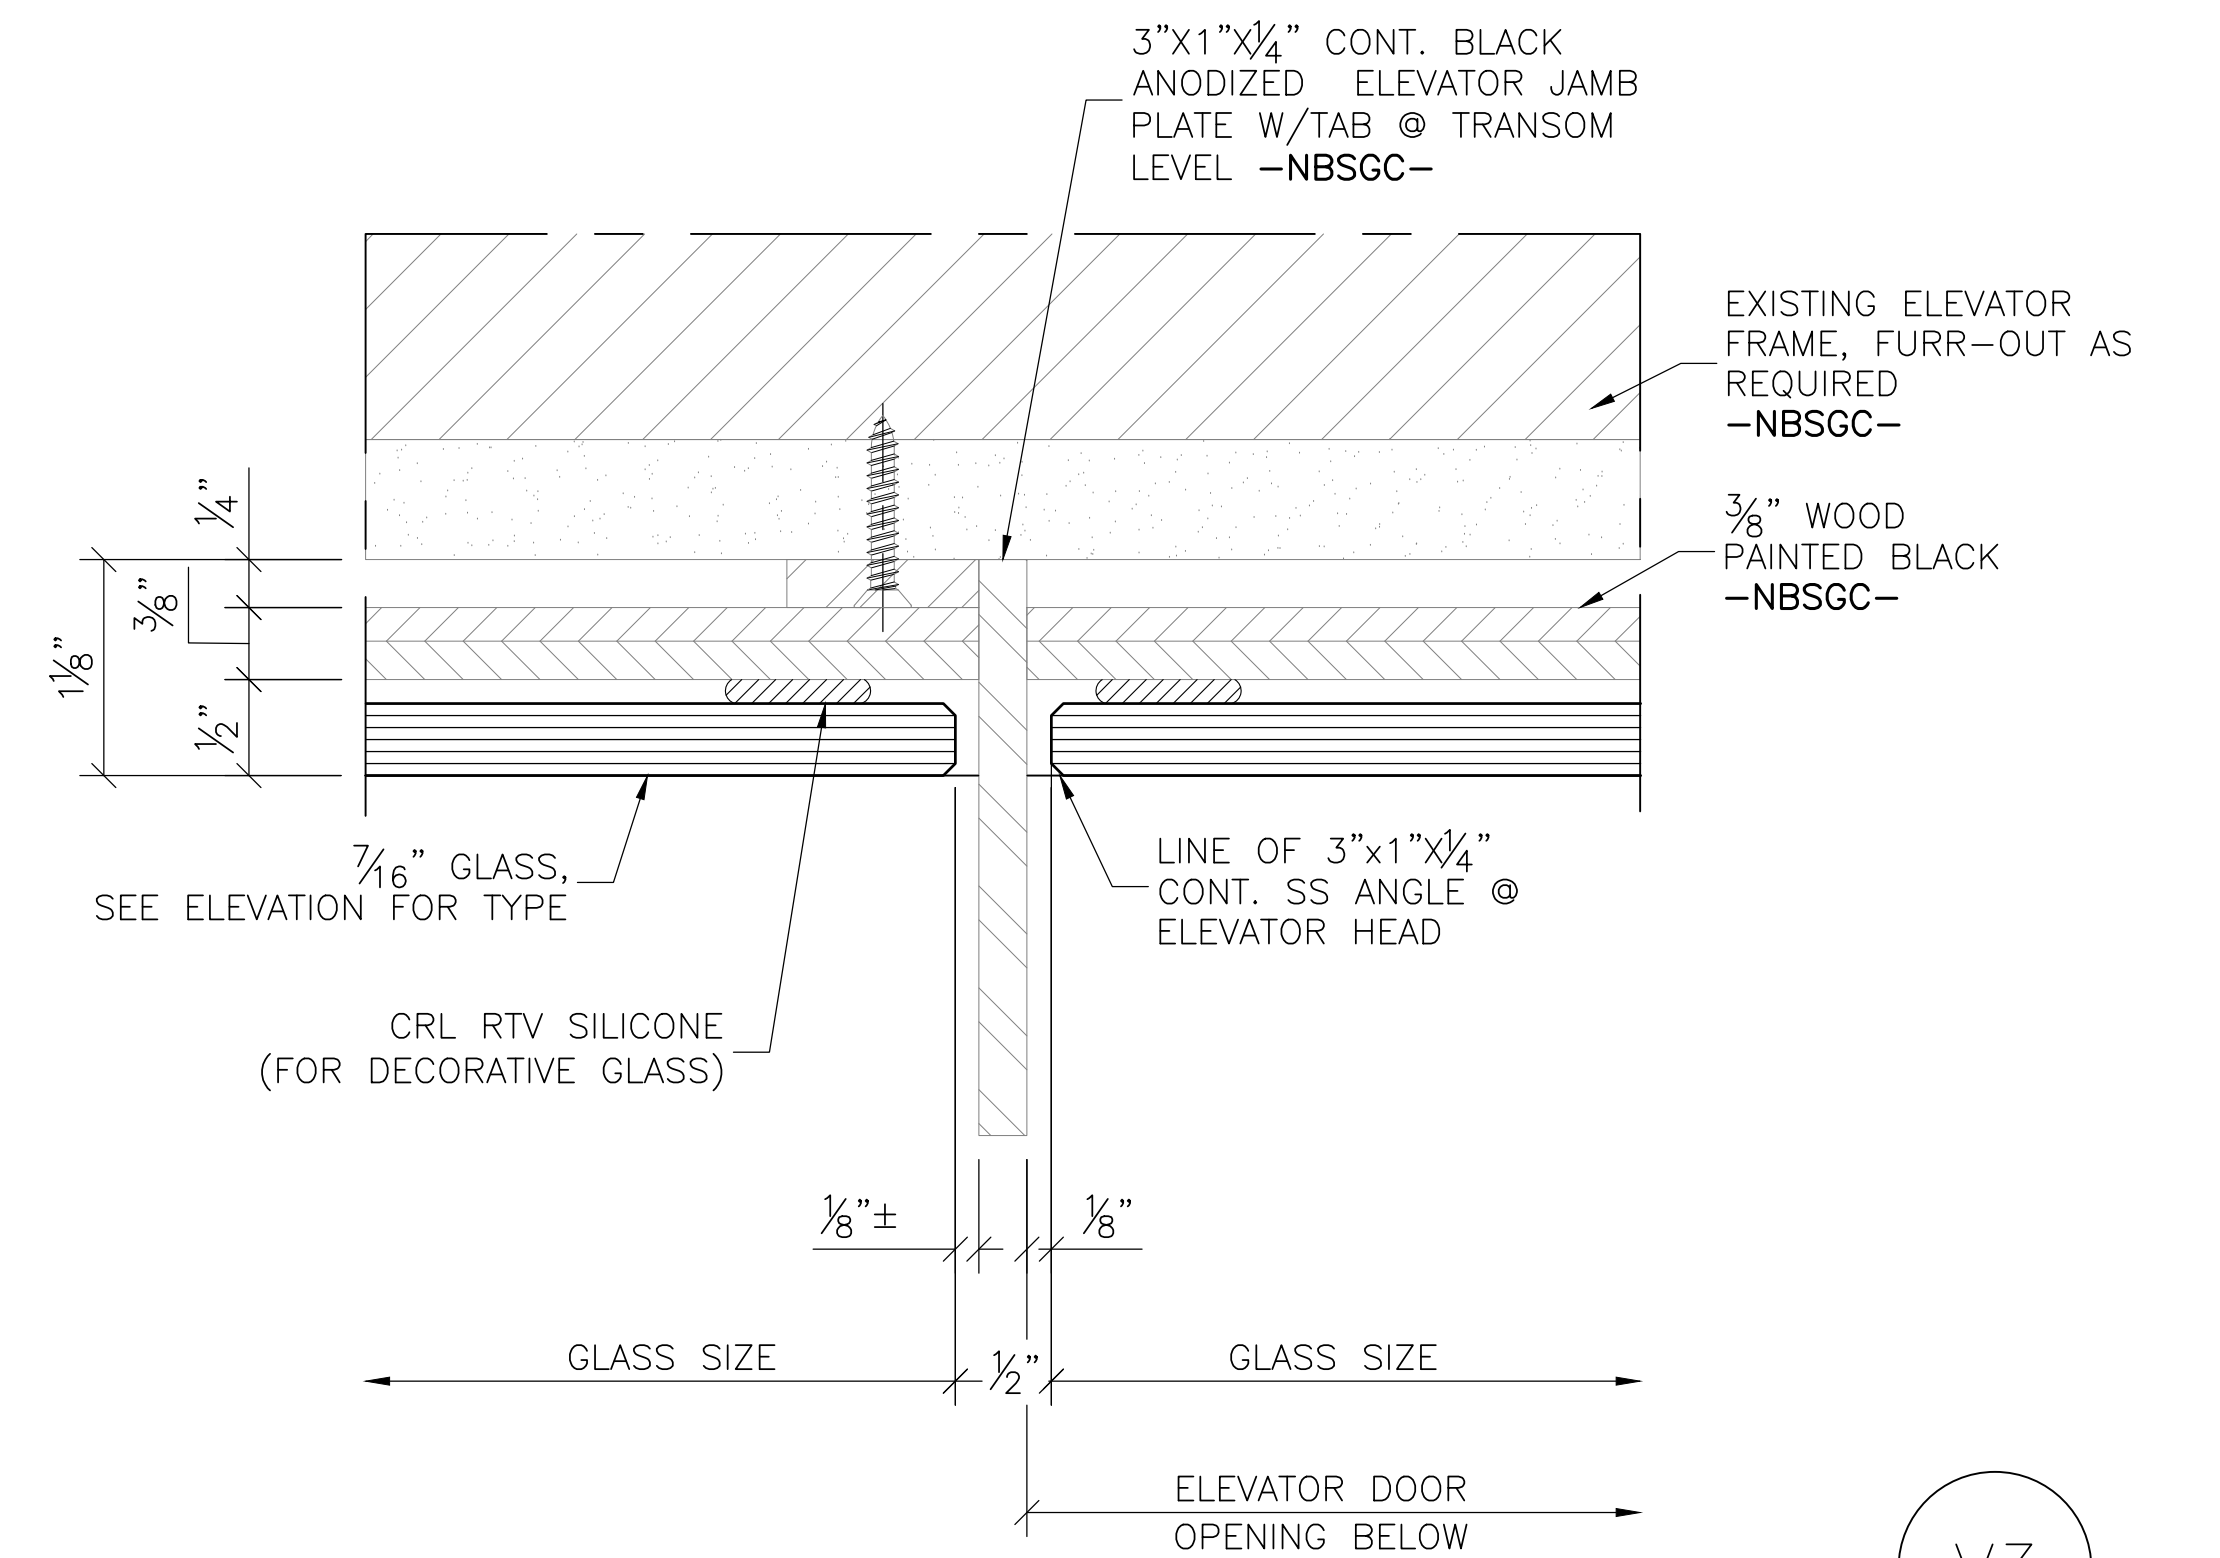

V3
ELEVATOR TRANSOM
© BACK PAINTED GLASS
ARCH REF: NONE

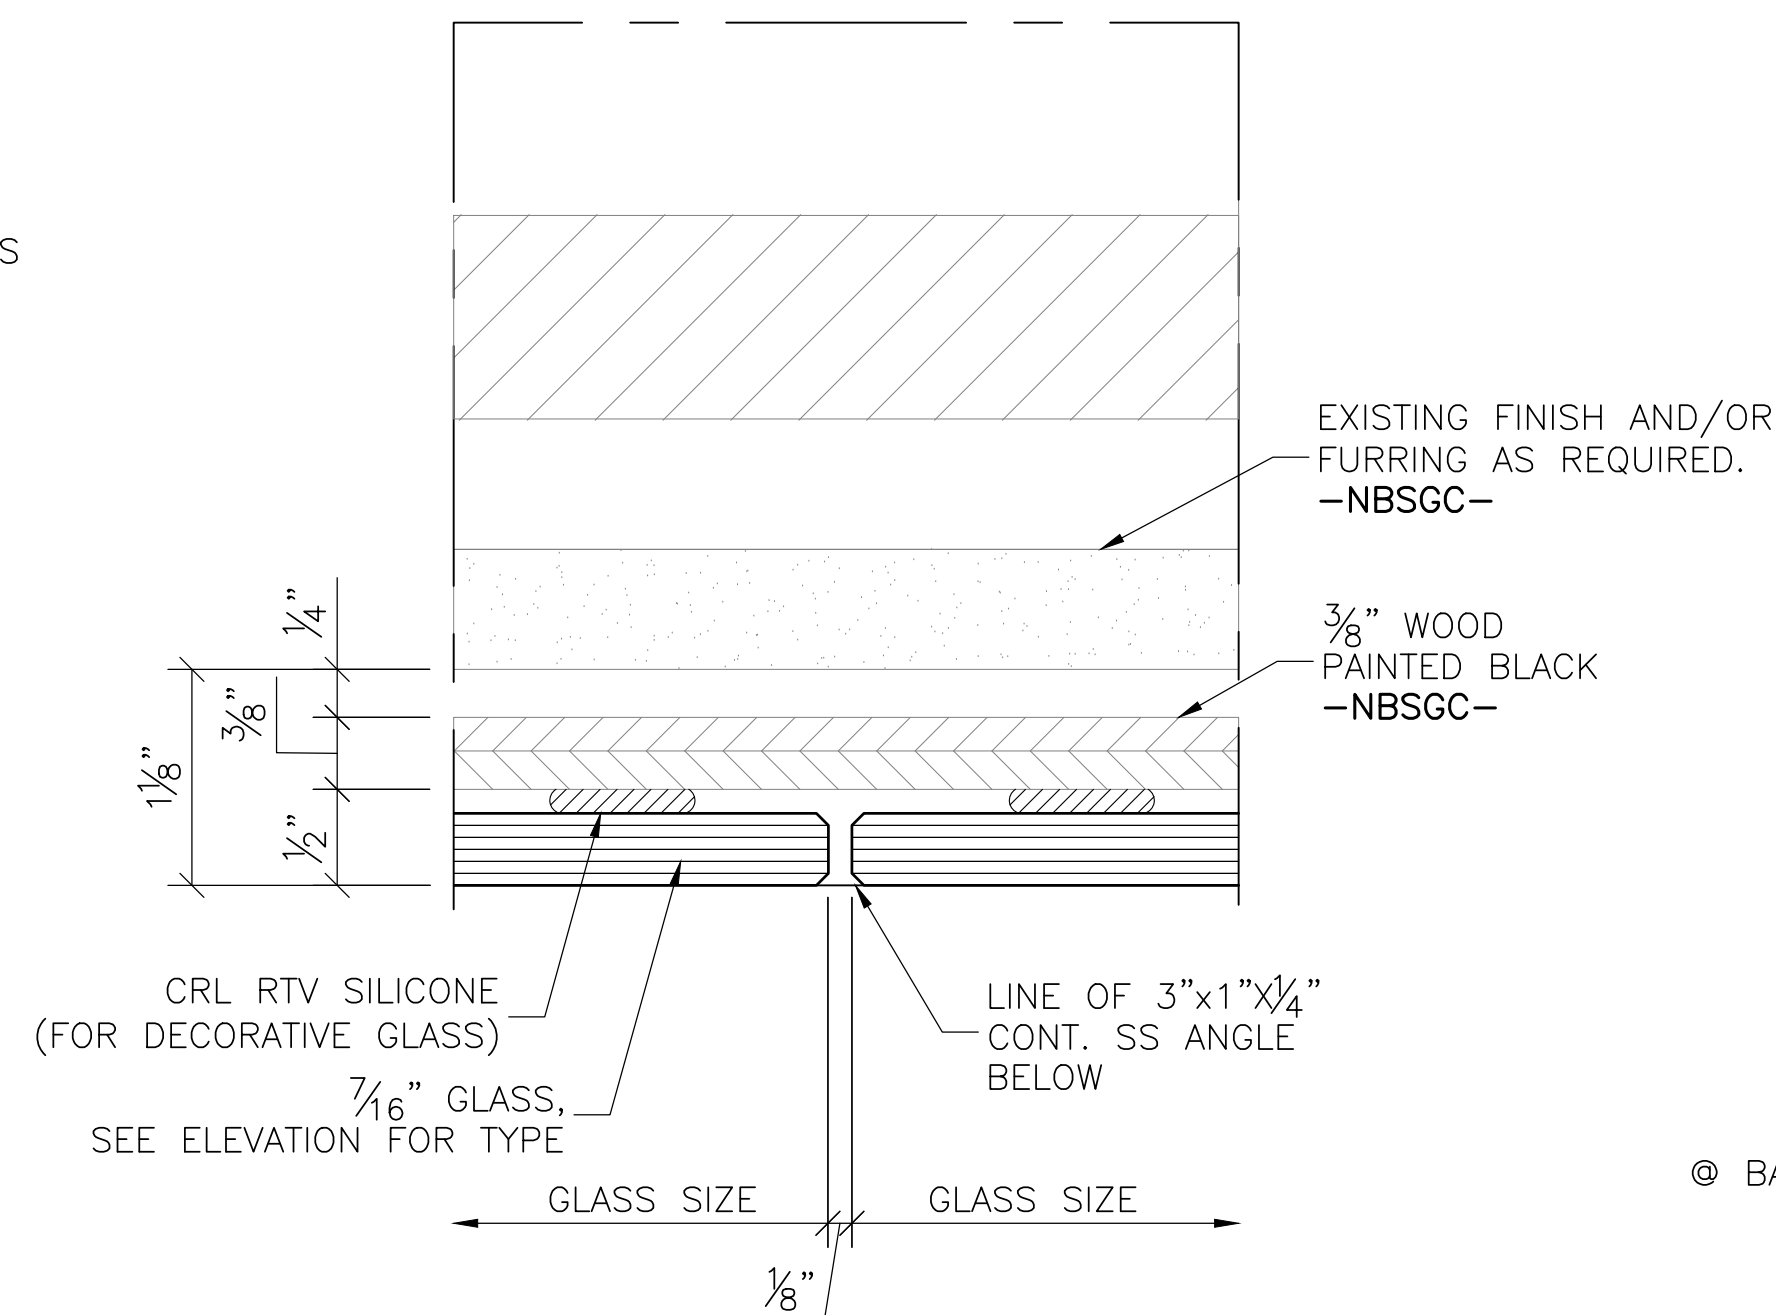

V4
BUTT JOINT
© BACK PAINTED GLASS
ARCH REF: NONE

PROJECT	ARCHITECT	GENERAL CONTRACTOR	DESCRIPTION	BY	DATE	REV
KIRKLAND & ELLIS	HO&K	STRUCTURE TONE, INC				
PROJ NO	8901					
DATE	5/4/26					
DRAWN	SM					
CHECKED	SB/MO					
FILE NAME	8109 v 1					
SCALE	FULL SCALE					
SHEET NUMBER	V101					



PROJECT	KIRKLAND & ELLIS
ARCHITECT	HO&K
GENERAL CONTRACTOR	STRUCTURE TONE INC.

SHEET NUMBER	V102
-----------------	------

