



INTERIOR GLAZING

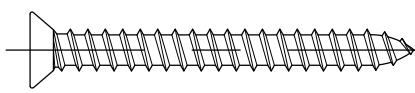


PROJECT	PROJ NO	8901	REV	DATE	BY	DESCRIPTION
KIRKLAND & ELLIS	DATE	WORKING				
ARCHITECT	DRAWN	SM				
HO&K	CHECKED	SB/MO				
GENERAL CONTRACTOR	FILE NAME	8109 c 1				
STRUCTURE TONE, INC	SCALE	NO SCALE				
	SHEET NUMBER	C101				

INTERIOR GLAZING FASTENER INDEX

FASTENER#:	1	IMAGE: 
PART#:		
FASTENAL #1173058		
DESCRIPTION:		#12-11 X 2" PFH TYPE-A SMS *18-8SS

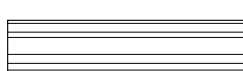FASTENER#:		2	IMAGE:  ✓ SGC INVENTORY
PART#:			
#FA083			
FASTENAL #50985			
.			
.			
DESCRIPTION: #10/#12 GREEN MASONRY PLUG *PLASTIC			

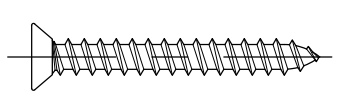FASTENER#:	3	IMAGE: 
PART#:		
FASTENAL #1173036		
.		
.		
.		
DESCRIPTION:		#10-12 x 1-1/2" PFH TYPE-A SMS *18-8SS



PROJECT	KIRKLAND & ELLIS	PROJ NO	8901
ARCHITECT	HO&K	DATE	WORKING
GENERAL CONTRACTOR	STRUCTURE TONE, INC	DRAWN	SM
		CHECKED	SB/MO
		FILE NAME	8109 c 1
		SCALE	NO SCALE
		SHEET NUMBER	C102



SALEM GLASS COMPANY
3 Technology Way, Salem, MA 01970
Phone# (978)744-5177 Fax# (978)745-4036

DESCRIPTION

BY

DATE

REV


PROJECT
KIRKLAND & ELLIS

ARCHITECT
HO&K

GENERAL CONTRACTOR
STRUCTURE TONE, INC

PROJ NO	8901
DATE	WORKING
DRAWN	SM
CHECKED	SB/MO
FILE NAME	8109 p 1
SCALE	1/8"=1'-0"

SHEET NUMBER	P101
--------------	------

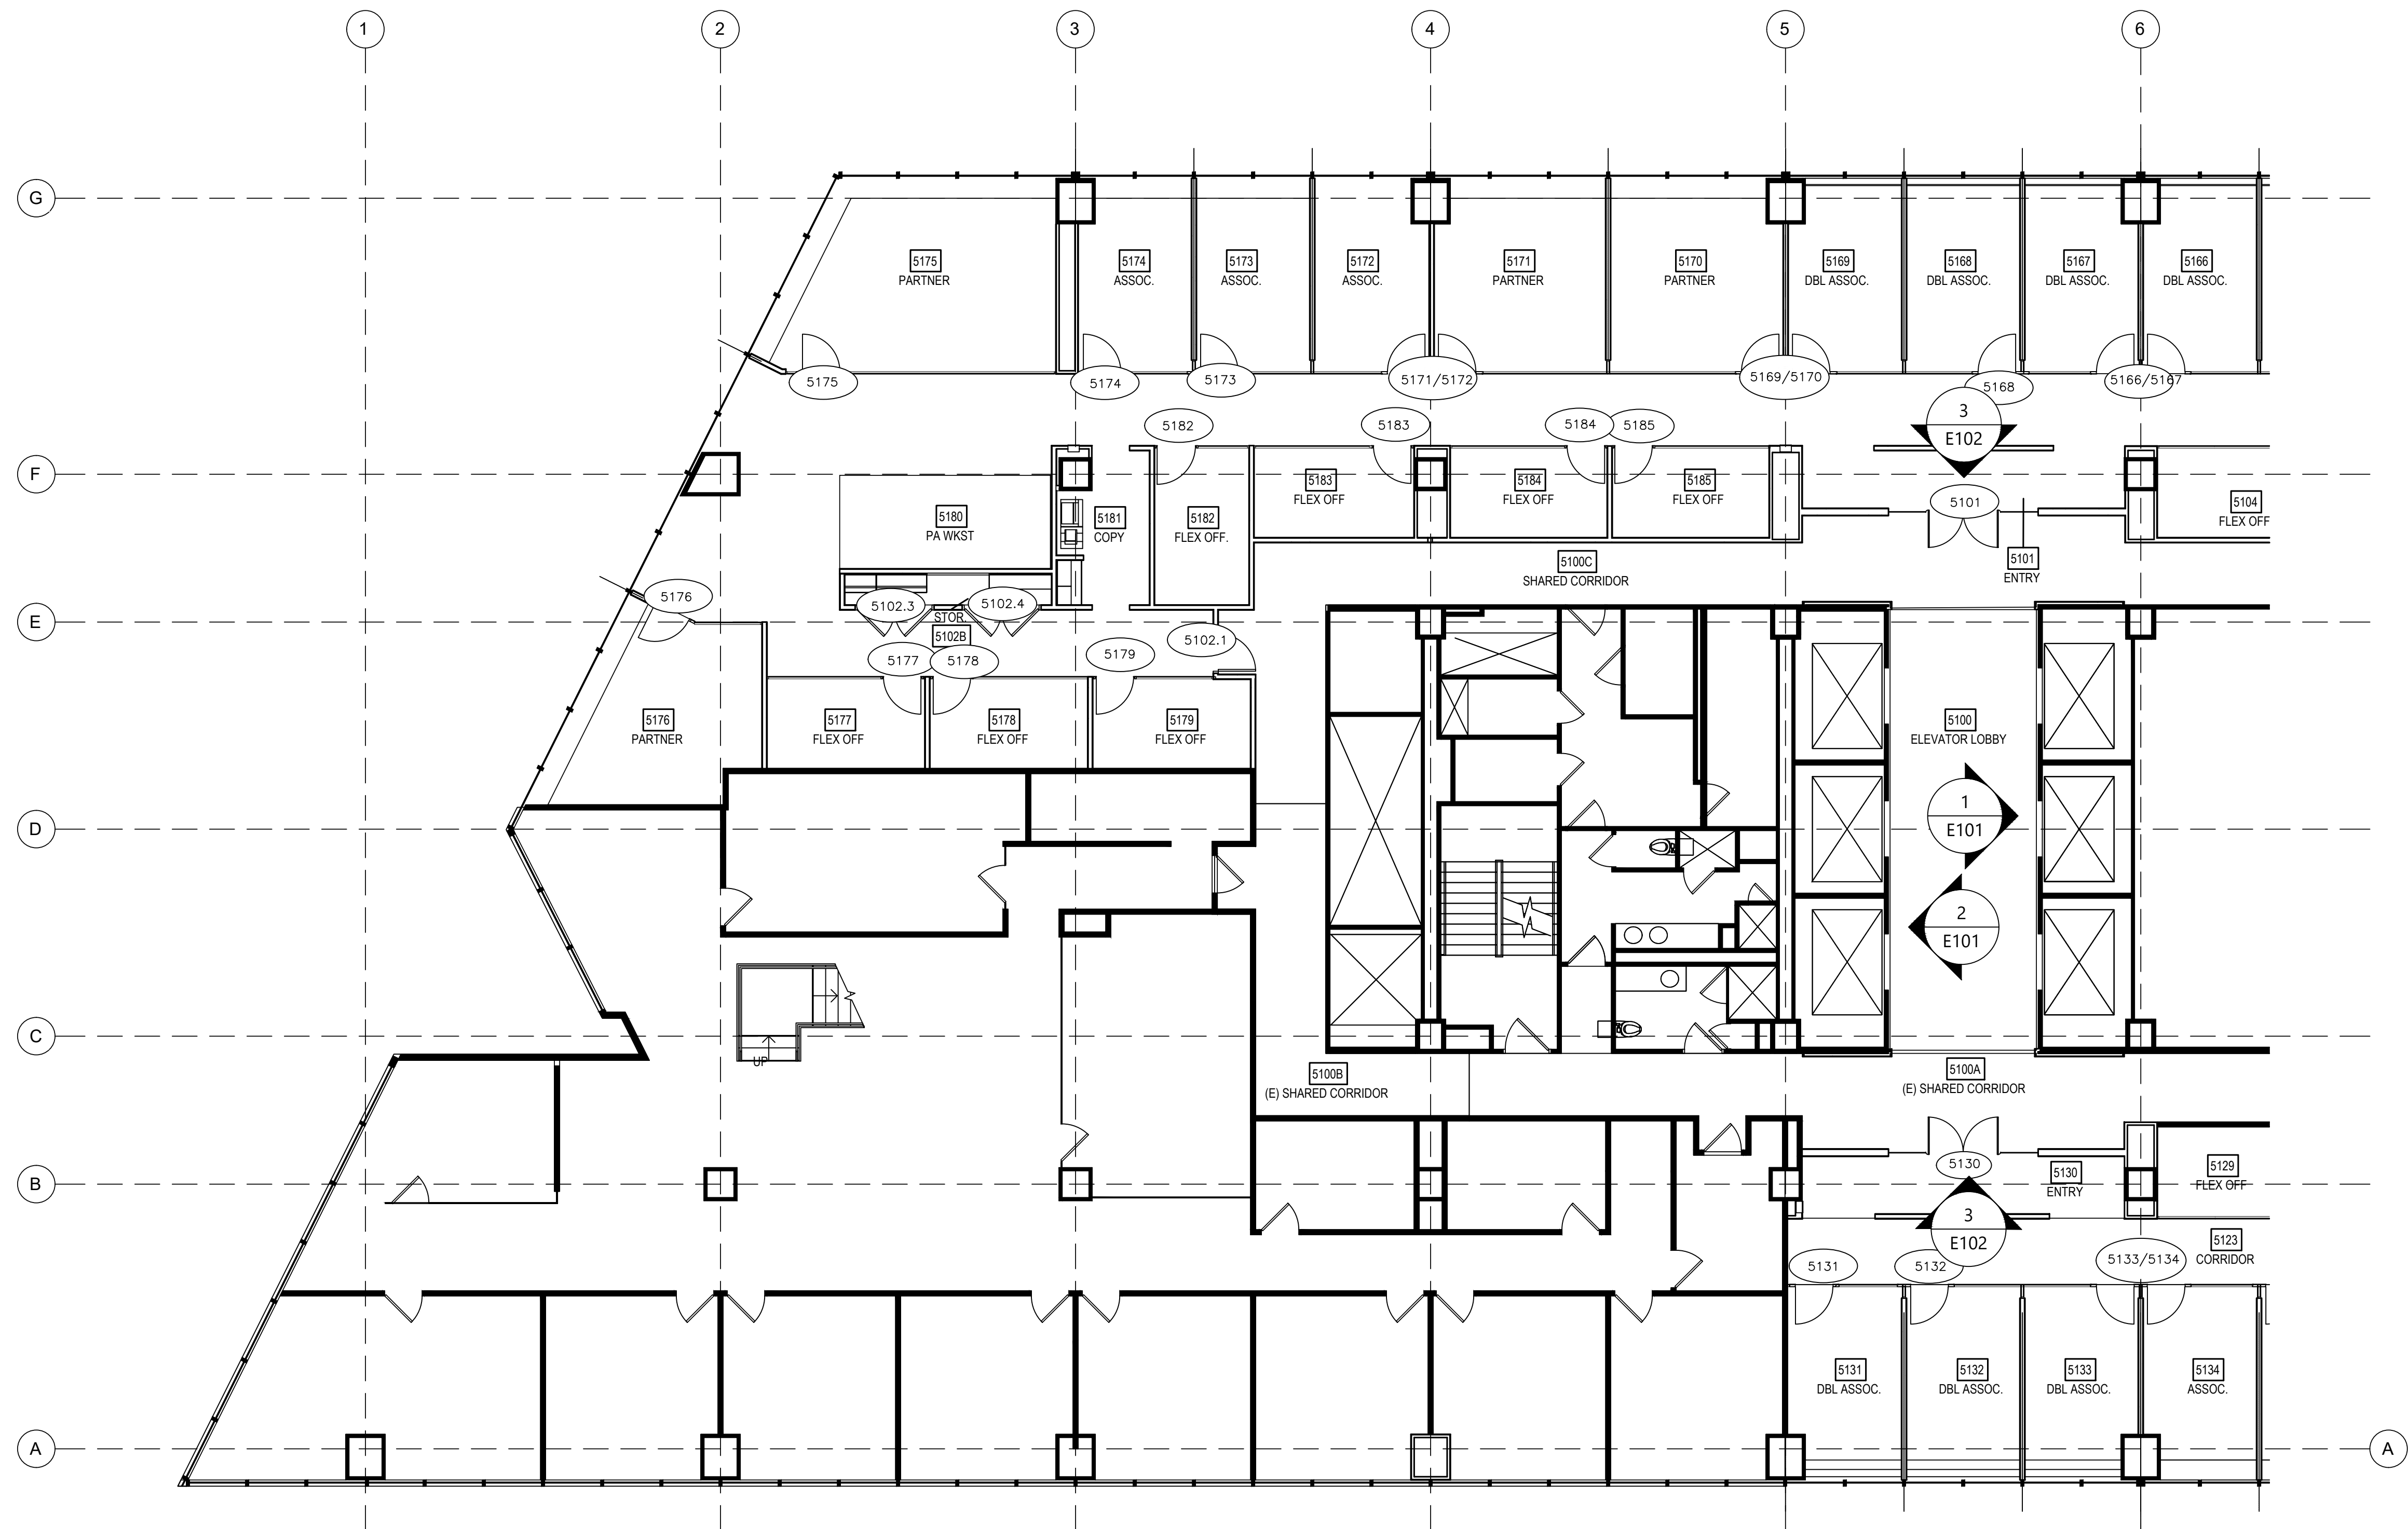

A LEVEL 51— FINISH PLAN— PART A
ARCH REF: 1/A401A




WE DO NOT NEED THESE
STRINGS OF DIMS. THERE ARE
NO DLOS.
KEEP IF YOU WANT.



SG
SC
EST. 1929

SALEM GLASS COMPANY
3 Technology Way, Salem, MA 01970
tel (978)744-5177 Fax# (978)745-4036

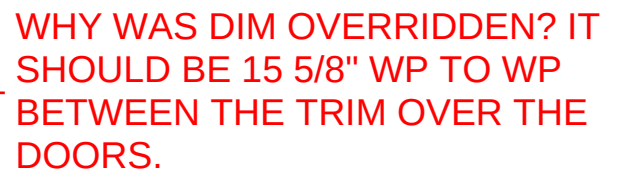

CHECK PICK POINT

SAME HERE

2 ELEVATION—WEST
QUANTITY: 1
ARCH REF: 2/A803
@ ELEVATOR LOBBY 5100


[illegible]

ALL DIMENSIONS TO BE
VERIFIED IN FIELD BY SGC
PRIOR TO FABRICATION

GL1	7/16" ACID ETCH LAMINATED MIRROR
GL2	1/2" CLEAR TEMPERED GLASS






SALEM GLASS COMPANY
3 Technology Way, Salem, MA 01970
Phone# (978)744-5177 Fax# (978)745-4036

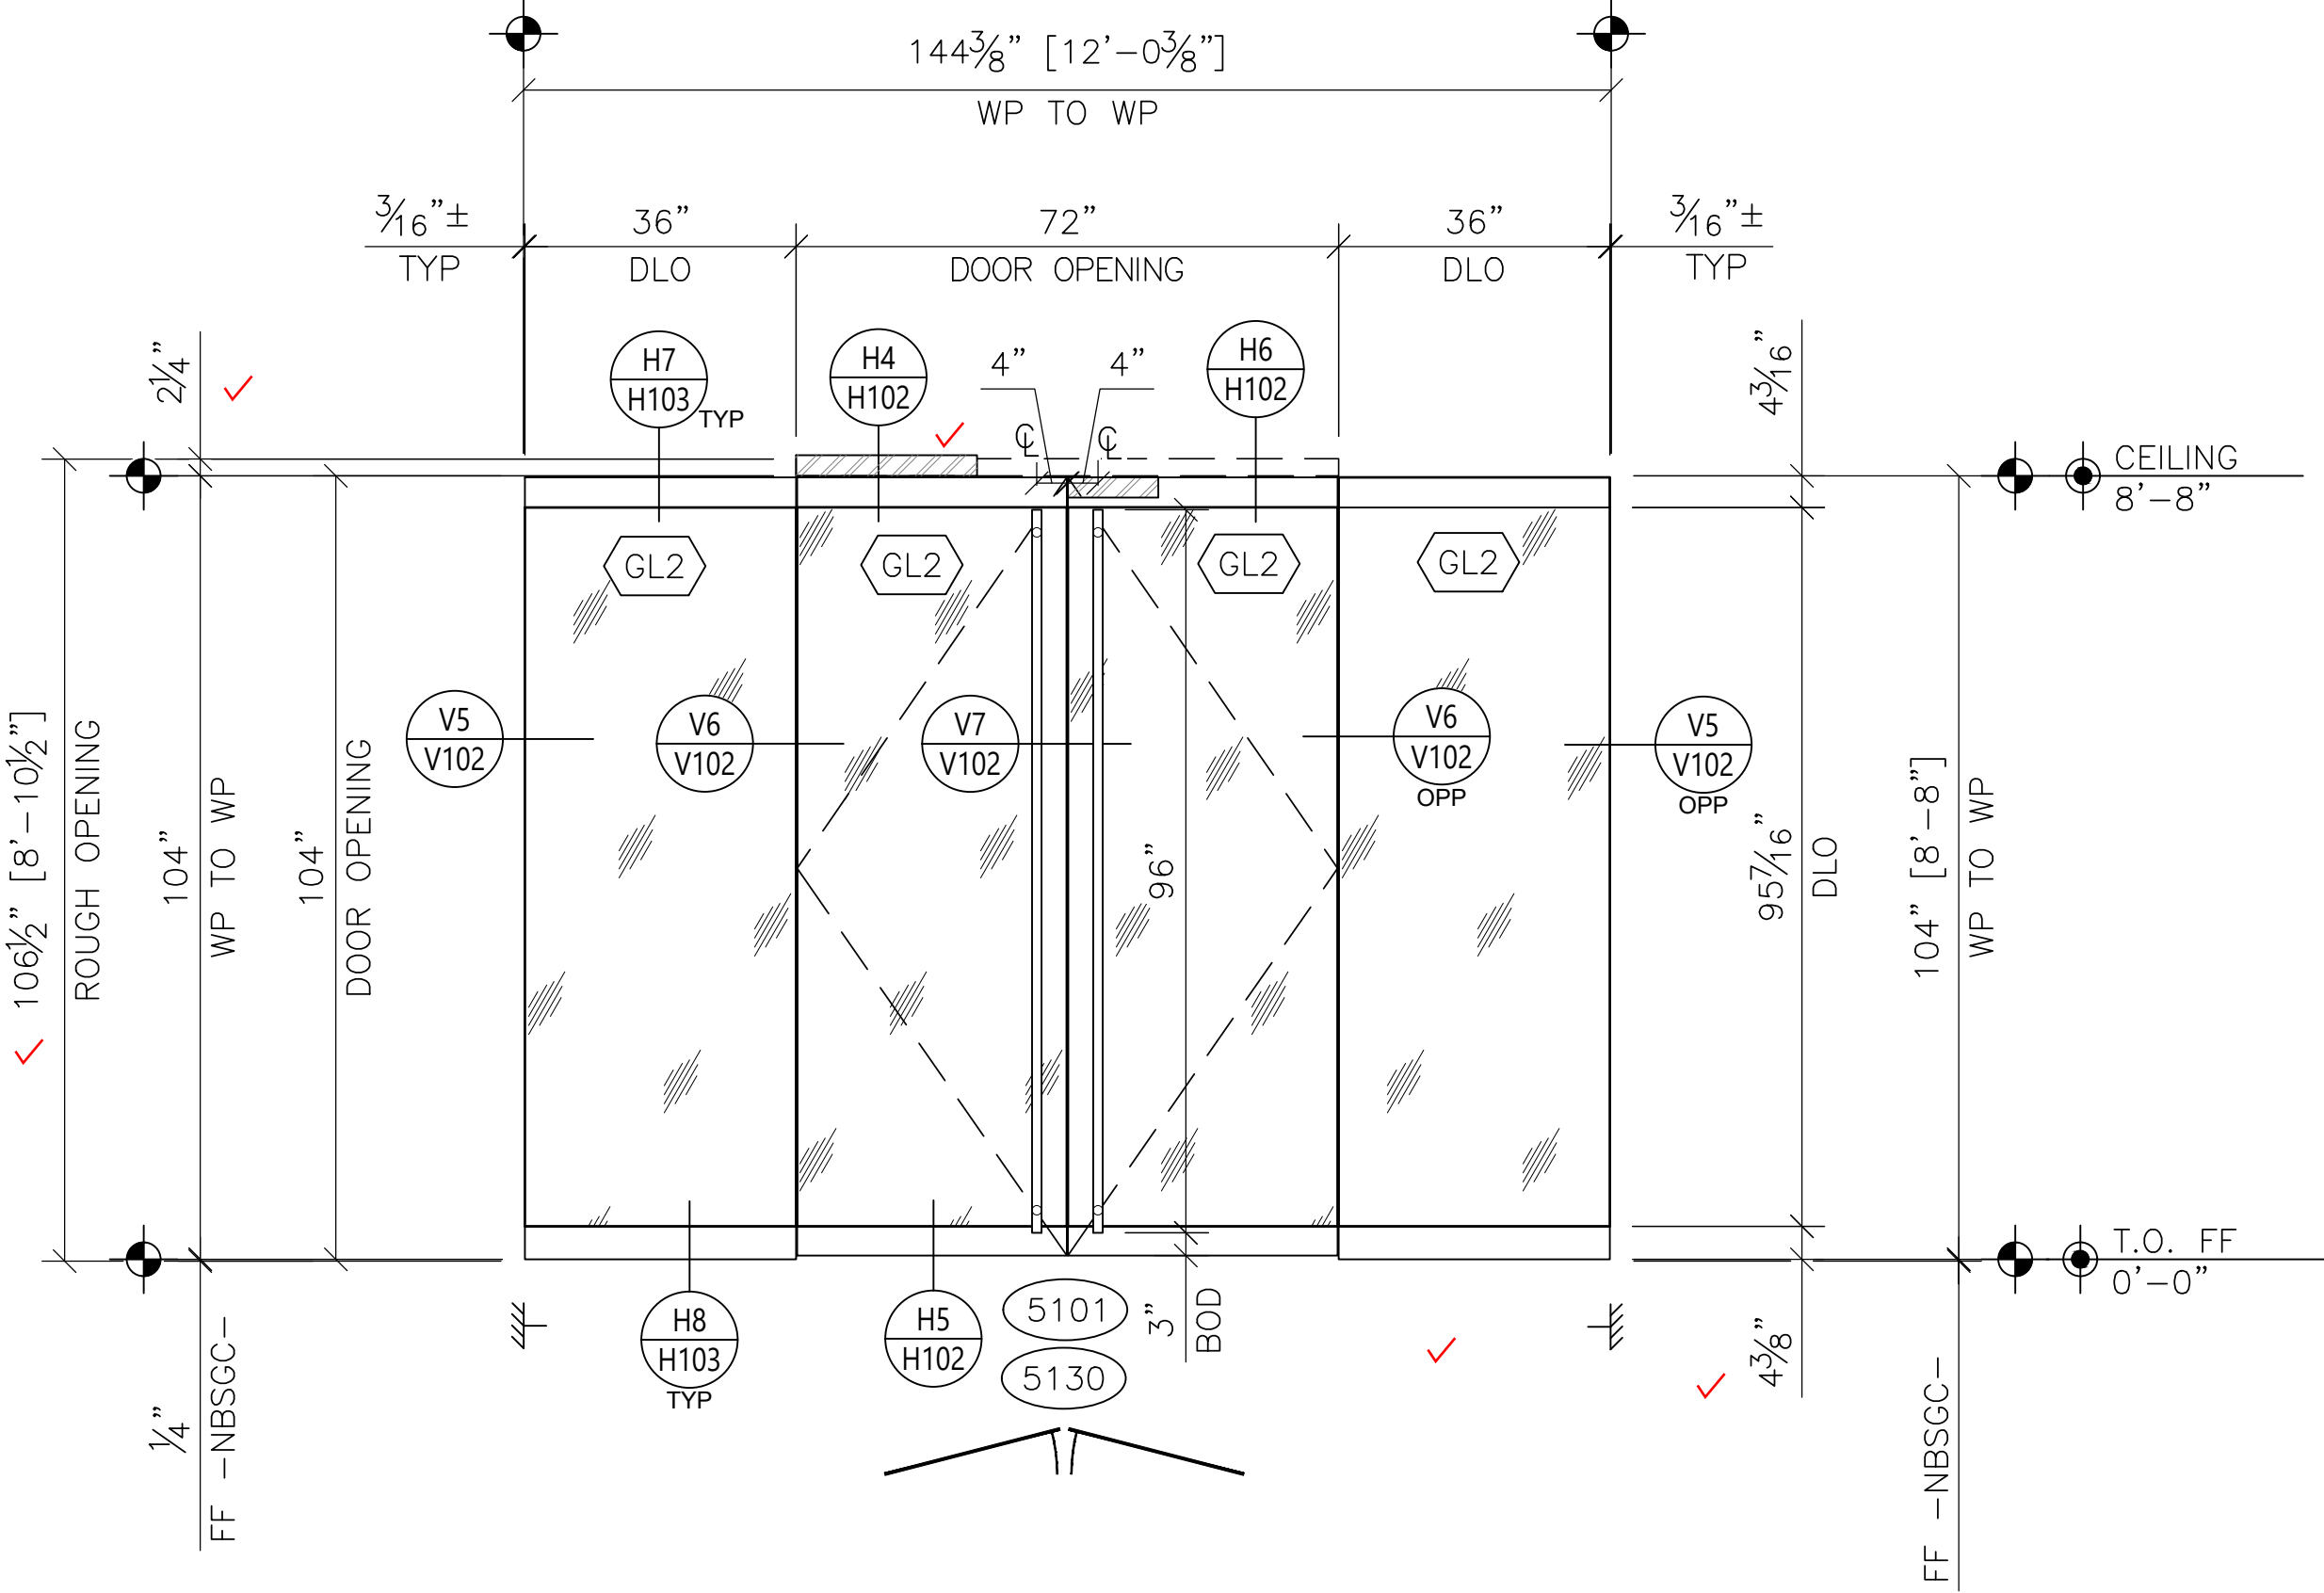


3 ELEVATION-ELEVATOR LOBBY-NORTH & SOUTH
QUANTITY: 2
ARCH REF: 1&3/A803
✓

[illegible]

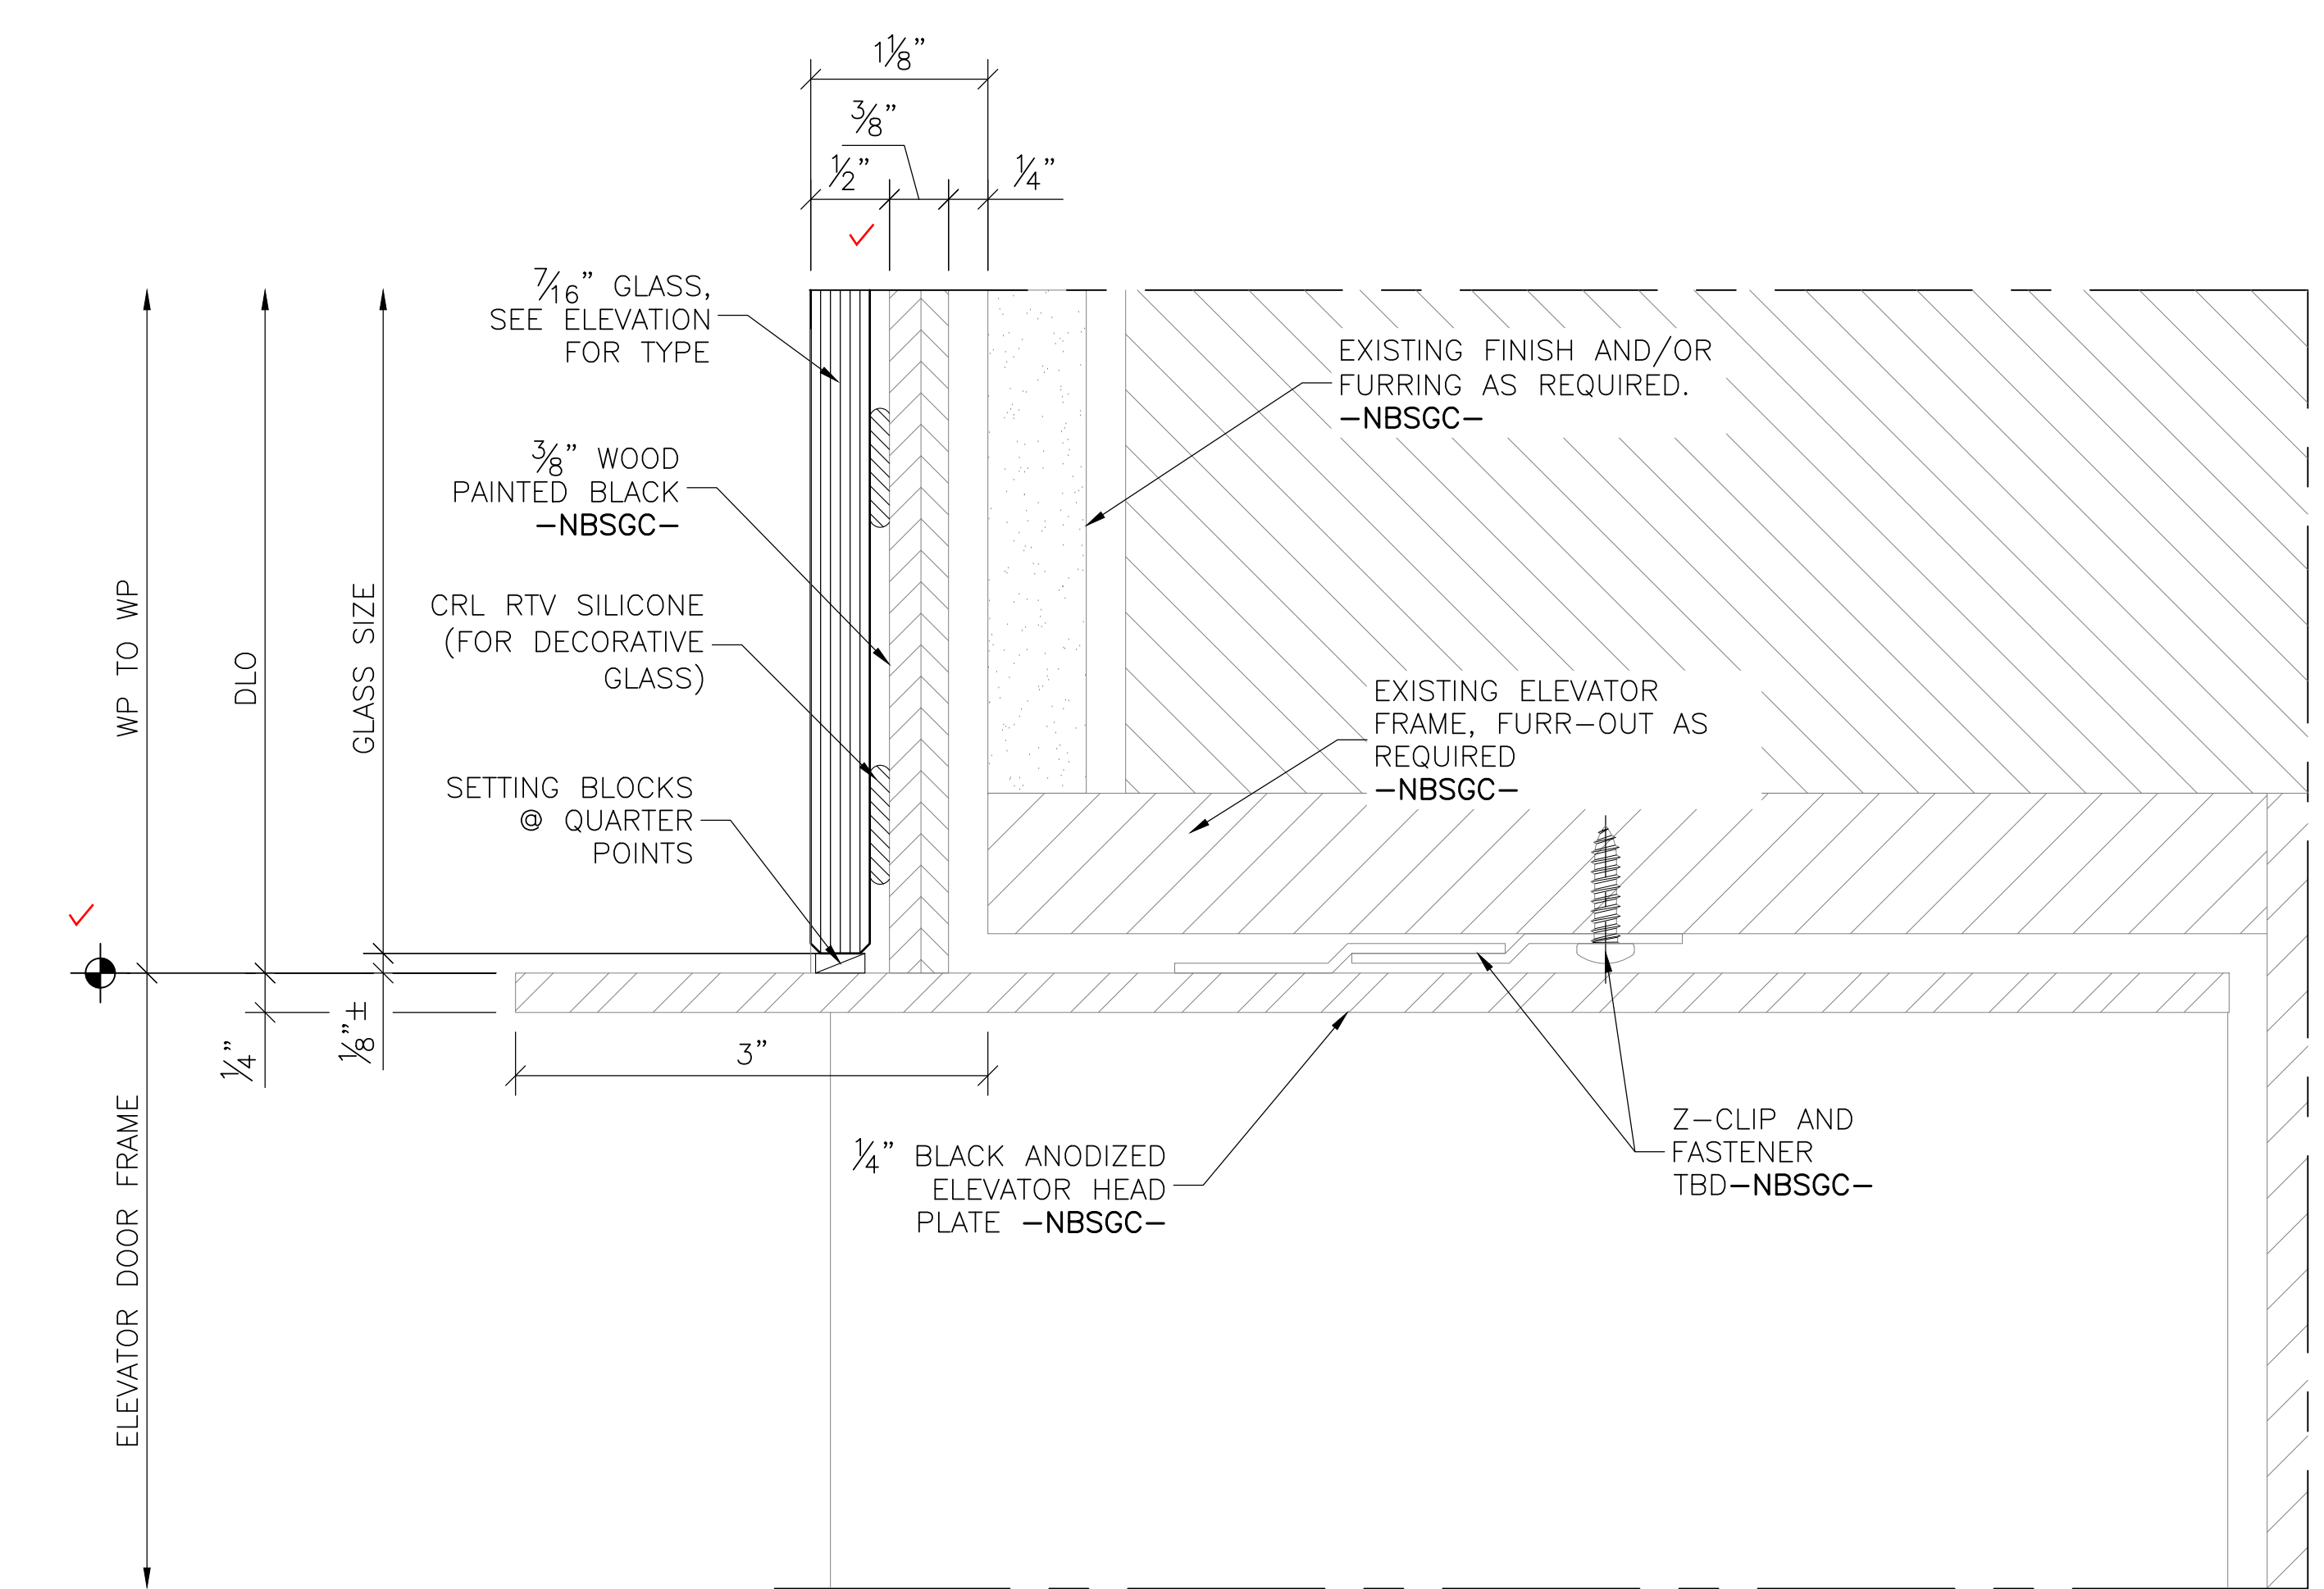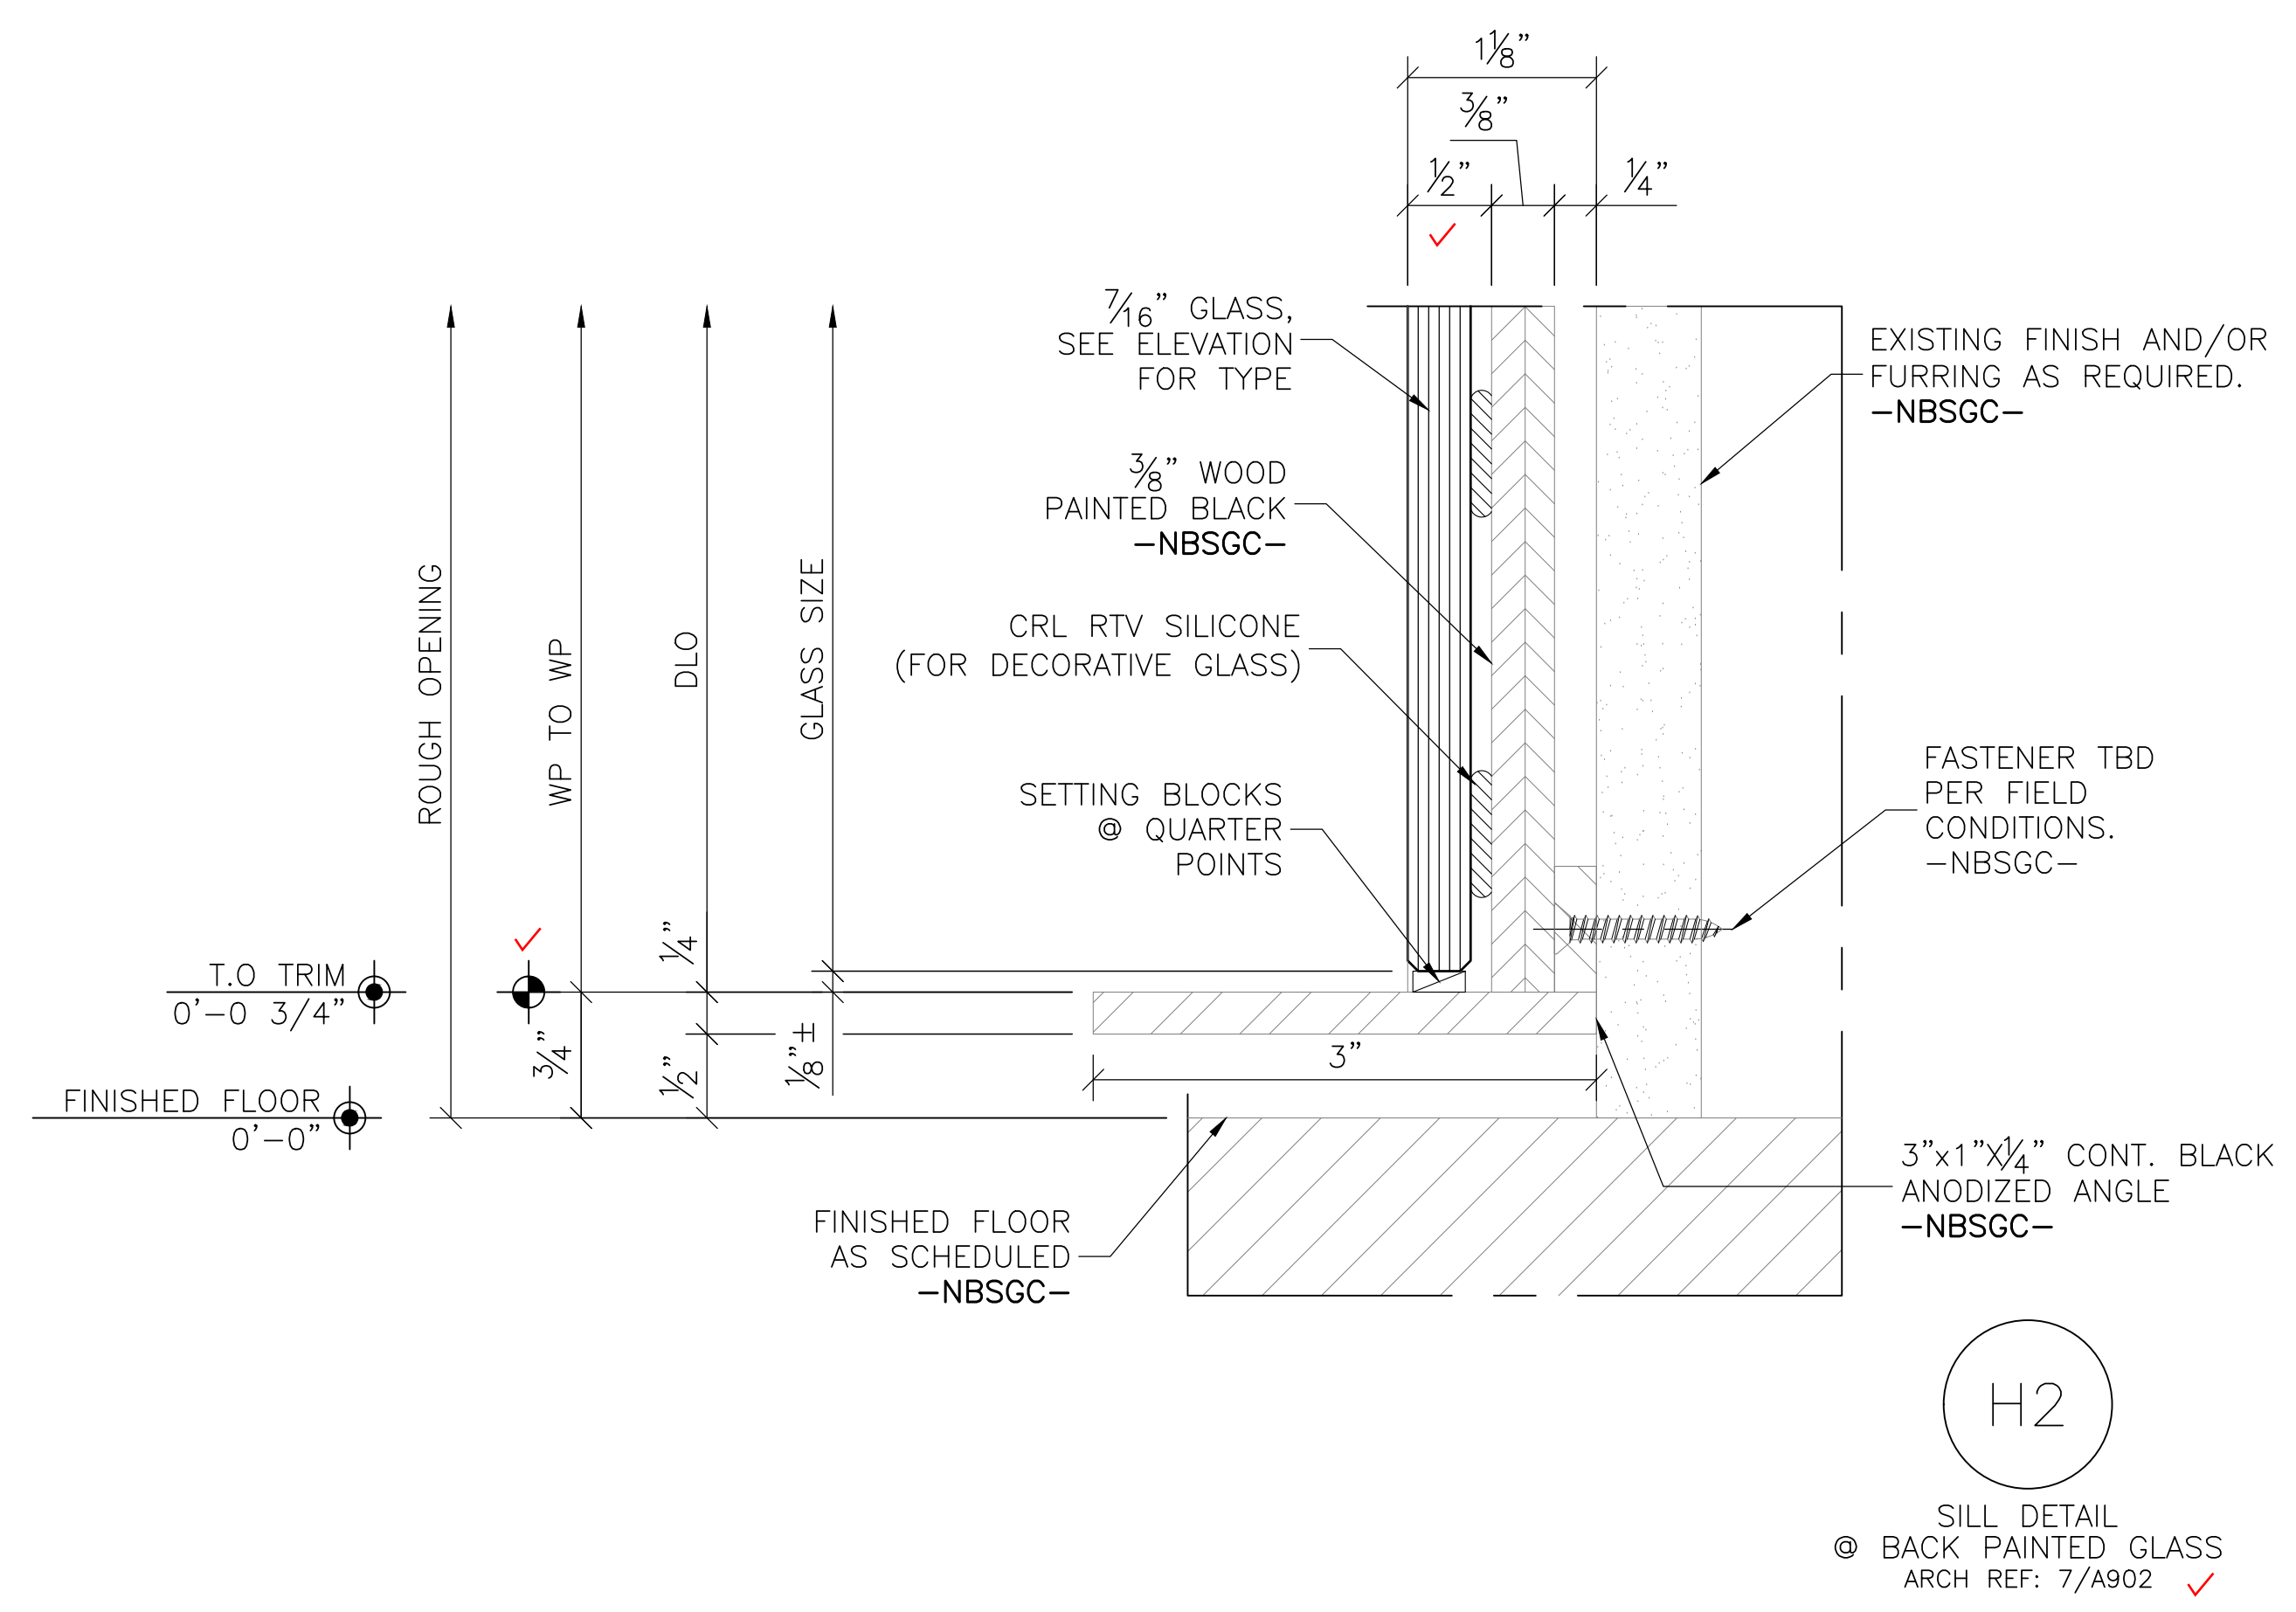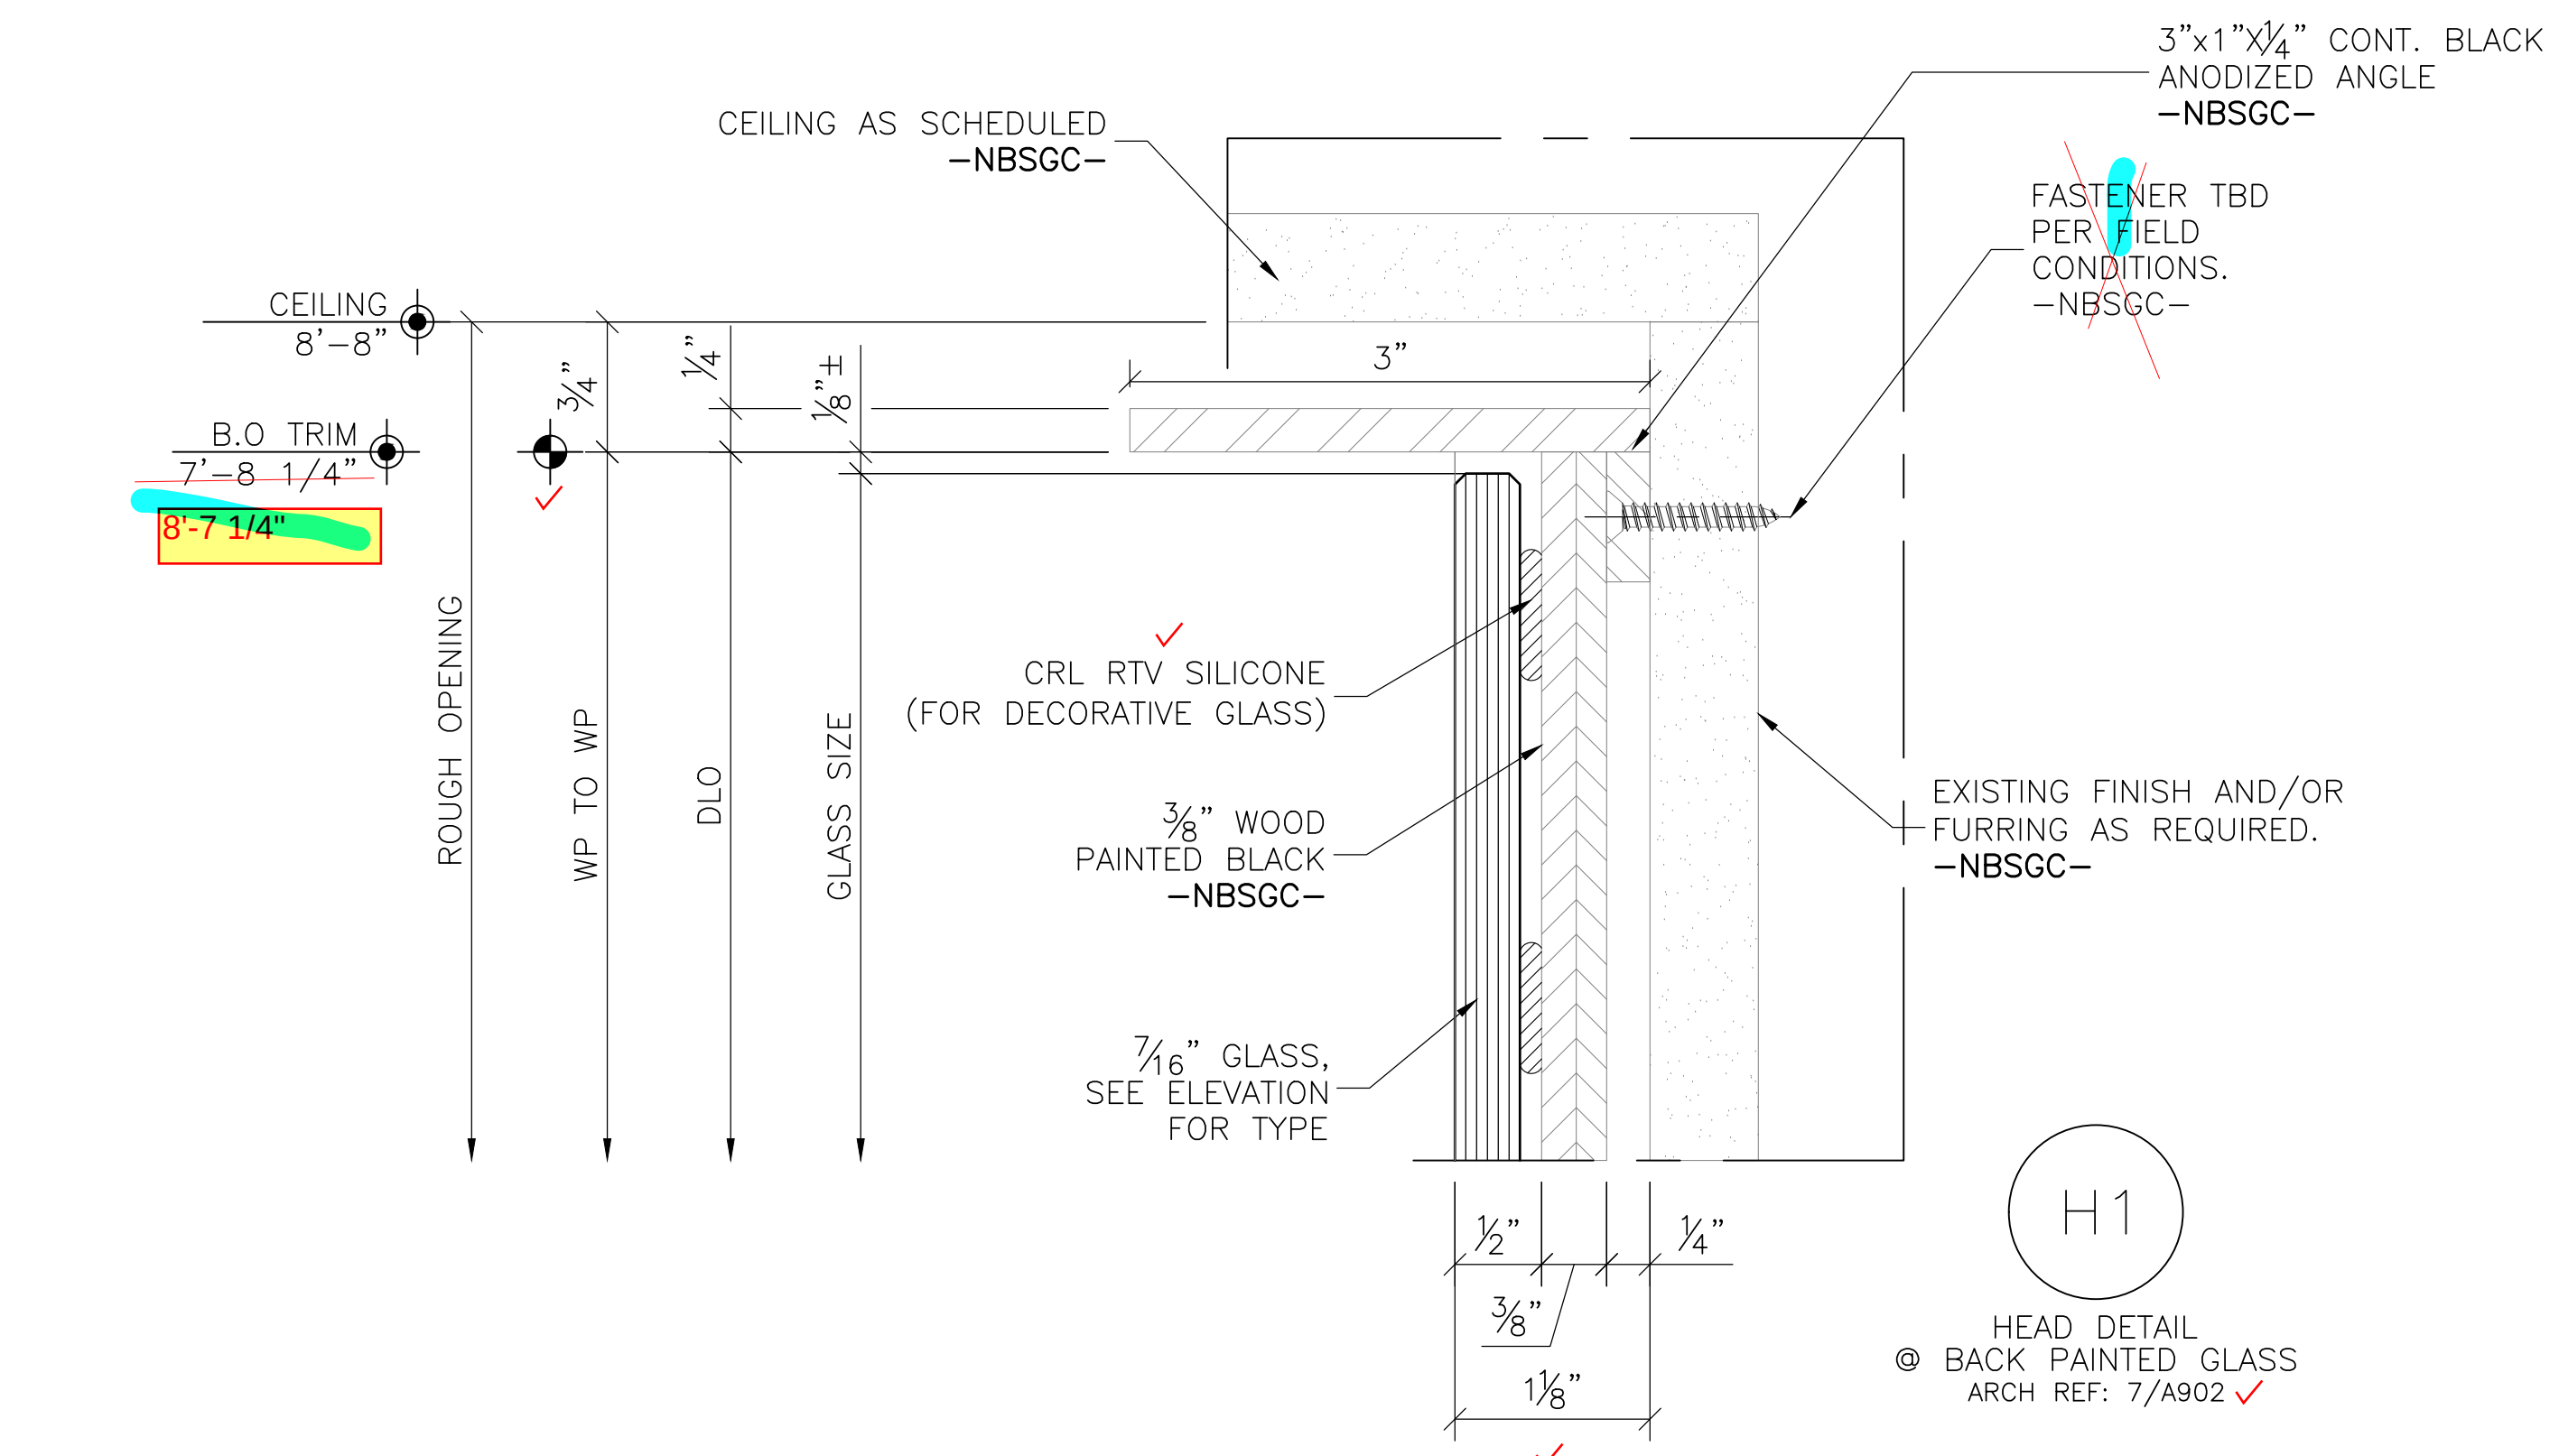


ARCHITECT/GC NOTE:
AT BACKPAINTED GLASS LOCATIONS ADHERED TO WOOD, THE WOOD SHOULD BE UNPRIMED/PAINTED, FREE OF DUST AND NOT BE FIRE RATED.

PROJECT	ARCHITECT	GENERAL CONTRACTOR
KIRKLAND & ELLIS	HO&K	STRUCTURE TONE, INC
PROJ NO	8901	
DATE	WORKING	
DRAWN	SM	
CHECKED	SB/MO	
FILE NAME	8109 h 1	
SCALE	FULL SCALE	
SHEET NUMBER	H101	

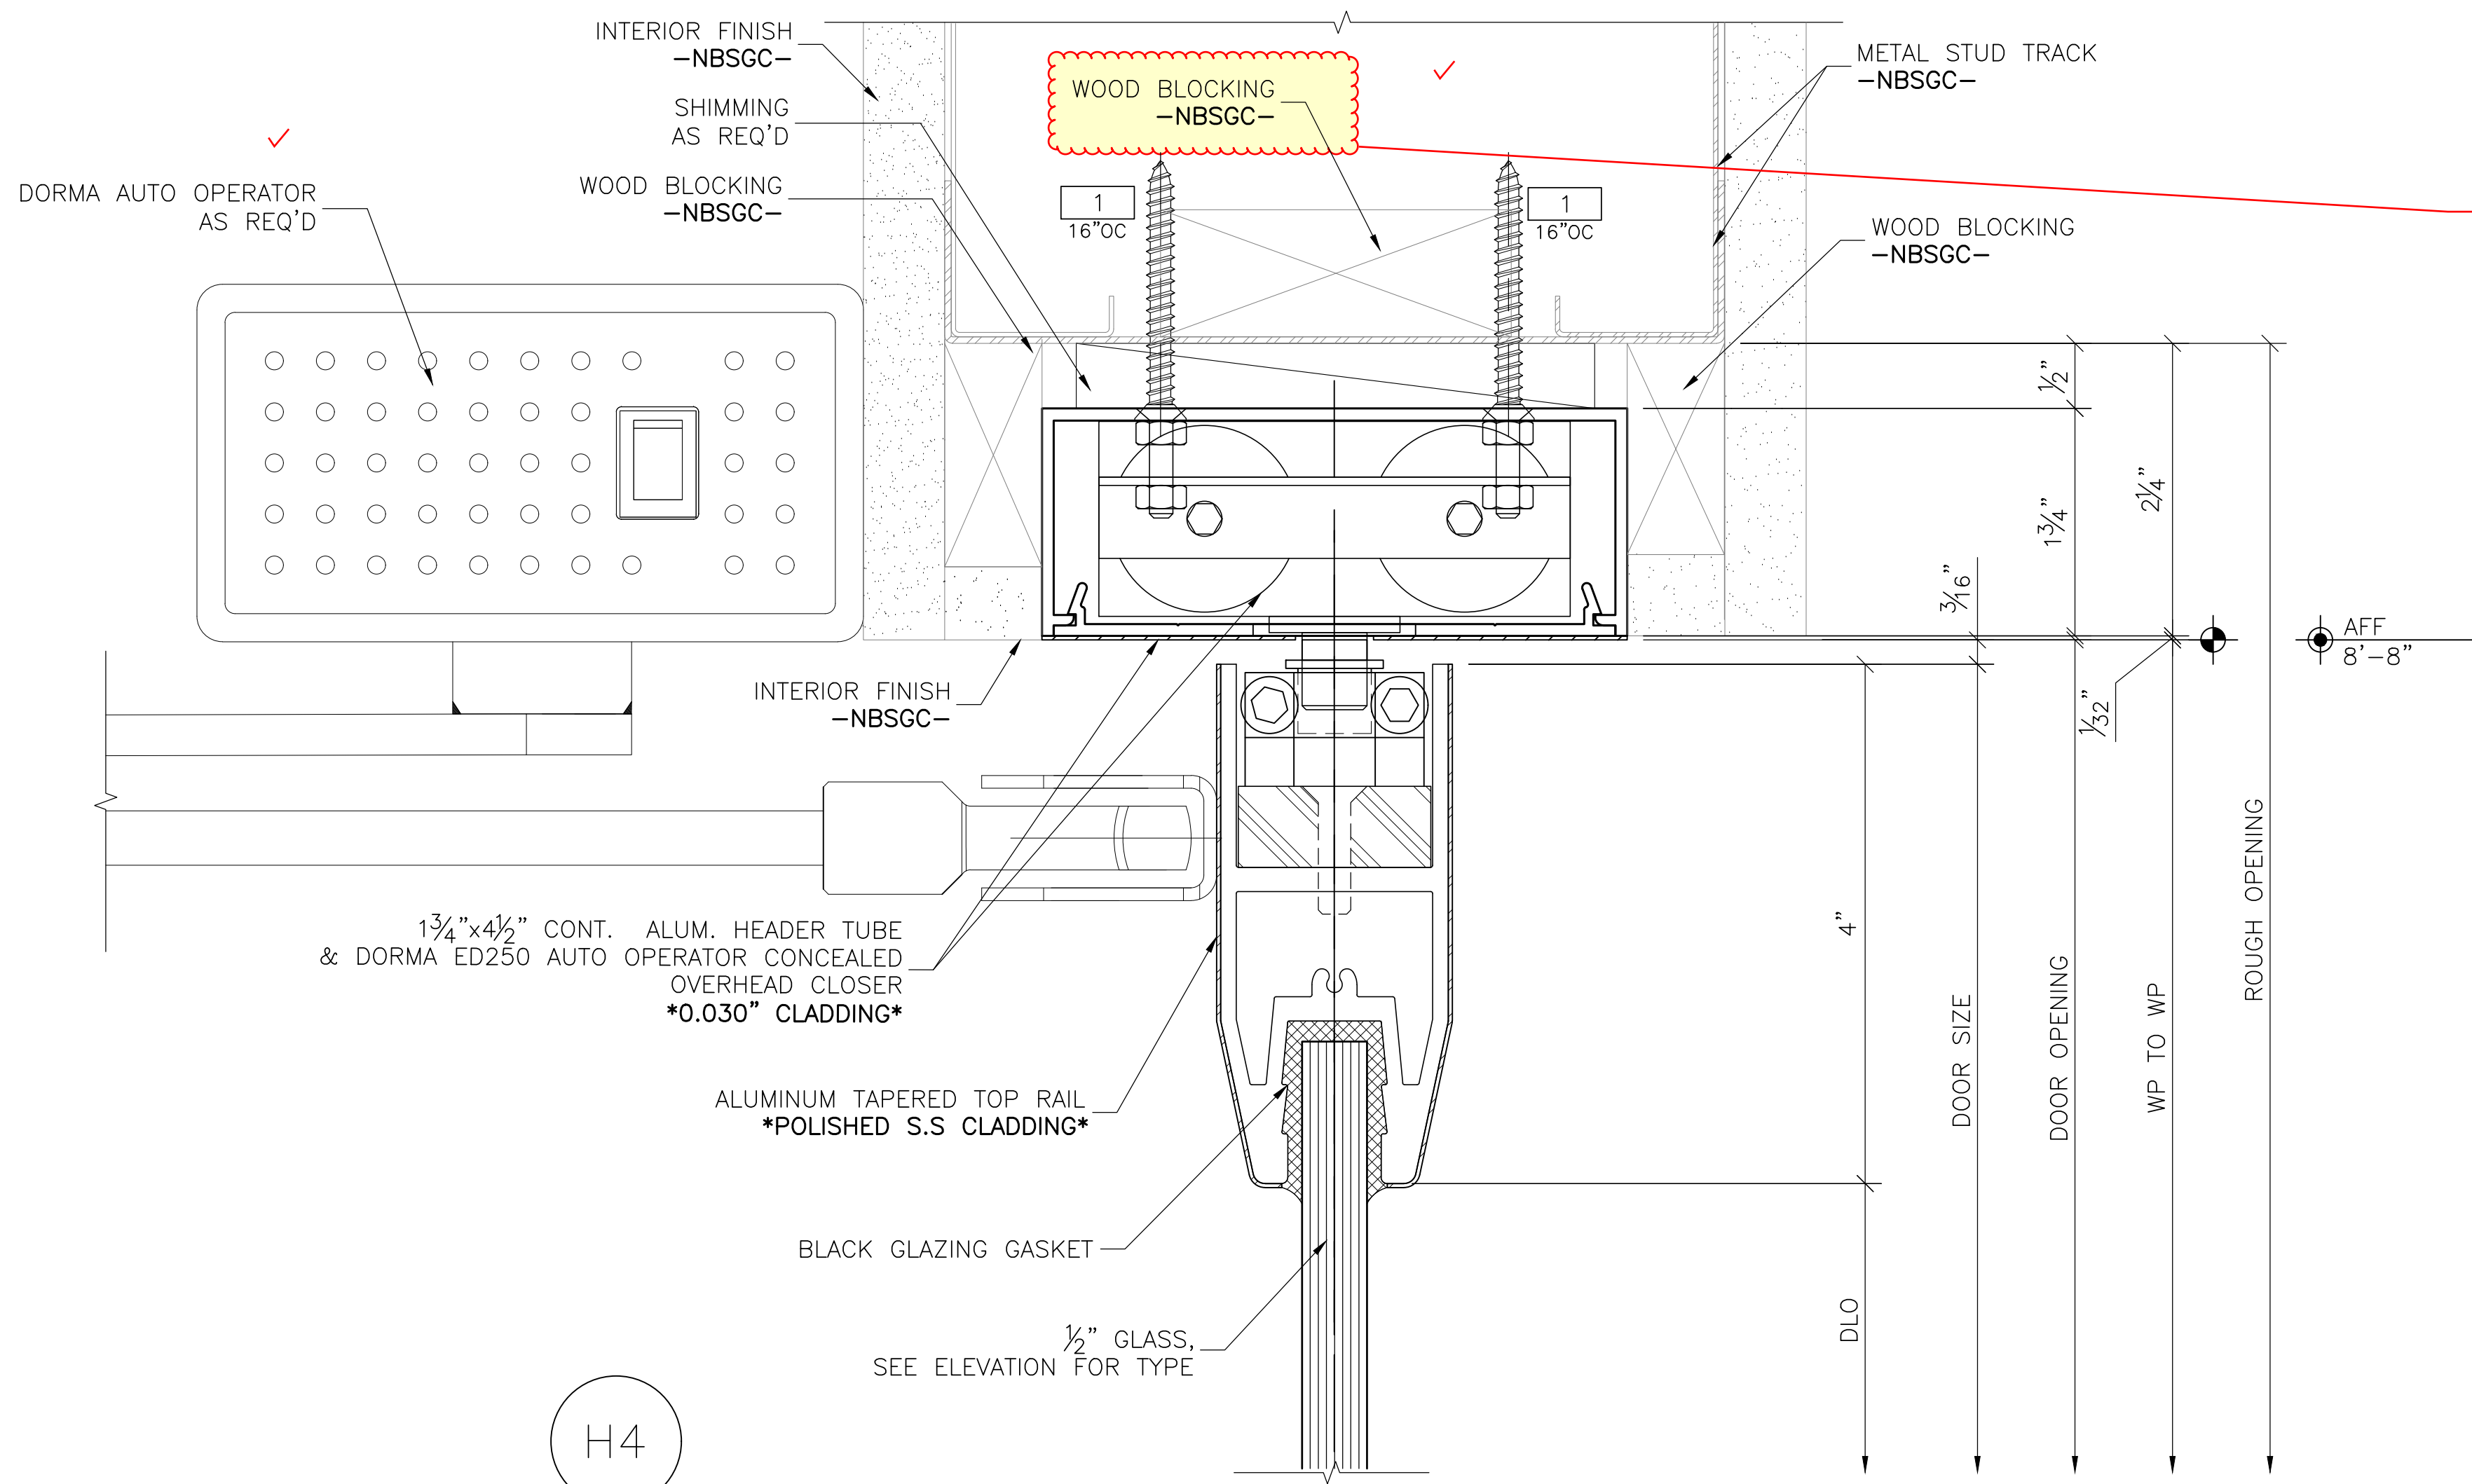


H4
DOOR HEAD DETAIL
W/ CLAD TOP RAIL & HEADER TUBE COC & DORMA AUTO OP
ARCH REF: NONE

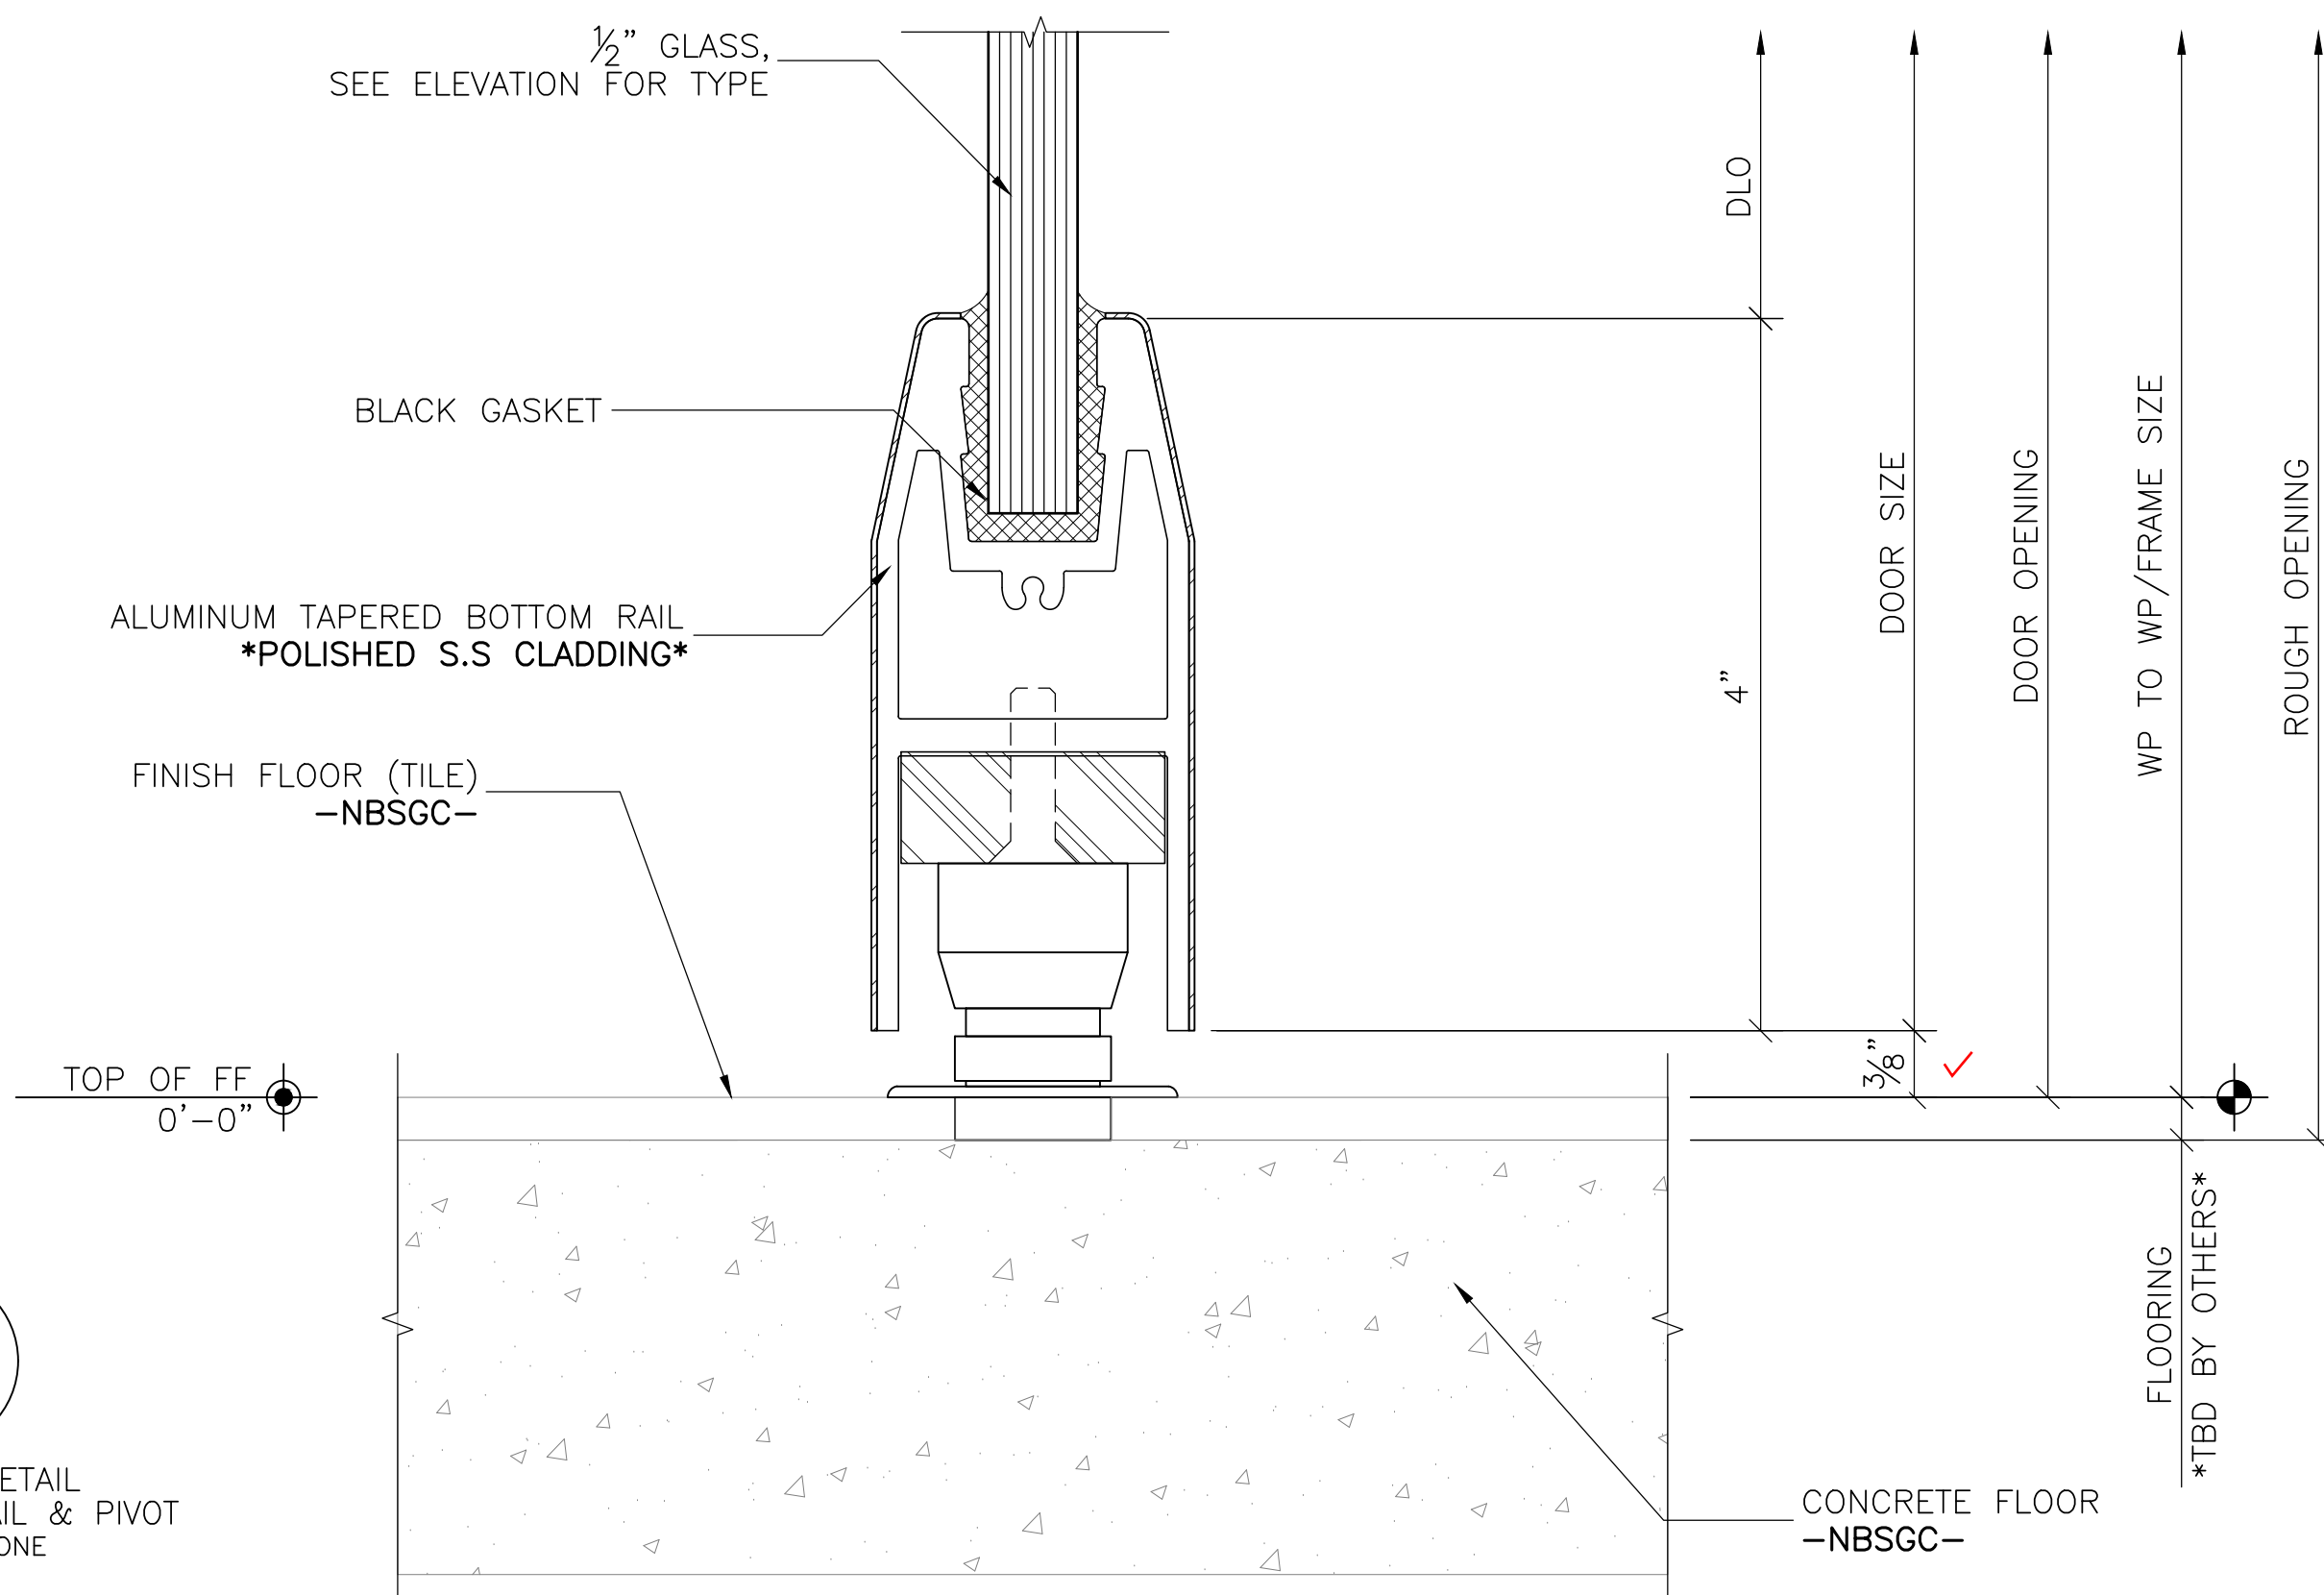

H5
DOOR SILL DETAIL
W/ CLAD BOTTOM RAIL & PIVOT
ARCH REF: NONE

I THINK WE NEED TO FIX THE
BLOCKING SO IT AT LEAST LOOKS
LIKE THE FASTENERS ARE GOING
INTO IT...

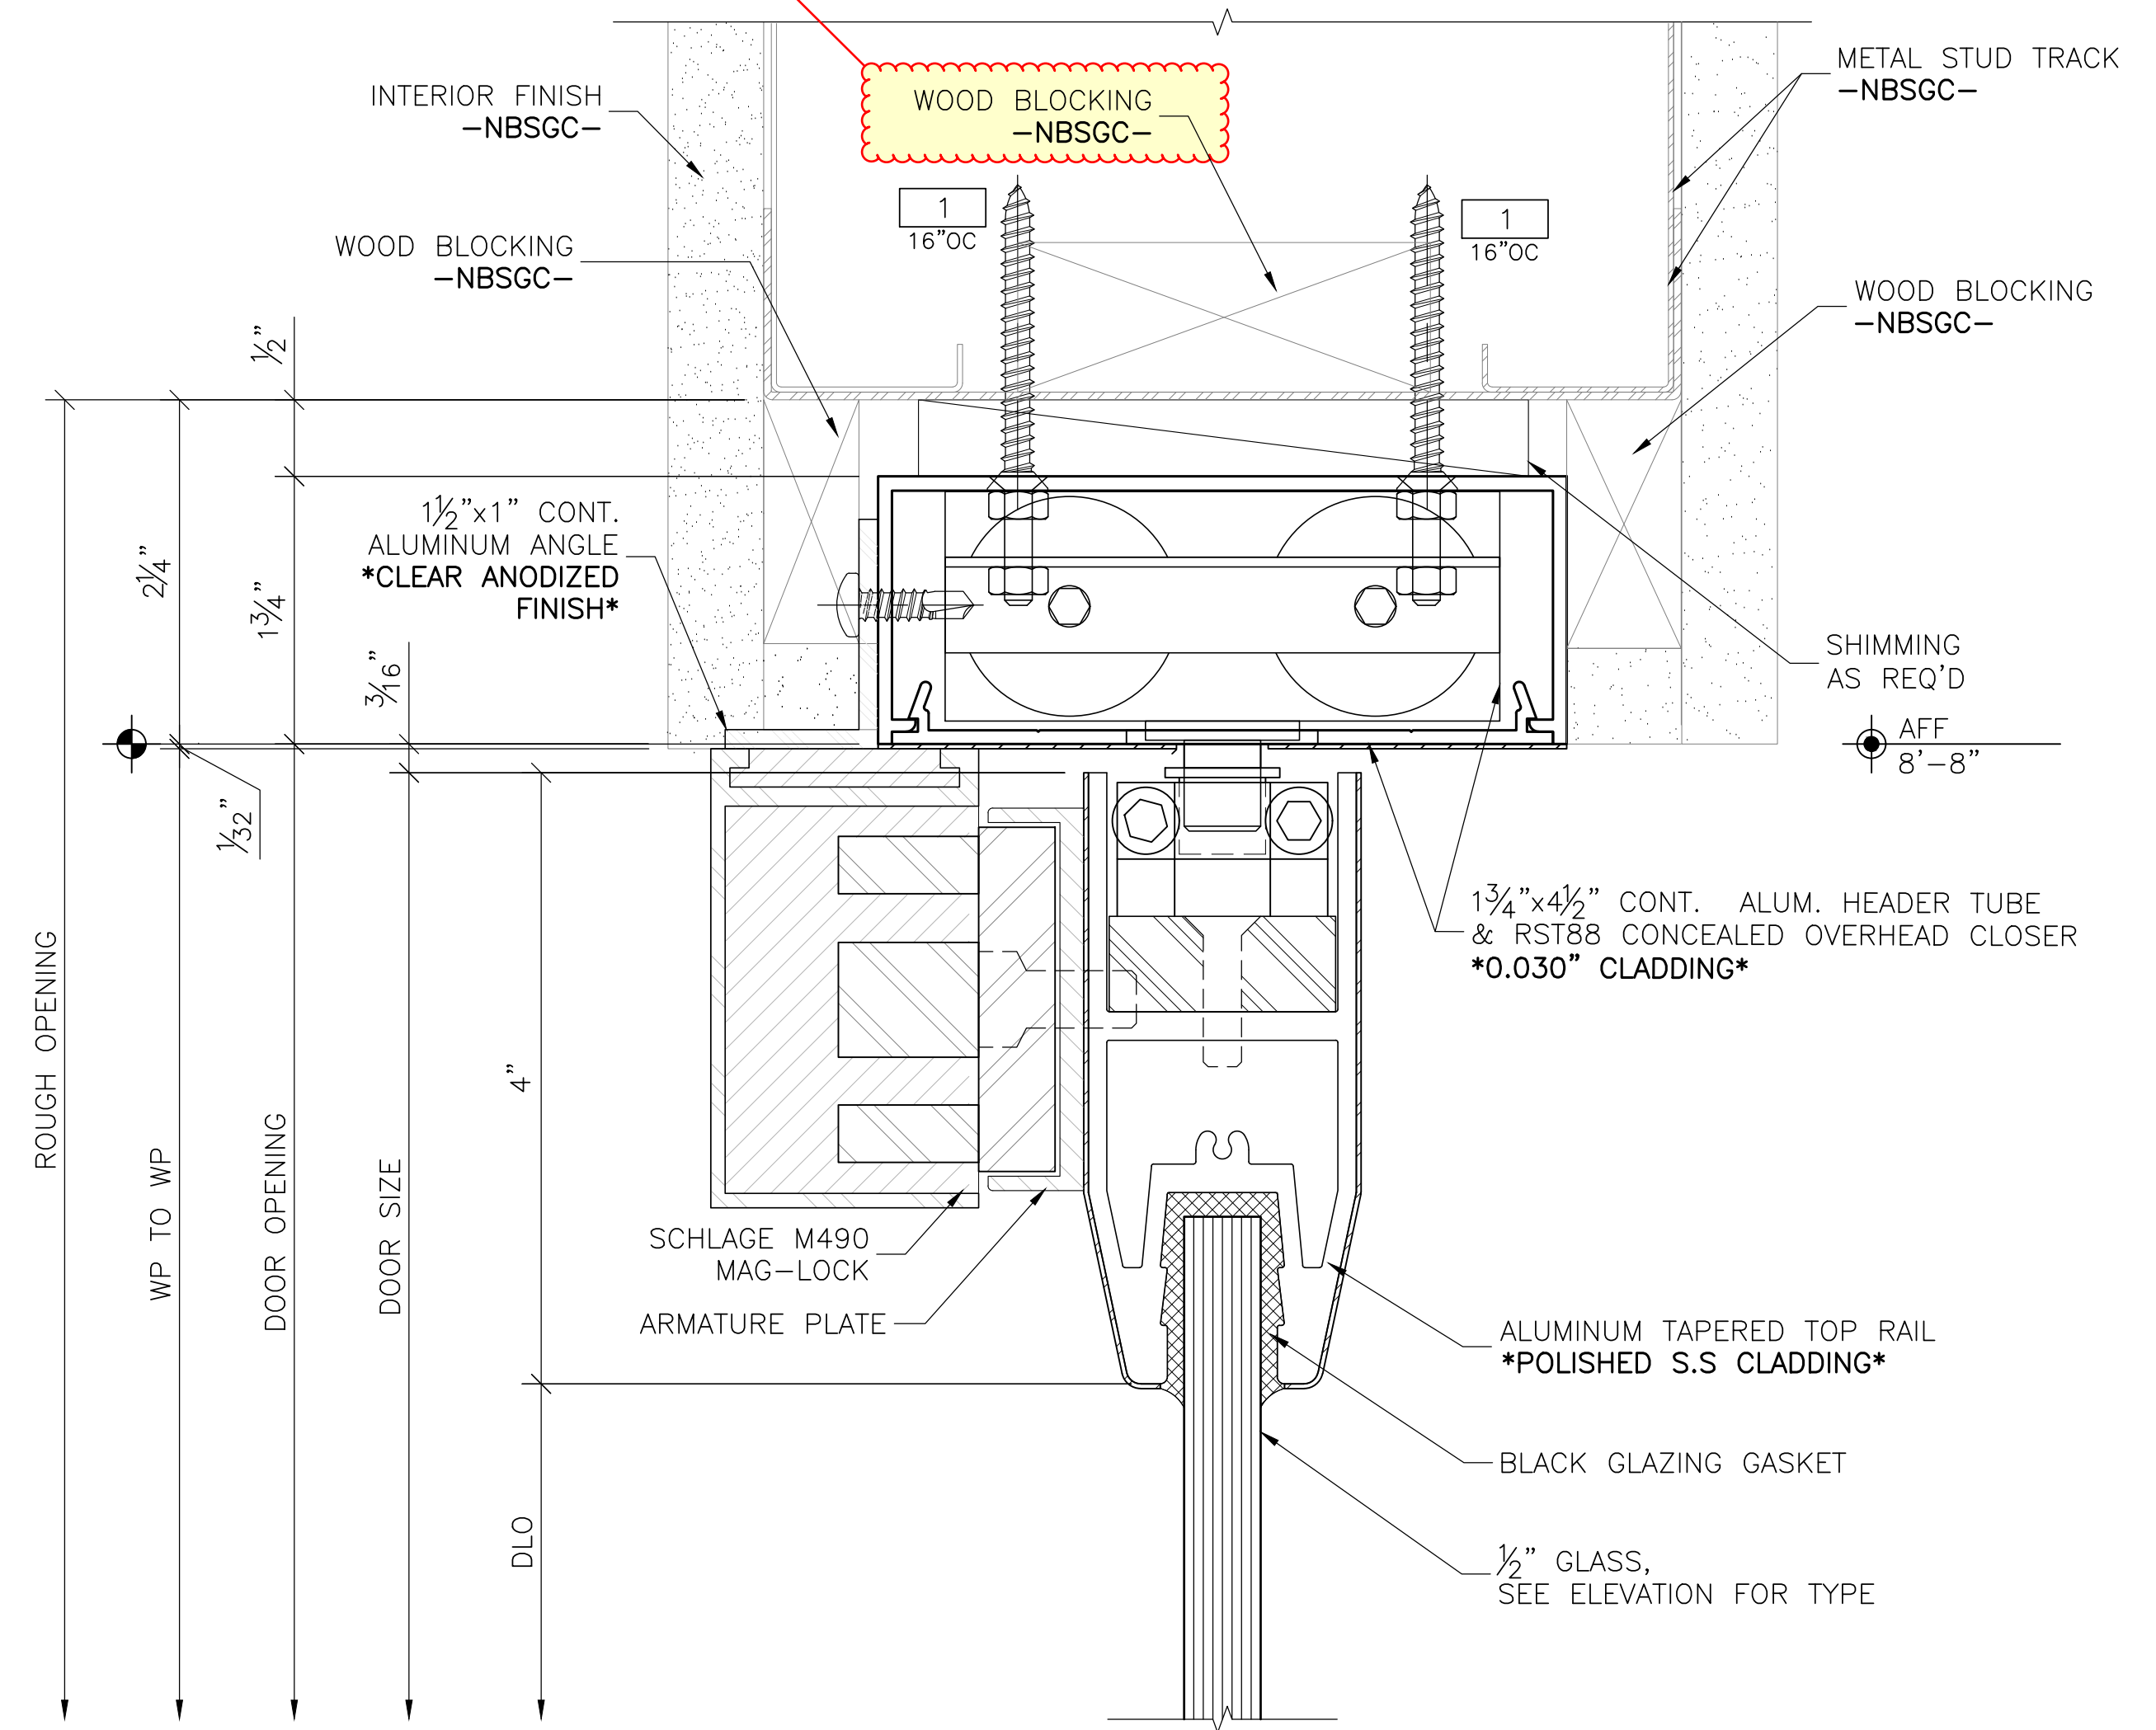

H6
DOOR HEAD DETAIL
W/ CLAD TOP RAIL & HEADER TUBE COC & MAG-LOCK
ARCH REF: 7/A621

DESCRIPTION

BY

DATE

REV

PROJECT
KIRKLAND & ELLIS

ARCHITECT
HO&K

GENERAL CONTRACTOR
STRUCTURE TONE, INC

PROJ NO	8901
DATE	WORKING
DRAWN	SM
CHECKED	SB/MO
FILE NAME	8109 h 1
SCALE	FULL SCALE

SHEET NUMBER	H102
--------------	------



PROJECT		KIRKLAND & ELLIS	REV	DATE	BY	DESCRIPTION
PROJ NO	8901					
DATE	WORKING					
DRAWN	SM					
CHECKED	SB/MO					
FILE NAME	8109 h 1	ARCHITECT				
SCALE	FULL SCALE					
SHEET NUMBER	H103					
GENERAL CONTRACTOR		STRUCTURE TONE, INC				

[illegible]